*Внимание!*

*Ремонт, техническое обслуживание и наладку оборудования, установленного в шахте и на кабине, необходимо производить только после отключения вводного устройства и выключателя SA1 в блоке питания, блока питания – после снятия напряжения с провода L3.*

*Сечение проводов (жил) силовой магистрали*

*Таблица 1*

| *Сечение проводов ПВ3 (жил кабеля КГВЭВ), мм.кв.* | | |
|---|---|---|
| *Q = 500 кг* | *Q = 1000 кг* | *Q = 2000, 3200, 5000, 6300 кг* |
| *2,5* | *2,5* | *6* |

*Таблица 2*

| *участок схемы* | *лист* |
|---|---|
| *Шахтные ленточные провода* | *3* |
| *Подвесные кабели* | *3* |
| *Вводная сеть* | *4* |
| *Лебедки* | *5* |
| *Преобразователь частоты* | *6* |
| *УКС, ВШ, ВК, СПК* | *7* |
| *Упоры* | *8* |
| *Кнопки вызова* | *9* |
| *Индикация на этажах* | *10* |
| *Ограничение доступа* | *11* |
| *Подключение поста приказов* | *12* |
| *Датчики положения* | *13* |
| *Цепь безопасности дверей шахты* | *14* |
| *Устройства безопасности приямка* | *15* |
| *Кабели к панели управления* | *16* |
| *Пост ревизии (кабина)* | *17* |
| *Устройства безопасности кабины* | *18* |
| *Складные перила кабины* | *19* |
| *Освещение кабины* | *20* |
| *Взвешивающее устройство* | *21* |
| *Переговорная связь* | *22* |

*1. Схема выполнена для грузовых лифтов грузоподъемностью до 6300 (включительно) кг со скоростью движения до 0,5 м/с (включительно) и количеством остановок до 24 с ручным открыванием дверей кабины и шахты со следующими видами управления:*

*– наружное с одного (основного) этажа (грузовые лифты),*

*– наружное со всех этажных площадок (грузовые лифты).*

*2. В позиционных обозначениях аппаратов и маркировках проводов буквы, указанные в скобках, означают:*

*"В" – число, соответствующее номеру верхней остановки;*

*"п" – число, соответствующее номеру промежуточных остановок;*

*3. На схеме в скобках указана заводская маркировка проводов и контактов электроаппаратов.*

*4. Монтаж пучков проводов по машинному помещению (МП) к электрооборудованию лифта*

*5. Монтаж пучков проводов электрооборудования кабины вести в металлорукавах.*

*В подвесном кабеле предусмотреть не менее 5% запасных жил.*

*6. Сечение проводов (жил) силовой магистрали см. таблицу 1.*

| | | | | | | |
|---|---|---|---|---|---|---|
| | | | | | ФАИД.484440.002 Э4 | |
| 7 | | 186.013823-2025 | | | Лифт грузовой и больничный с ручными дверьми (наружное управление) Схема электрическая соединений | Лит. / Масса / Масштаб: — / — |
| Изм | Лист | №докум. | Подп. | Дата | | Лист 1 / Листов 34 |
| Разраб. | | Соболев | (Подп) | 15.12.2025 | | ОАО "МОГИЛЕВЛИФТМАШ" ОЛ НТЦ |
| Пров. | | Архангельский | (Подп) | 15.12.2025 | | |
| Т. контр. | | | | | | |
| Э. метр. | | | | | | |
| Н.контр. | | Власович | (Подп) | 16.12.2025 | | |
| Утв. | | Архангельский | (Подп) | 16.12.2025 | | |

Инв.№ подл. 4031 | Подп. и дата Черенкова (Подп) 19.12.2025 | Взам. инв. № | Инв.№ дубл. | Подп. и дата | Справ. №

Перв. примен.

IPS ID: 110655800

Список цехов: расцеховок нет.

Копировал Формат А3

Таблица 3 – Подключение жил в пучках ленточных проводов ПУВПГ-18х0,5, идущих в шахту

| Жила | Жгут ГВ0505.12.00.030 | | | |
|---|---|---|---|---|
| | Пучок 1 | Пучок 2 | Пучок 3 | Пучок 4 |
| | -00 | -01 | -03 | -05*4 |
| 1 | L313 | *1 | 505 | 602 |
| 2 | L312 | *1 | 506 | 652 |
| 3 | L314 | 64 | 507 | 658 |
| 4 | L315 | 70 | P3 | 807 |
| 5 | N3 | 224 | 601 | 857 |
| 6 | 213 | 110 | 651 | 603 |
| 7 | 72 | 022 | 654 | 653 |
| 8 | 74 | 501 | 655 | 659 |
| 9 | 75 | 502 | 656 | |
| 10 | 74-1 | 503 | 657 | |
| 11 | 212 | 504 | 658 | |
| 12 | 163 | 508 | 806 | |
| 13 | 3 | 605 | 856 | 12-7 |
| 14 | -L | 606 | P1 | 12-8 |
| 15 | 438 | 608 | 04-7 | 16-7 |
| 16 | 153 | 609 | 04-8 | 16-8 |
| 17 | 01-7 | 805 | 08-7 | 20-7 |
| 18 | 01-8 | 855 | 08-8 | 20-8 |

Таблица 4 – Подключение жил в трассах подвесных кабелей КПЛ-18х0,75 и КПЛм-6х0,75, идущих в кабину


| Жила | Кабель ГВ0505.12.00.050 | |
|---|---|---|
| | Трасса 4.1 | Трасса 4.2 |
| | -00 | -01 |
| 1 | 63 | 501 |
| 2 | 64 | 502 |
| 3 | 70 | 503 |
| 4 | 71 | 507 |
| 5 | 72 | 508 |
| 6 | 213 | 601 |
| 7 | N | 605 |
| 8 | N3 | 606 |
| 9 | L312 | 609 |
| 10 | L313 | 438 |
| 11 | L315 | 439 |
| 12 | 342 | D1 |
| 13 | 342-1 | D4 |
| 14 | | M1 |
| 15 | 153 | M4 |
| 16 | L318 | 3 |
| 17 | L319 | -L |
| 18 | PE | P3 |

Таблица 5 – Подключение жил в пучках ленточных проводов ПУВПГ-6х0,5, идущих в шахту

Жгут ГВ0505.12.00.010

| Пучок 4 |
|---|
| -02*3 |
| 602 |
| 652 |
| 806 |
| 856 |
| 658 |
| |

Монтаж с использованием зажимов типа "скотчлок"

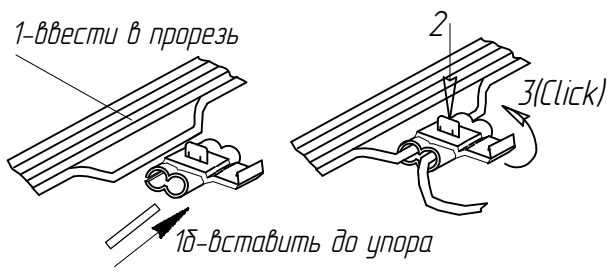


1 – Ввести провода в изоляции в клипсу
2 – Сжать до упора для прокола изоляции
3 – Закрыть крышку до щелчка

Условное обозначение:

*1 – Жилы кабеля 2.1, 2.2, 3.16 на остановках необходимо разрезать.
*3 – Исполнение жгута используется при количестве остановок от 9 до 16.
*4 – Исполнение жгута используется при количестве остановок от 17 до 24.
Указанные жилы используются в качестве перемычек между остановками.
Перемычки с маркировками 04-7, 08-7, 12-7, 16-7, 20-7, проходящие в жиле 2.1 и перемычки 04-8, 08-8, 12-8, 16-8, 20-8, проходящие в жиле 2.2 дополнительно подключить к соответствующим жилам кабеля (см. таблицу 5).

# Подключение подвесных и шахтных кабелей к станции УЛ

ФАИД.484440.002 Э4

А1

Устройство управления УЛ

**ХТ3А**

| Марк. | Конт. |
|---|---|
| 63 | 1 |
| 64 | 2 |
| 75-1 | 3 |
| 75 | 4 |
| 74 | 5 |
| 72 | 6 |
| 71 | 7 |
| 213 | 8 |
| 212 | 9 |
| | 10 |
| 20-8 | 11 |
| 16-8 | 12 |
| 12-8 | 13 |
| 08-8 | 14 |
| 04-8 | 15 |
| 01-8 | 16 |
| 70 | 17 |
| 20-7 | 18 |
| 16-7 | 19 |
| 12-7 | 20 |
| 08-7 | 21 |
| 04-7 | 22 |
| 01-7 | 23 |
| 110 | 24 |
| N1 | 25 |
| 224 | 26 |
| 74-1 | 27 |
| 74-2 | 28 |
| -L | 29 |
| -L | 30 |

**ХТ4А**

| Марк. | Конт. |
|---|---|
| 13' | 1 |
| 13 | 2 |
| 657 | 3 |
| 658 | 4 |
| 659 | 5 |
| 153 | 6 |
| 805 | 7 |
| 806 | 8 |
| 807 | 9 |
| 438 | 10 |
| 855 | 11 |
| 856 | 12 |
| 857 | 13 |
| 3T | 14 |
| 5 | 15 |
| 7 | 16 |
| P3 | 17 |
| P1 | 18 |
| 022 | 19 |
| 163 | 20 |
| 3 | 21 |
| 3 | 22 |
| -L | 23 |
| -L | 24 |

**ХТ4В**

| Марк. | Конт. |
|---|---|
| 501 | 1 |
| 502 | 2 |
| 503 | 3 |
| 504 | 4 |
| 505 | 5 |
| 506 | 6 |
| 507 | 7 |
| 508 | 8 |
| 601 | 9 |
| 602 | 10 |
| 603 | 11 |
| | 12 |
| 605 | 13 |
| 606 | 14 |
| 439 | 15 |
| | 16 |
| 608 | 17 |
| 609 | 18 |
| 651 | 19 |
| 652 | 20 |
| 653 | 21 |
| 654 | 22 |
| 655 | 23 |
| 656 | 24 |

**ХТ2А**

| Марк. | Конт. |
|---|---|
| DS1 | 1 |
| DS0 | 2 |
| D1 | 3 |
| 361 | 4 |
| L313 | 5 |
| N3 | 6 |
| 362 | 7 |
| L123 | 8 |
| L124 | 9 |
| 348 | 10 |
| 342 | 11 |
| N | 12 |
| 342-1 | 13 |
| 349 | 14 |
| L312 | 15 |
| L314 | 16 |
| L315 | 17 |
| L318 | 18 |
| L319 | 19 |
| | 20 |
| | 21 |
| | 22 |
| L160 | 23 |
| L161 | 24 |
| N | 25 |
| L311 | 26 |
| D1 | 27 |
| D4 | 28 |
| M1 | 29 |
| M4 | 30 |
| | 31 |
| | 32 |
| | 33 |

В диспетчерский пункт

ГВ0505.12.00.050-00 — 4.1

ГВ0505.12.00.050-01 — 4.2

В кабину

ГВ0505.12.00.030-00 — 1

ГВ0505.12.00.030-01 — 2

ГВ0505.12.00.030-03 — 3

ГВ0505.12.00.030-05 *4 или ГВ0505.12.00.010-02 *3 — 4

В шахту

*3 – Исполнение жгута используется при количестве остановок от 9 до 16.

*4 – Исполнение жгута используется при количестве остановок от 17 до 24.

| Изм | Лист | № докум. | Подп. | Дата | ФАИД.484440.002 Э4 | Лист 3 |
|---|---|---|---|---|---|---|
| 7 | | 186.013823-2025 | | | | |

Перв. примен.

Справ. №

Подп. и дата

Инв.№ подл. 4031 | Подп. и дата (Подп) Черенкова 19.12.2025 | Взам. инв. № | Инв.№ дубл. | Подп. и дата


IPS ID: 110655800

Список цехов: расцеховок нет.

Копировал

Формат А3

# Вводная сеть (с машинным помещением)

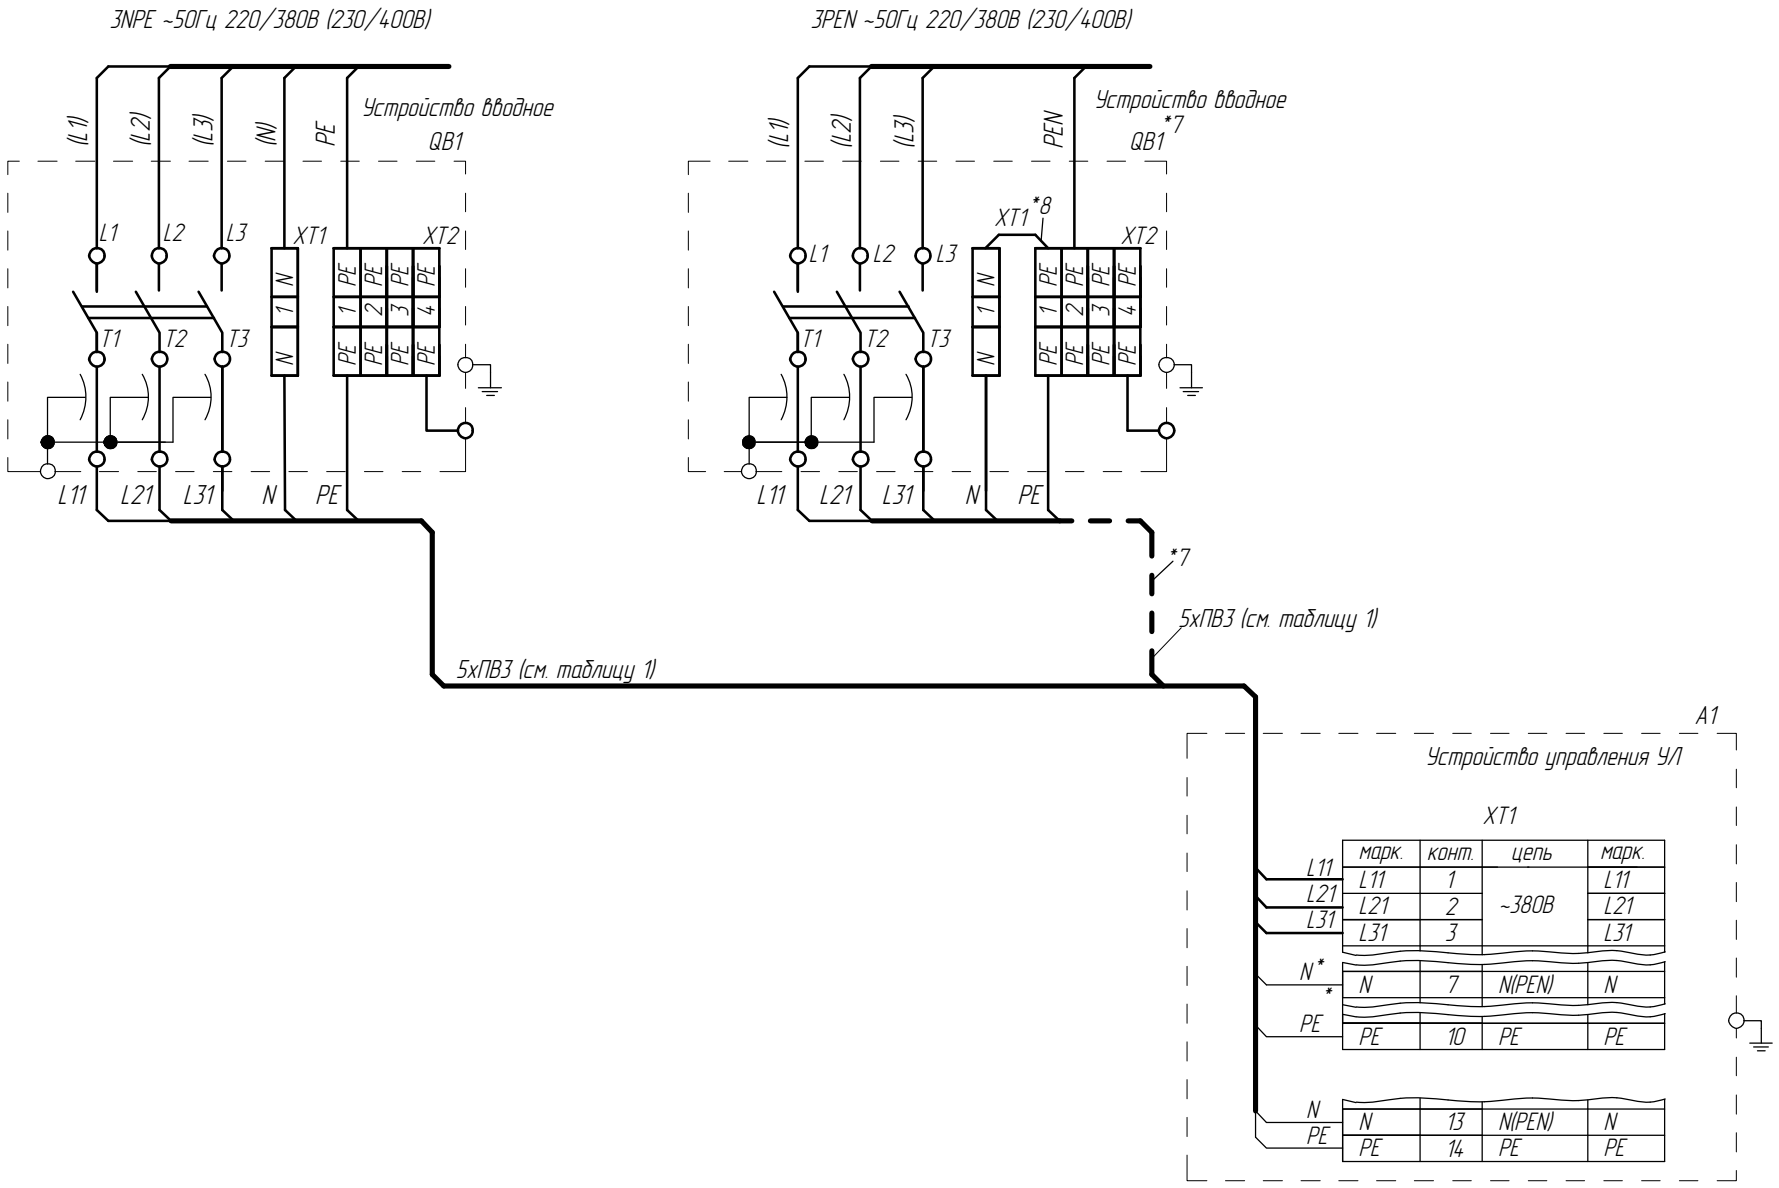


* Клеммная коробка XT1 показана для варианта исполнения станции со встроенным преобразователем частоты

*7 При питаниии от сети TN-C

*8 ПВ3, сечение не менее сечения PEN

| Изм | Лист | № докум. | Подп. | Дата | ФАИД.484440.002 Э4 | Лист 4 |
|---|---|---|---|---|---|---|
| 7 | | 186.013823-2025 | | | | |


Инв.№ подл. 4031 | Подп. и дата Черенкова (Подп) 19.12.2025 | Взам. инв. № | Инв.№ дубл. | Подп. и дата

Справ. №


Перв. примен.

IPS ID: 110655800 | Список цехов: расцеховок нет. | Копировал | Формат А3

## Асинхронный привод

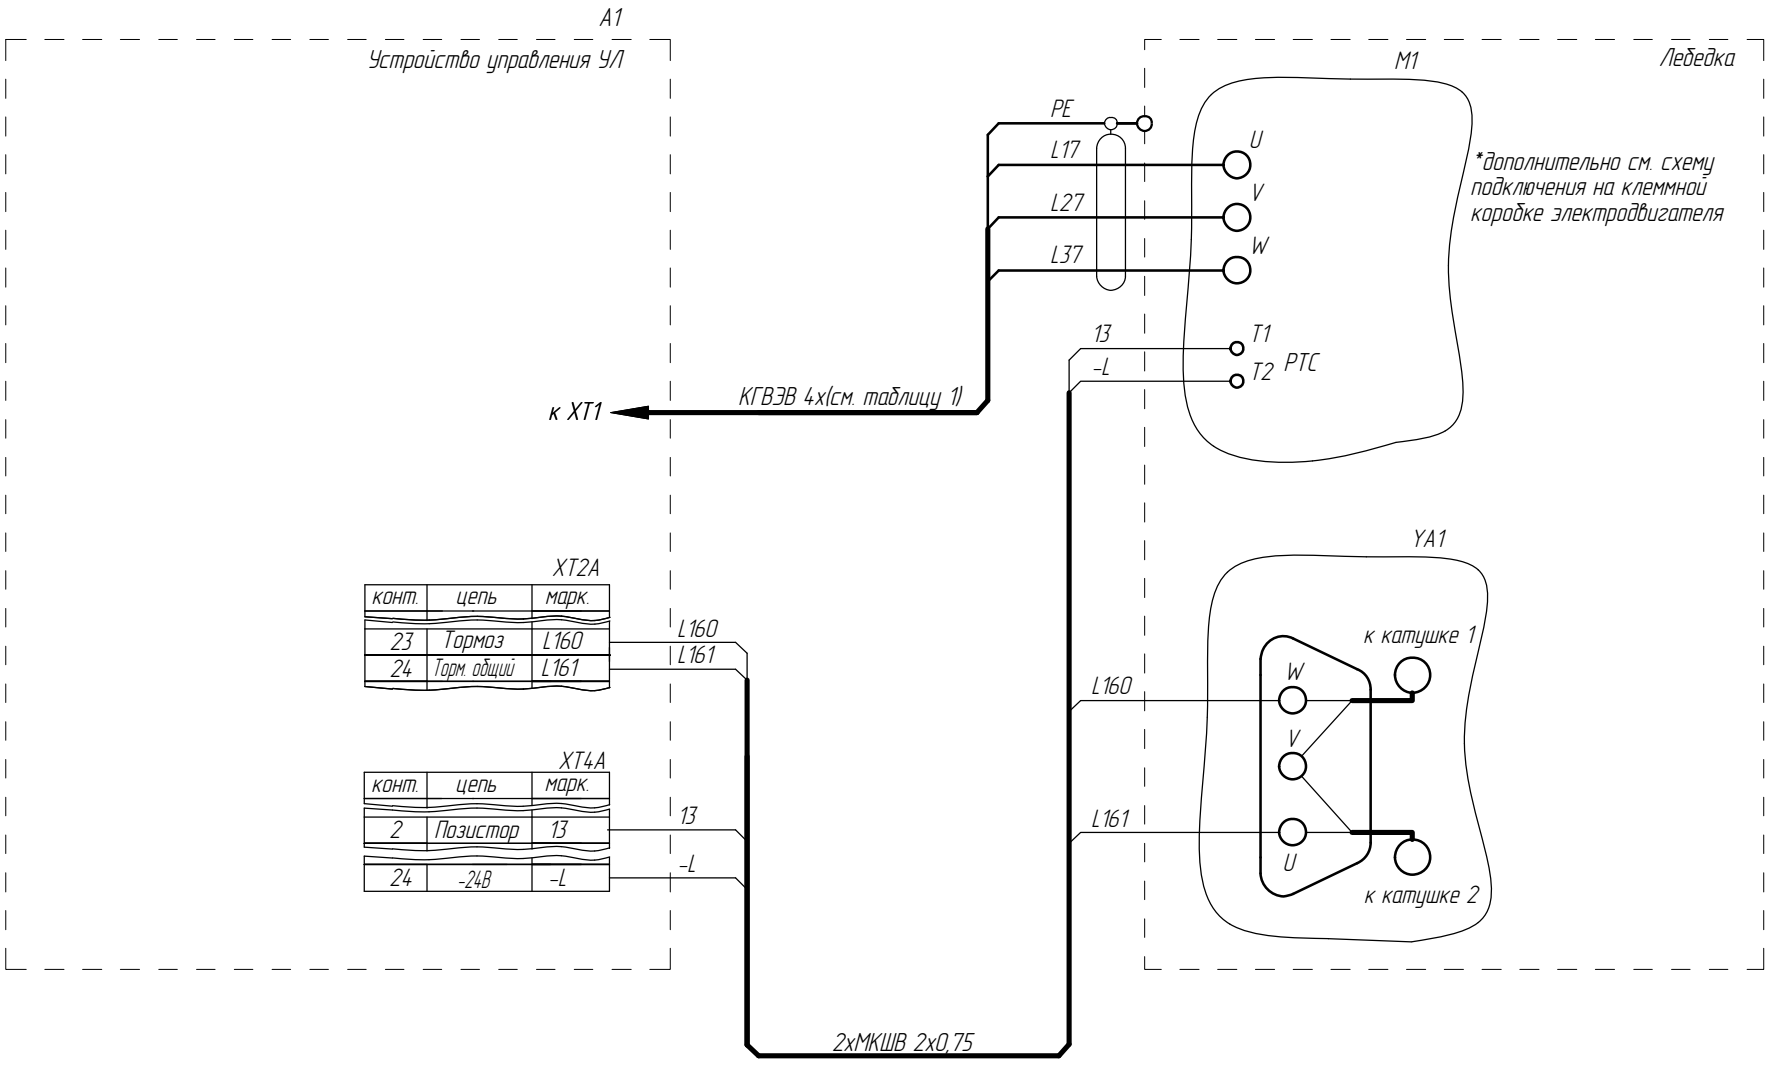


## Асинхронный привод с тормозом на тихоходном валу

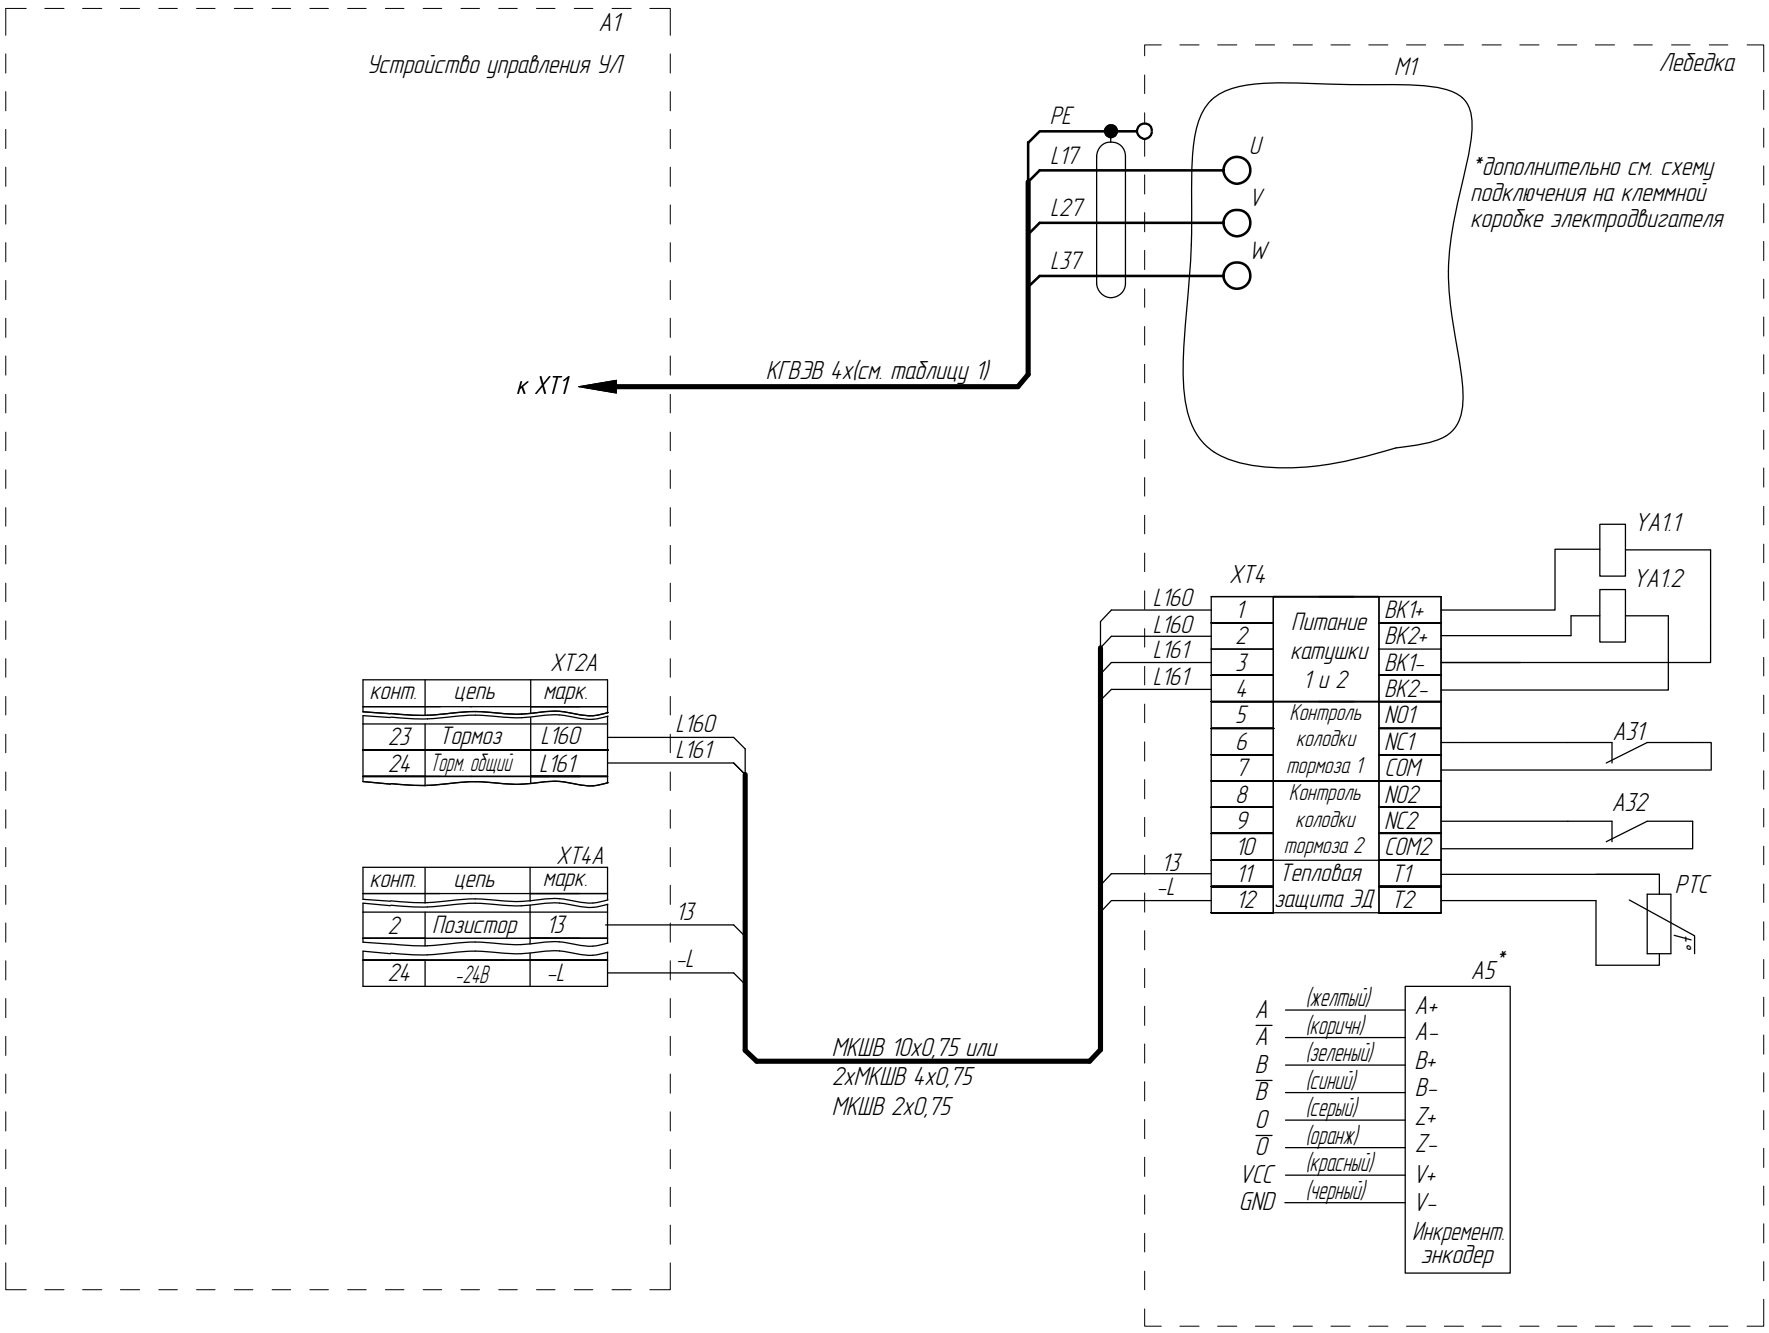



Раму лебедки заземлить

| Изм | Лист | № докум. | Подп. | Дата | 186.013823-2025 | ФАИД.484440.002 Э4 | Лист 5 |
|---|---|---|---|---|---|---|---|

Инв.№ подл. 4031 | Подп. и дата Черенкова (Подп) 19.12.2025 | Взам. инв. № | Инв.№ дубл. | Подп. и дата | Справ. №

# Регулятор скорости (не встроен в устройство УЛ)
# Yaskawa L1000A

ФАИД.484440.002 Э4

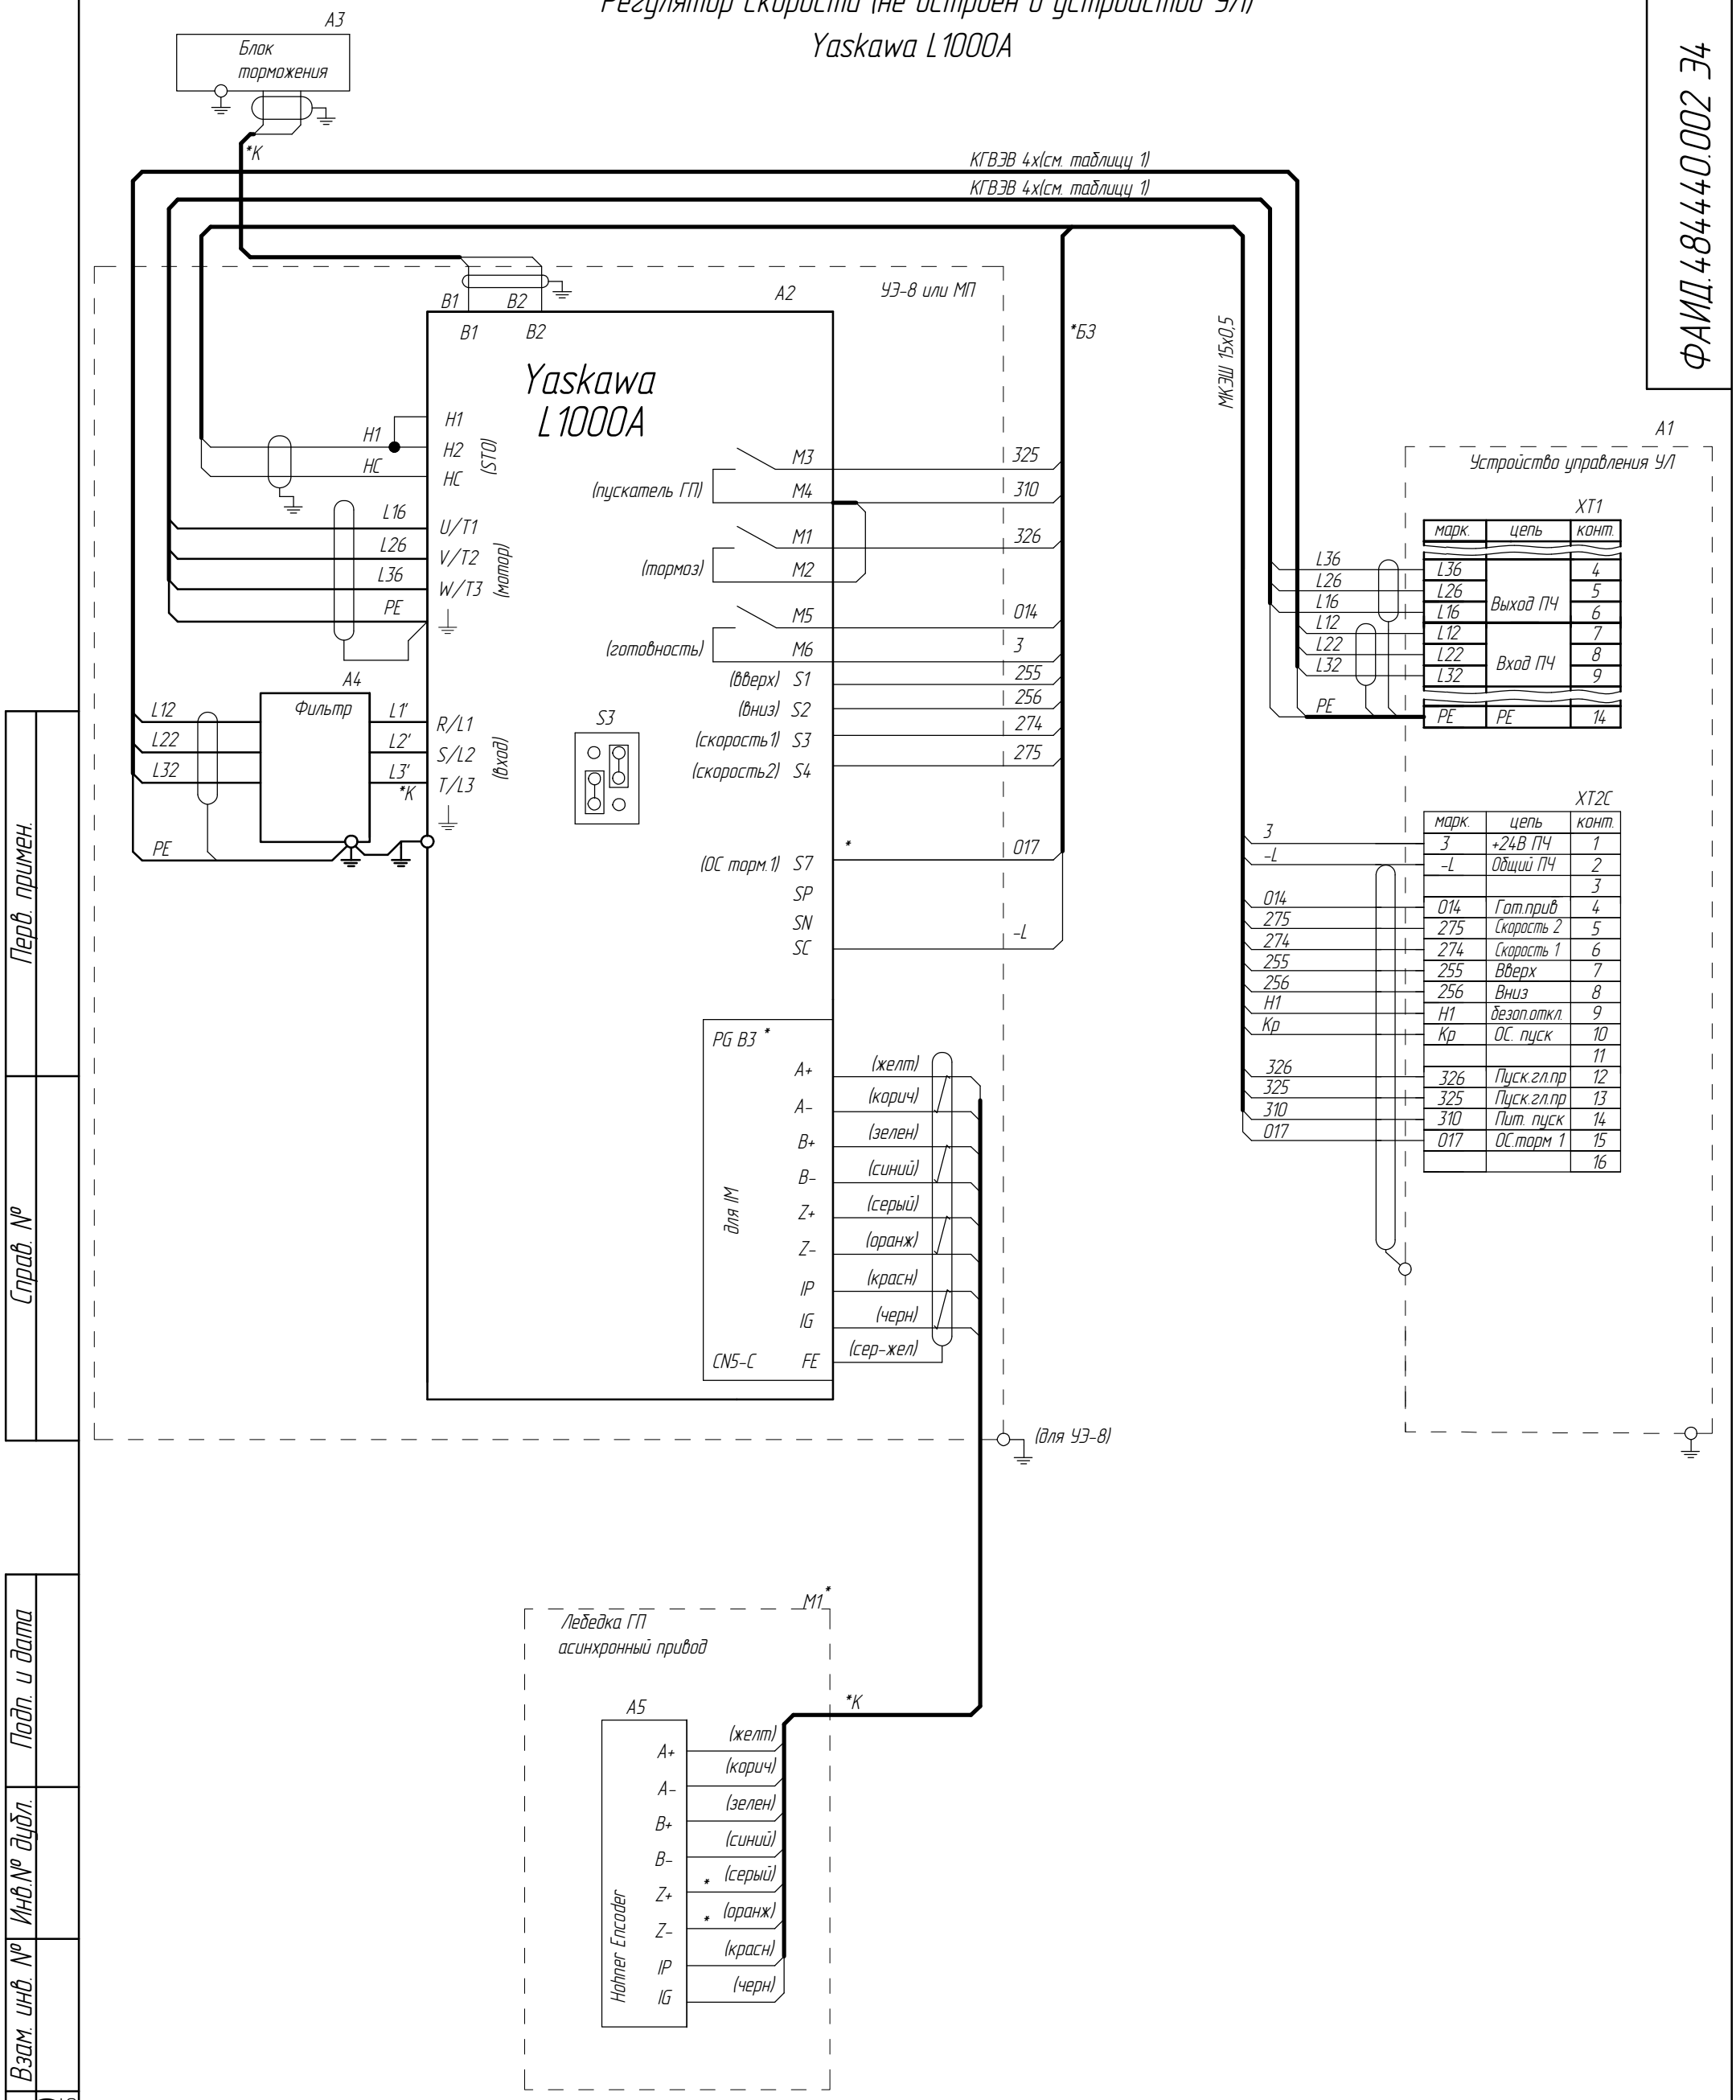


*Б3 - экран кабеля со стороны частотного преобразователя не заземлять

* - наличие зависит от исполнения аппаратов или устройств

| Изм | Лист | № докум. | Подп. | Дата | ФАИД.484440.002 Э4 | Лист 6 |
|---|---|---|---|---|---|---|
| 7 | | 186.013823-2025 | | | | |

Перв. примен.

Справ. №

Подп. и дата

Инв.№ дубл.

Взам. инв. №

Подп. и дата 19.12.2025 Черенкова (Подп)

Инв.№ подл. 4031

IPS ID: 110655800


Список цехов-расцеховок нет.

Копировал

Формат А3

# Преобразователь частоты (не встроен в устройство УЛ)
# HPMONT HD5L

ФАИД.484440.002 Э4

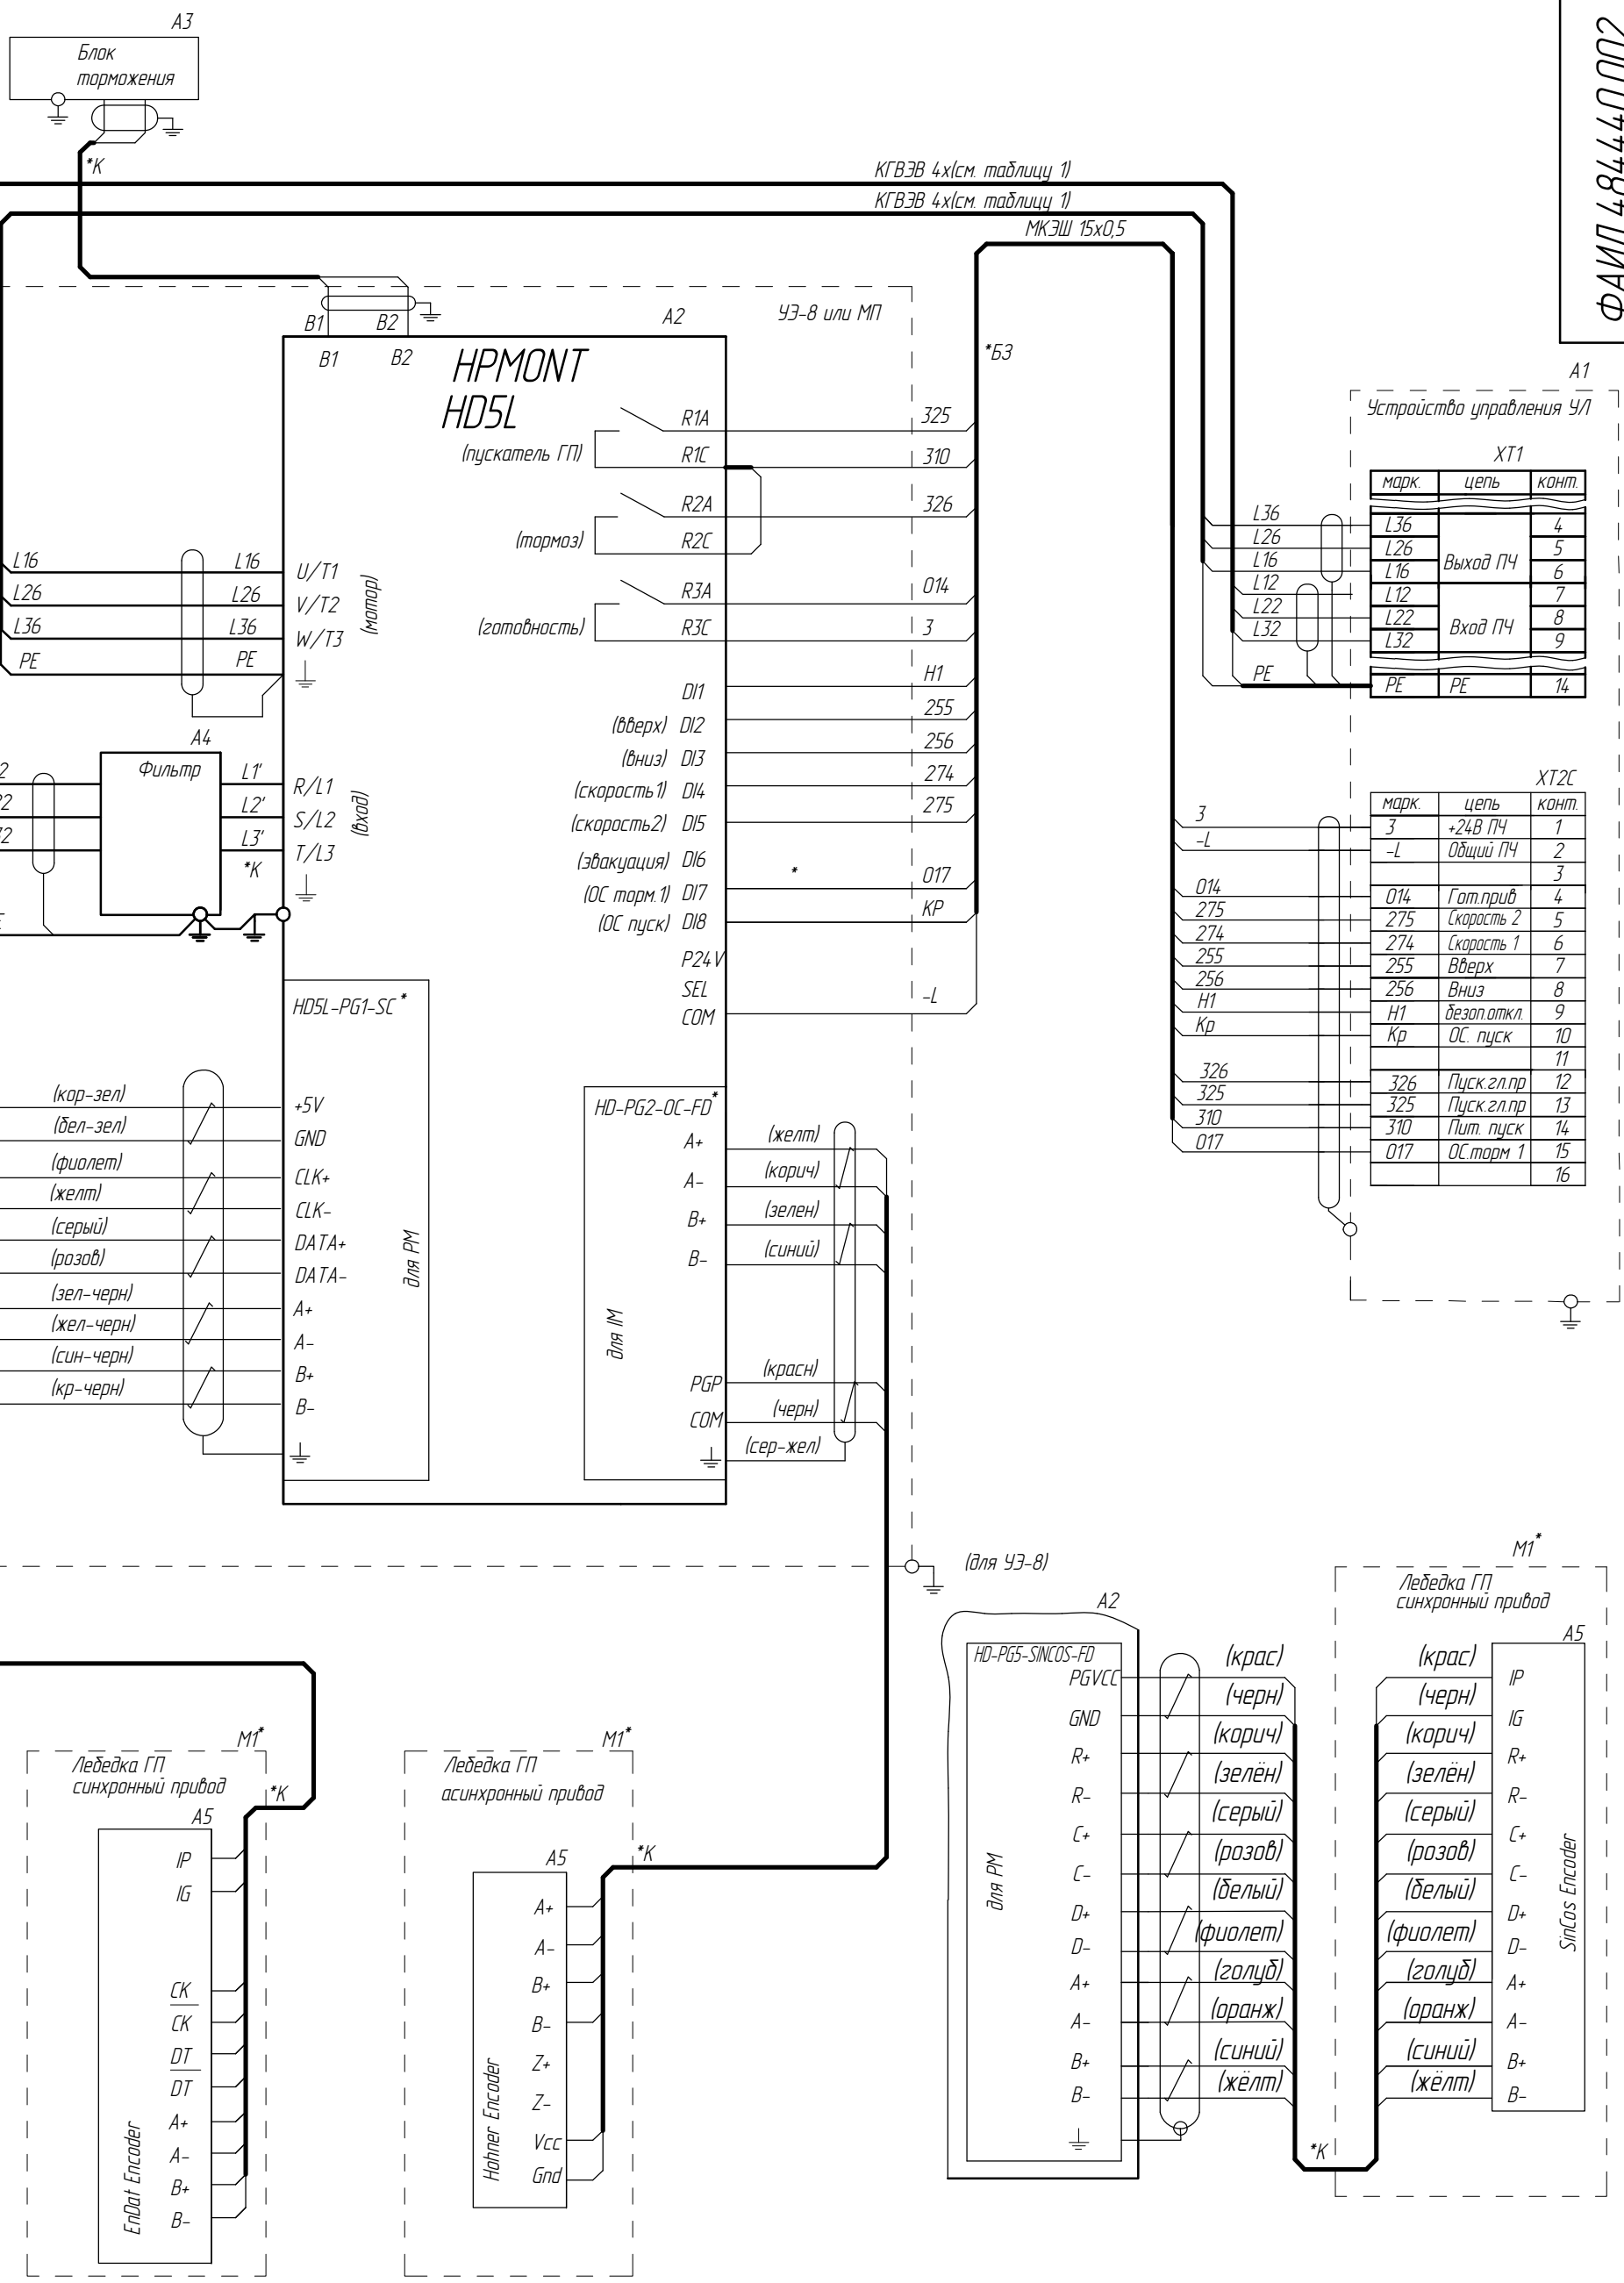


*Б3 – экран кабеля со стороны частотного преобразователя не заземлять

* – наличие зависит от исполнения аппаратов или устройств

*К – кабель в комплекте с устройством

| Изм | Лист | № докум. | Подп. | Дата | ФАИД.484440.002 Э4 | Лист 6а |
|---|---|---|---|---|---|---|
| 7 | | 186.013823-2025 | | | | |

Инв.№ подл. 4031 | Подп. и дата Черенкова (Подп) 19.12.2025 | Взам. инв. № | Инв.№ дубл. | Подп. и дата | Справ. № | Перв. примен.


IPS ID: 110655800

Список цехов-расцеховок нет.

Копировал Формат А3

# Преобразователь частоты (не встроен в устройство УЛ)
# HPMONT HD5L PLUS

ФАИД.484440.002 Э4

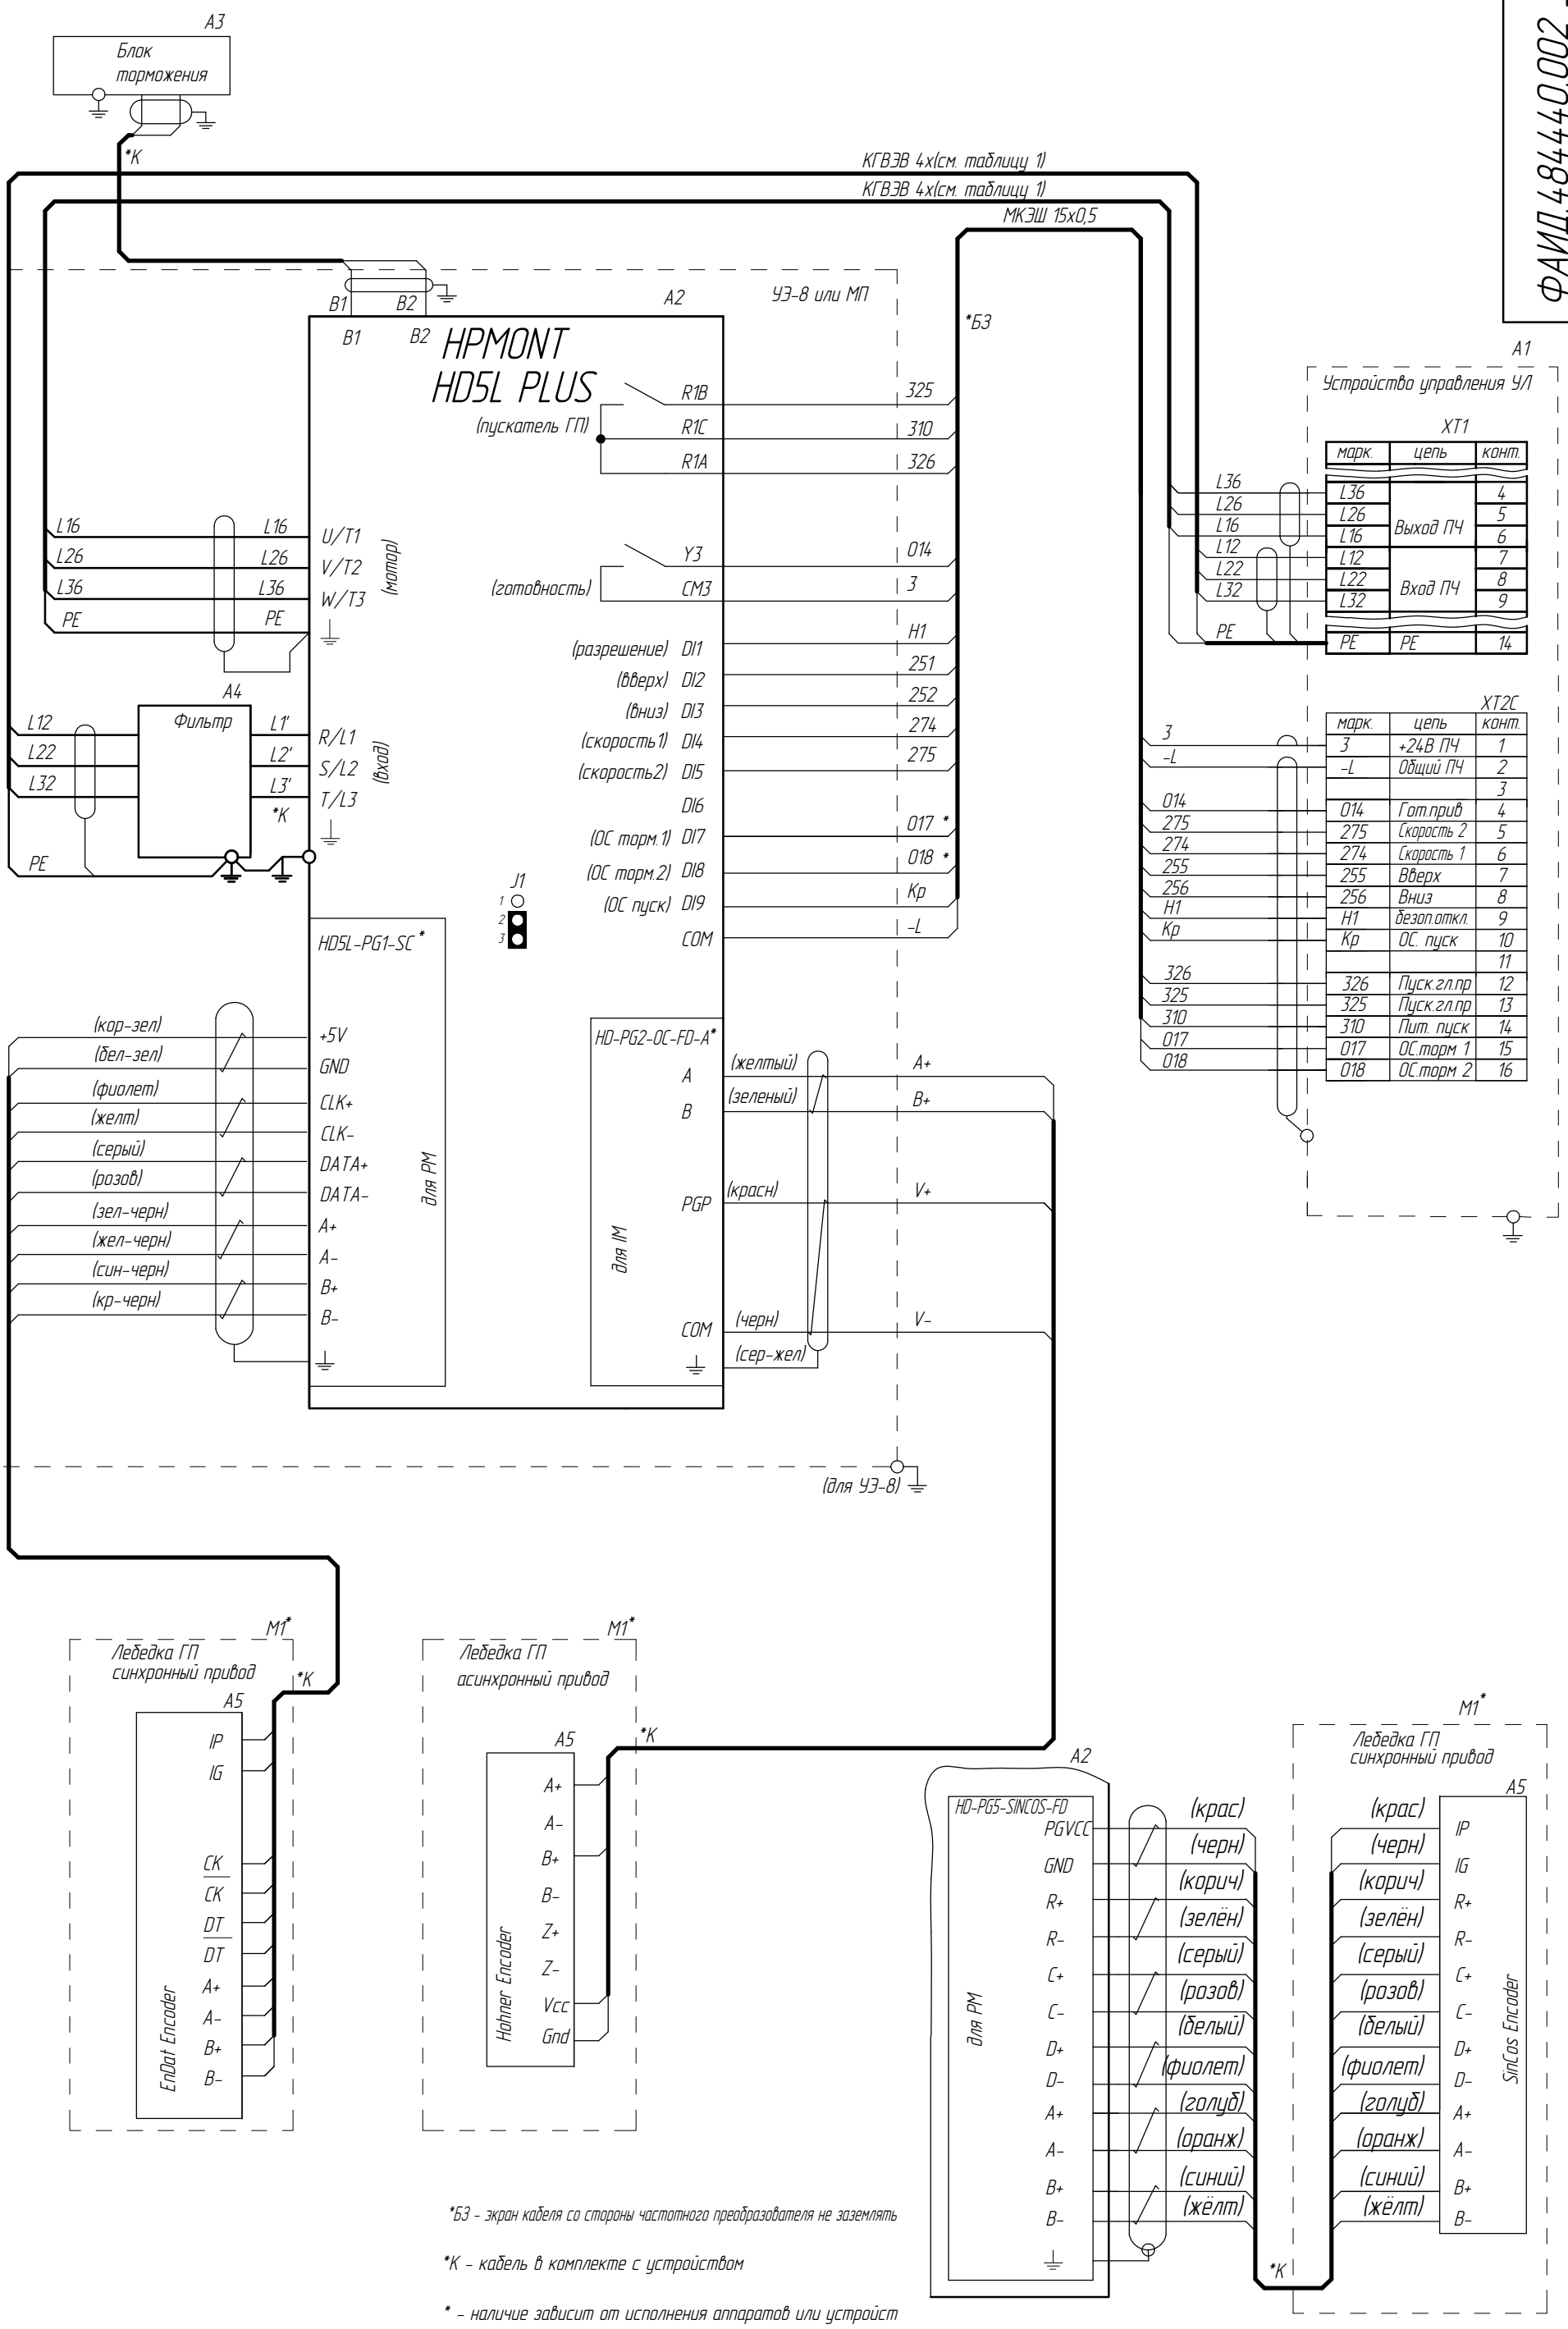


*Б3 - экран кабеля со стороны частотного преобразователя не заземлять

*К - кабель в комплекте с устройством

* - наличие зависит от исполнения аппаратов или устройст

| Изм | Лист | № докум. | Подп. | Дата | ФАИД.484440.002 Э4 | Лист 6б |
|---|---|---|---|---|---|---|
| 7 | | 186.013823-2025 | | | | |

Перв. примен.

Справ. №

Подп. и дата

Инв.№ дубл.

Взам. инв. №

Подп. и дата 19.12.2025 (Подп.) Черенкова

Инв.№ подл. 4031

IPS ID: 110655800

Список цехов: расцеховок нет.

Копировал

Формат А3

# Преобразователь частоты (не встроен в устройство УЛ)
# INVT Goodrive GD300L

ФАИД.484440.002 Э4

А3 Блок торможения

*К

КГВЭВ 4х(см. таблицу 1)

КГВЭВ 4х(см. таблицу 1)

МКЭШ 15х0,5

*Б3

А2 INVT Goodrive GD300L

УЭ-8 или МП

В1 В2 + РВ

RO1A (пускатель ГП) RO1C — 325, 310

RO2A (тормоз) RO2C — 326

RO3A (готовность) RO3C — 014, 3

(разрешение) S1 — Н1

(вверх) S2 — 251

(вниз) S3 — 252

(скорость1) S4 — 274

(скорость2) S5 — 275

(ОС пускателя) S6 — Кр

(ОС торм.1) S7 — 017 *

(ОС торм.2) S8 — 018 *

COM — -L

24V

L16 L26 L36 PE — U V W (мотор) — L16 L26 L36 PE

А4 Фильтр

L12 L22 L32 — L1' L2' L3' — R S T (вход) — *К

PE

EC-PG106-05-T (EnDAT)

(кор-зел) PWR
(бел-зел) GND
(фиолет) CLK+
(желт) CLK-
(серый) DATA+
(розов) DATA-
(зел-черн) A+
(жел-черн) A-
(син-черн) B+
(кр-черн) B-

для СД

EC-PG101-12(-24)

IA+ (корич) A-
IA- (синий) B-
IB+ (жёлт) A+
IB- (зелён) B+
IZ+ (серый) B+
IZ- (оранж.) B+
PWR (красн) V+
COM1 (черн) V-
(сер-жел)

для АД

(для УЭ-8)

А1 Устройство управления УЛ

ХТ1

| марк. | цепь | конт. |
|---|---|---|
| L36 | Выход ПЧ | 4 |
| L26 | | 5 |
| L16 | | 6 |
| L12 | Вход ПЧ | 7 |
| L22 | | 8 |
| L32 | | 9 |
| PE | PE | 14 |

ХТ2С

| марк. | цепь | конт. |
|---|---|---|
| 3 | +24В ПЧ | 1 |
| -L | Общий ПЧ | 2 |
| | | 3 |
| 014 | Гот.прив | 4 |
| 275 | Скорость 2 | 5 |
| 274 | Скорость 1 | 6 |
| 255 | Вверх | 7 |
| 256 | Вниз | 8 |
| Н1 | безоп.откл. | 9 |
| Кр | ОС. пуск | 10 |
| | | 11 |
| 326 | Пуск.гл.пр | 12 |
| 325 | Пуск.гл.пр | 13 |
| 310 | Пит. пуск | 14 |
| | | 15 |
| 017 | ОС.торм 1 | 16 |
| 018 | ОС.торм 2 | 17 |

M1* Лебедка ГП синхронный привод — А5 EnDat Encoder: IP IG CK /CK DT /DT A+ A- B+ B- — *К

M1* Лебедка ГП асинхронный привод — А5 Hohner Encoder: A+ A- B+ B- Z+ Z- Vcc Gnd — *К

А2 EC-PG102-05-T (SinCos) для СД: PWR GND R+ R- D+ D- C+ C- B+ B- A+ A-

(крас) (черн) (корич) (зелён) (серый) (розов) (белый) (фиолет) (голуб) (оранж) (синий) (жёлт) — *К

M1* Лебедка ГП синхронный привод — А5 SinCos Encoder: IP IG R+ R- C+ C- D+ D- A+ A- B+ B-

*Б3 - экран кабеля со стороны частотного преобразователя не заземлять

*К - кабель в комплекте с устройством

* - наличие зависит от исполнения аппаратов или устройст

| Изм | Лист | № докум. | Подп. | Дата | 186.013823-2025 | ФАИД.484440.002 Э4 | Лист 6в |
|---|---|---|---|---|---|---|---|

Перв. примен.

Справ. №

Подп. и дата

Инв.№ дубл.

Взам. инв. №

Подп. и дата (Подп) Черенкова 19.12.2025

Инв.№ подл. 4031

IPS ID: 110655800

Список цехов:расцеховок нет.

Копировал

Формат А3

# Подключение устройства контроля скорости (УКС), ВШ, ВК, СПК для лифтов с верхним машинным помещением

ФАИД.484440.002 Э4

Машинное помещение

Устройство управления УЛ

XT3A

| марк. | конт. | цепь | марк. |
|---|---|---|---|
| 63 | 1 | Кн.шунт.ДШ | 63 |
| 64 | 2 | ДШэ | 64 |
| 75-1 | 3 | БОС | 75-1 |
| 75 | 4 | ВШ,ВОС | 75 |
| 74 | 5 | ВК | 74 |
| 72 | 6 | ВУ | 72 |
| 71 | 7 | "СТОП" | 71 |
| 213 | 8 | ВЛ | 213 |
| 212 | 9 | ДШп | 212 |

| | | | |
|---|---|---|---|
| 74-1 | 27 | СПК' | 74-1 |
| 74-2 | 28 | СПК' | 74-2 |

XT4A

| марк. | конт. | цепь | марк. |
|---|---|---|---|
| 5 | 15 | Вых.датч | 5 |
| 7 | 16 | +12В Датч | 7 |
| -L | 23 | Общий 24В | -L |

Ограничитель скорости

ВОС SE20 — 74-2, 75 — Выключатель ограничителя скорости

ВК SE5 — 74, 74-1 — Выключатель конечный переспуска/переподъёма кабины

МКШВ 2х0,5

A7 УКС

| | марк. |
|---|---|
| 7 | BROWN |
| -L | BLUE |
| 5 | BLACK |

A24* Энкодер 1020БК.07.00.100

XT1

| | к. | марк. |
|---|---|---|
| 7 | 1 | +12V |
| -L | 2 | 0V |

XT2

| | к. | марк. |
|---|---|---|
| 5 | 1 | DA |
| | 2 | DB |

A28* Индуктивный датчик

| | марк. |
|---|---|
| 7 | BROWN |
| -L | BLUE |
| 5 | BLACK |

СПК SE3*9 — 74-1, 74-2 — Выключатель слабины подъемных канатов (для Q>500 кг)

ВШ SE19 — 75-1, 75 — Выключатель штурвала

ВК SE5*ГВ05 — 74, 74-1 — Выключатель конечный переспуска/переподъёма кабины

* – наличие зависит от исполнения аппаратов или устройств

*ГВ05 – для лифтов модели ГВ0505

*9 – Выключатель SE3 (СПК) для лифтов с верхним МП устанавливается для Q = 500 кг на кабине, для Q > 500 кг – в машинном помещении (МП).

| Изм | Лист | № докум. | Подп. | Дата |
|---|---|---|---|---|
| 7 | | 186.013823-2025 | | |

ФАИД.484440.002 Э4

Лист 7

Перв. примен.

Справ. №

Подп. и дата

Инв.№ подл. 4031

Подп. и дата (Подп) Черенкова 19.12.2025

Взам. инв. №

Инв.№ дубл.

Подп. и дата


IPS ID: 110655800

Список цехов-расцеховок нет.

Копировал

Формат А3

# Подключение устройства контроля скорости (УКС), ВШ, ВК,СПК для лифтов с нижним машинным помещением

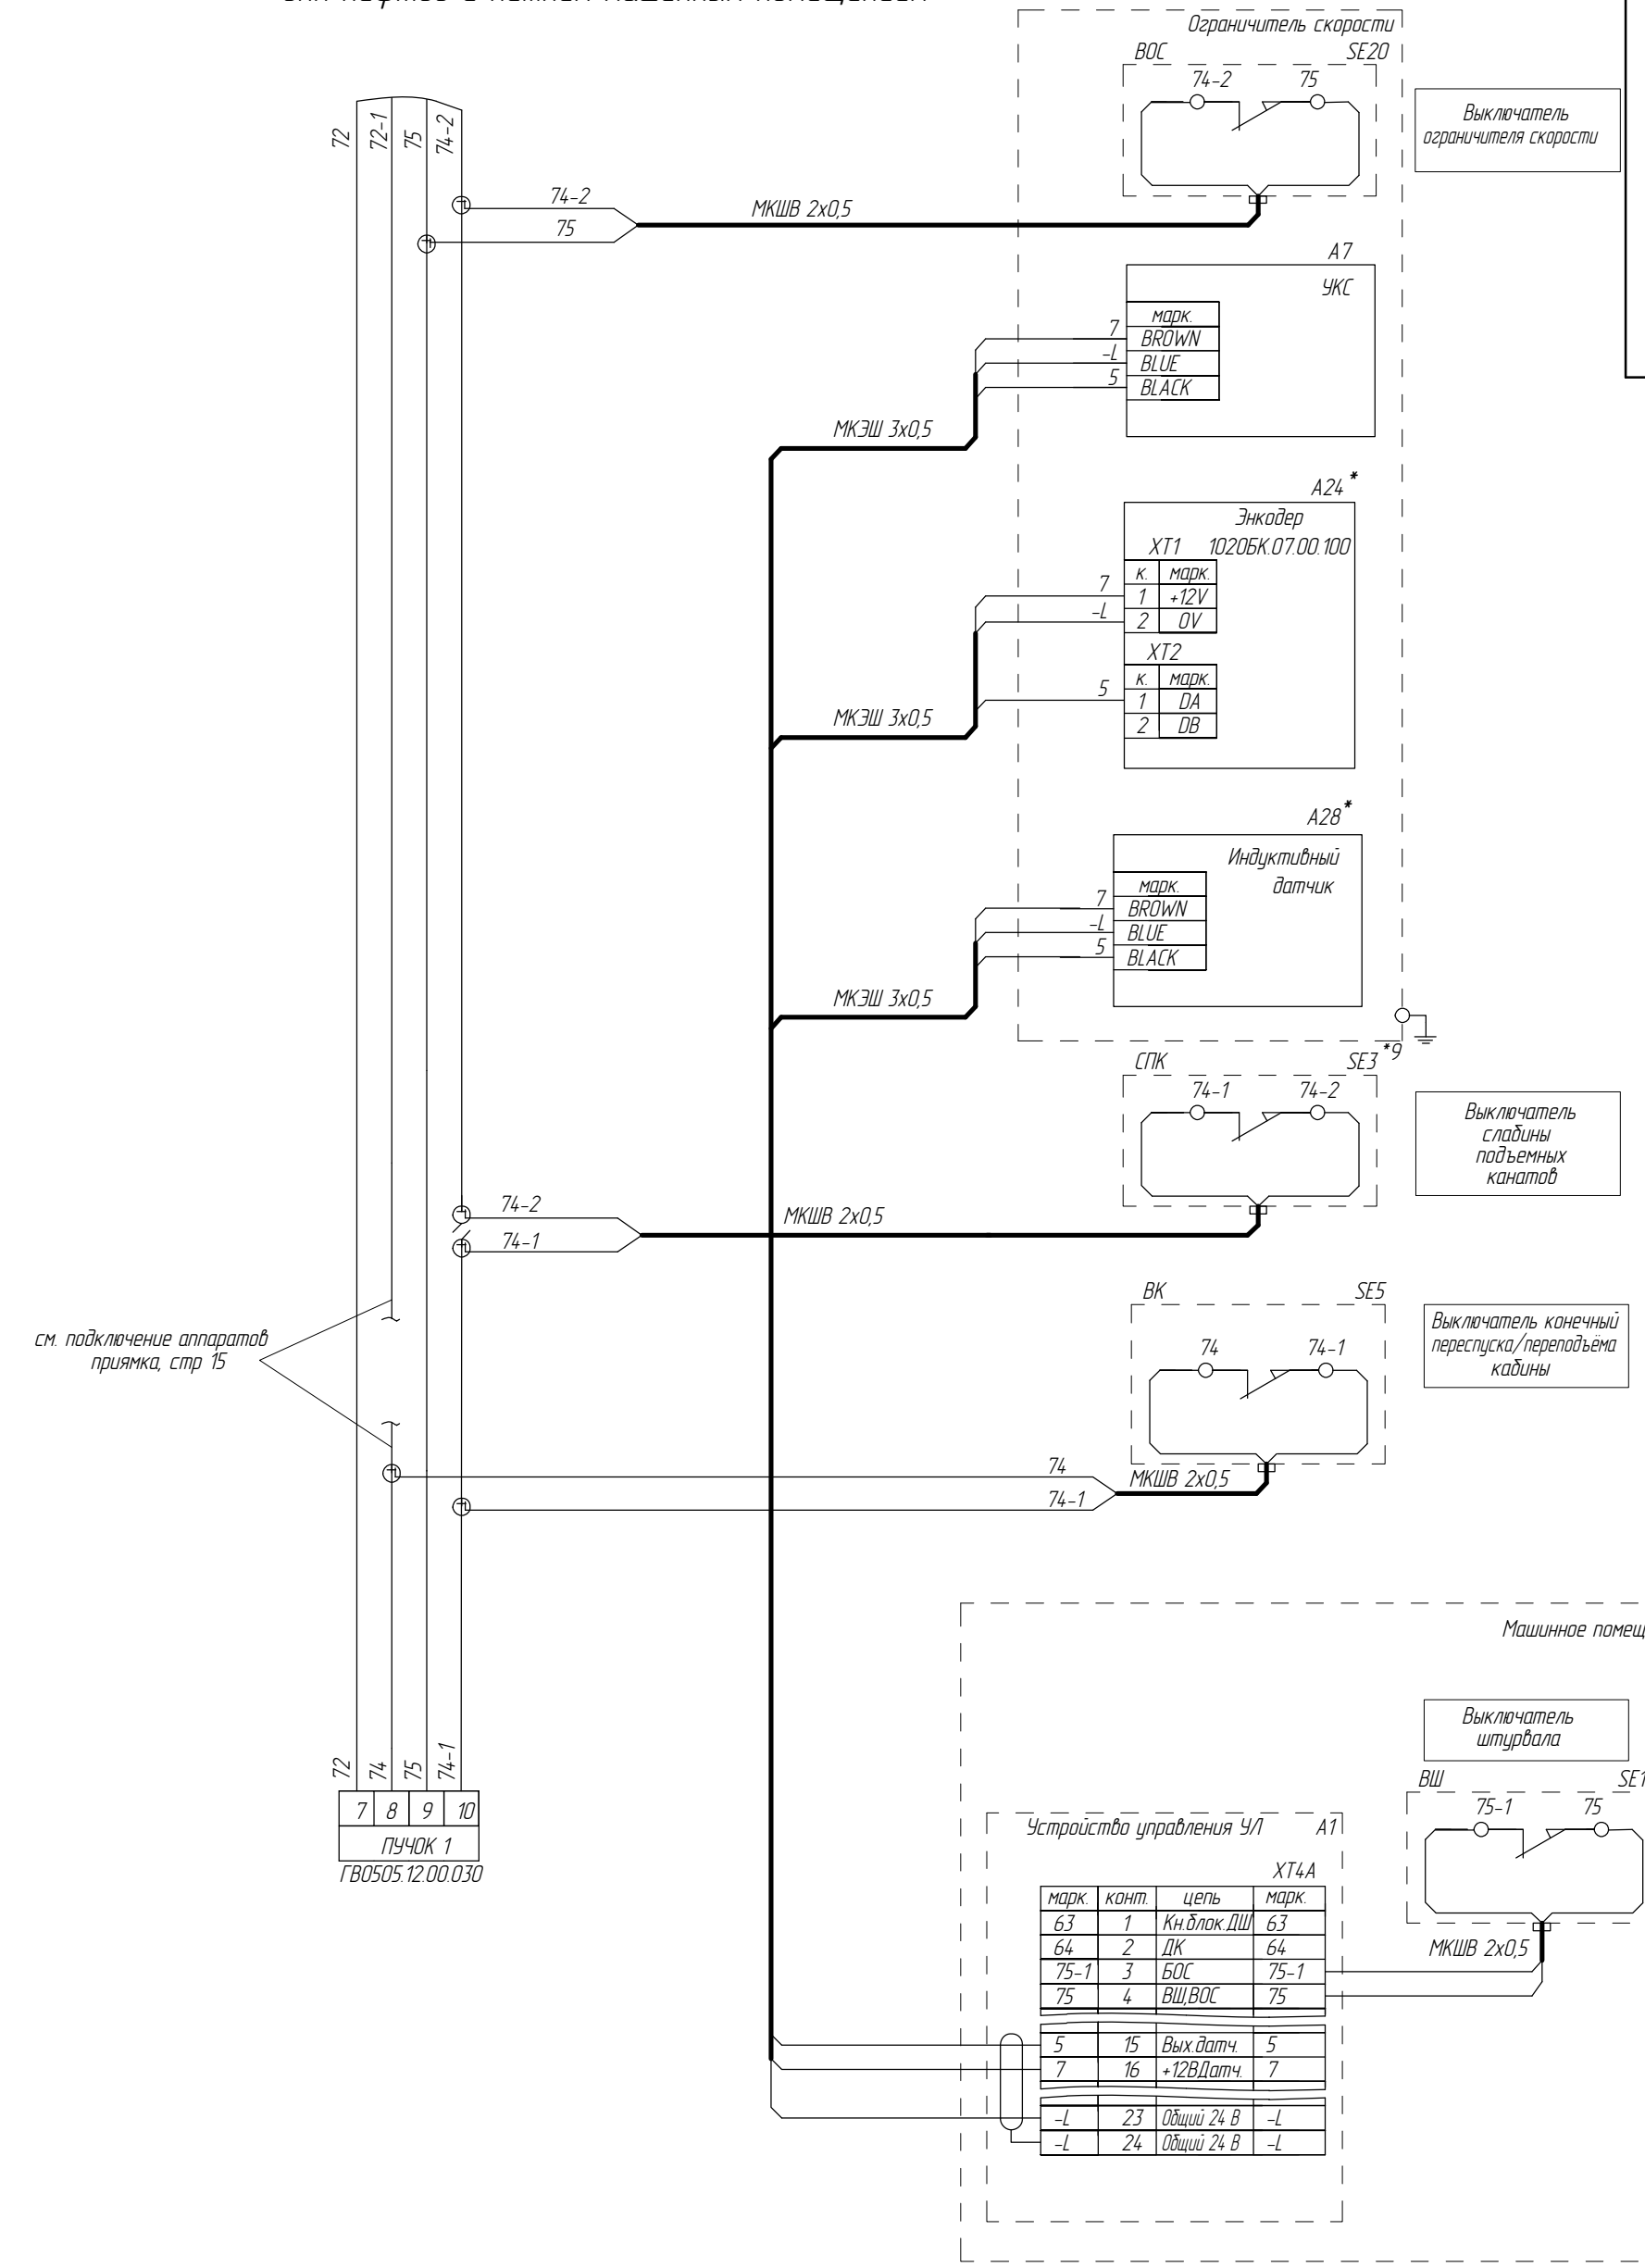


*9 – Выключатель SE3 (СПК) для лифтов с верхним МП устанавливается для Q = 500 кг на кабине, для Q > 500 кг – в машинном помещении (МП).

*МаВ – только для лифтов с малым верхним этажом

| Изм | Лист | № докум. | Подп. | Дата | ФАИД.484440.002 Э4 | Лист 7а |
|---|---|---|---|---|---|---|
| 7 | | 186.013823-2025 | | | | |

ФАИД.484440.002 Э4

Перв. примен.

Справ. №

Подп. и дата

Инв.№ дубл.

Взам. инв. №

Подп. и дата 19.12.2025

Инв.№ подл. 4031

Черенкова (Подп)

IPS ID: 110655800


Список цехов:расцеховок нет.

Копировал

Формат А3

# Ограничитель скорости 1020БК.17.ХХ.ХХХ, ВК, СПК, ВШ (лифт с верхним машинным помещением)



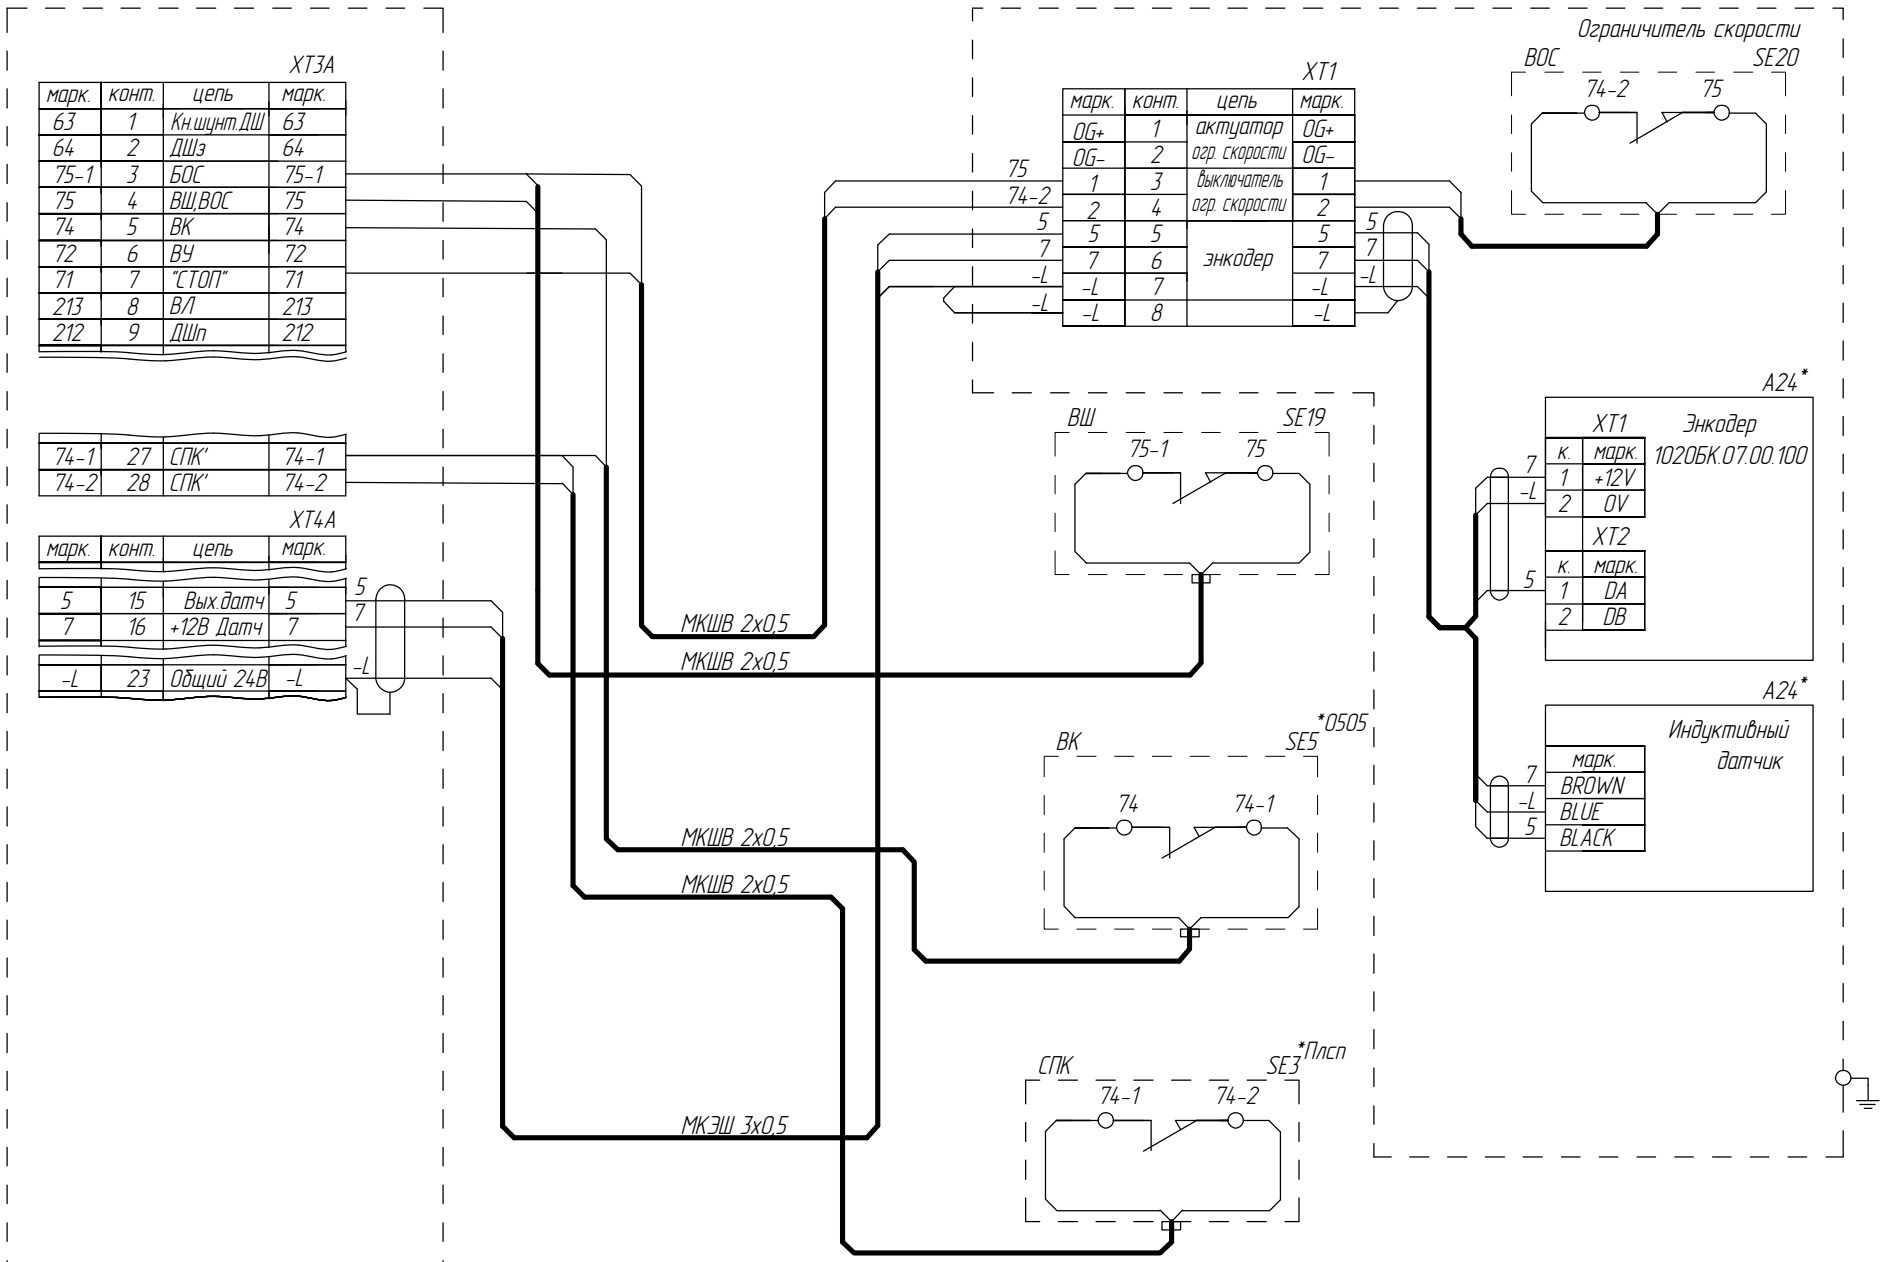


*0505 – кроме лифтов ГВ0505, для лифтов ГВ0505 ВК расположен в приямке
* – наличие зависит от исполнения аппаратов или устройств
*Плсп – для лифтов с полиспастом

| Изм | Лист | № докум. | Подп. | Дата | ФАИД.484440.002 Э4 | Лист 7б |
|---|---|---|---|---|---|---|
| 7 | | 186.013823-2025 | | | | |

Инв.№ подл. 4031 | Подп. и дата Черенкова (Подп) 19.12.2025 | Взам. инв. № | Инв.№ дубл. | Подп. и дата

Перв. примен.

Справ. №

IPS ID: 110655800

Список цехов: расцеховок нет.

Копировал

Формат А3

# Ограничитель скорости 1020БК.17.ХХ.ХХХ, ВШ, СПК
## (лифт с нижним машинным помещением)



Верхний этаж

72 72-1 75 70

74-2 МКШВ 2х0,5 75

74-2 МКШВ 2х0,5 74-1

МКЭШ 3х0,5

Ограничитель скорости
ВОС SE20
74-2 75

XT1

| марк. | конт. | цепь | марк. |
|---|---|---|---|
| ОБ+ | 1 | актуатор огр. скорости | ОБ+ |
| ОБ- | 2 | | ОБ- |
| 1 | 3 | выключатель огр. скорости | 1 |
| 2 | 4 | | 2 |
| 5 | 5 | энкодер | 5 |
| 7 | 6 | | 7 |
| -L | 7 | | -L |
| -L | 8 | | -L |

75 74-2 5 7 -L -L

5 7 -L

Выключатель СПК
74-1 SE3 74-2

A24*
XT1 Энкодер 1020БК.07.00.100

| к. | марк. |
|---|---|
| 1 | +12V |
| 2 | 0V |

7 -L

XT2

| к. | марк. |
|---|---|
| 1 | DA |
| 2 | DB |

5

A24*
Индуктивный датчик

| марк. |
|---|
| BROWN |
| BLUE |
| BLACK |

7 -L 5

72 74 75 74-1

| 9 | 10 | 11 | 12 |
|---|---|---|---|
| ПУЧОК 1 | | | |

ГВ0505.12.00.030

см. подключение аппаратов приямка, стр 15

Машинное помещение

Машинное помещение

Выключатель штурвала
ВШ SE19
75-1 75

МКШВ 2х0,5


Устройство управления УЛ A1

XT4A


| марк. | конт. | цепь | марк. |
|---|---|---|---|
| 63 | 1 | Кн.блок.ДШ | 63 |
| 64 | 2 | ДК | 64 |
| 75-1 | 3 | БОС | 75-1 |
| 75 | 4 | ВШ,ВОС | 75 |
| 5 | 15 | Вых.датч. | 5 |
| 7 | 16 | +12ВДатч. | 7 |
| -L | 23 | Общий 24 В | -L |
| -L | 24 | Общий 24 В | -L |

# Подключение выключателей упоров верхнего этажа с двумя выключателями

## Верхнее машинное помещение

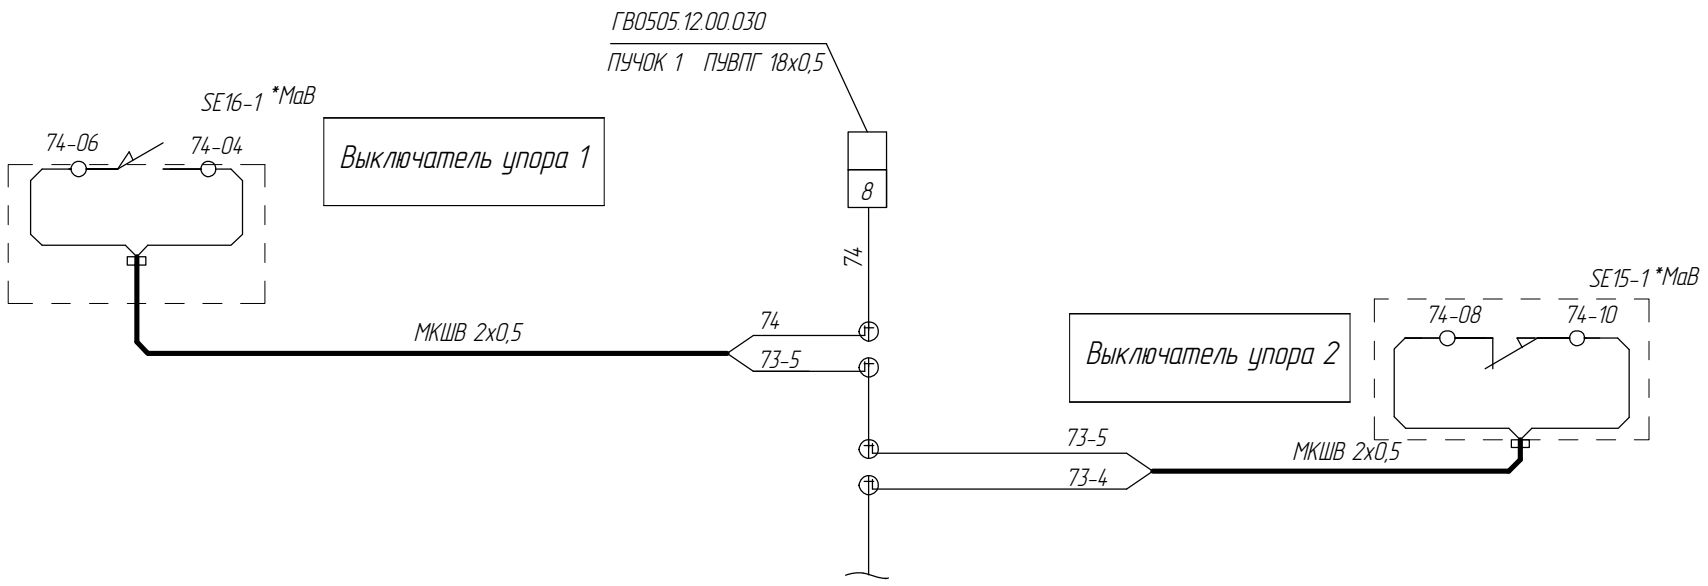


## Нижнее машинное помещение

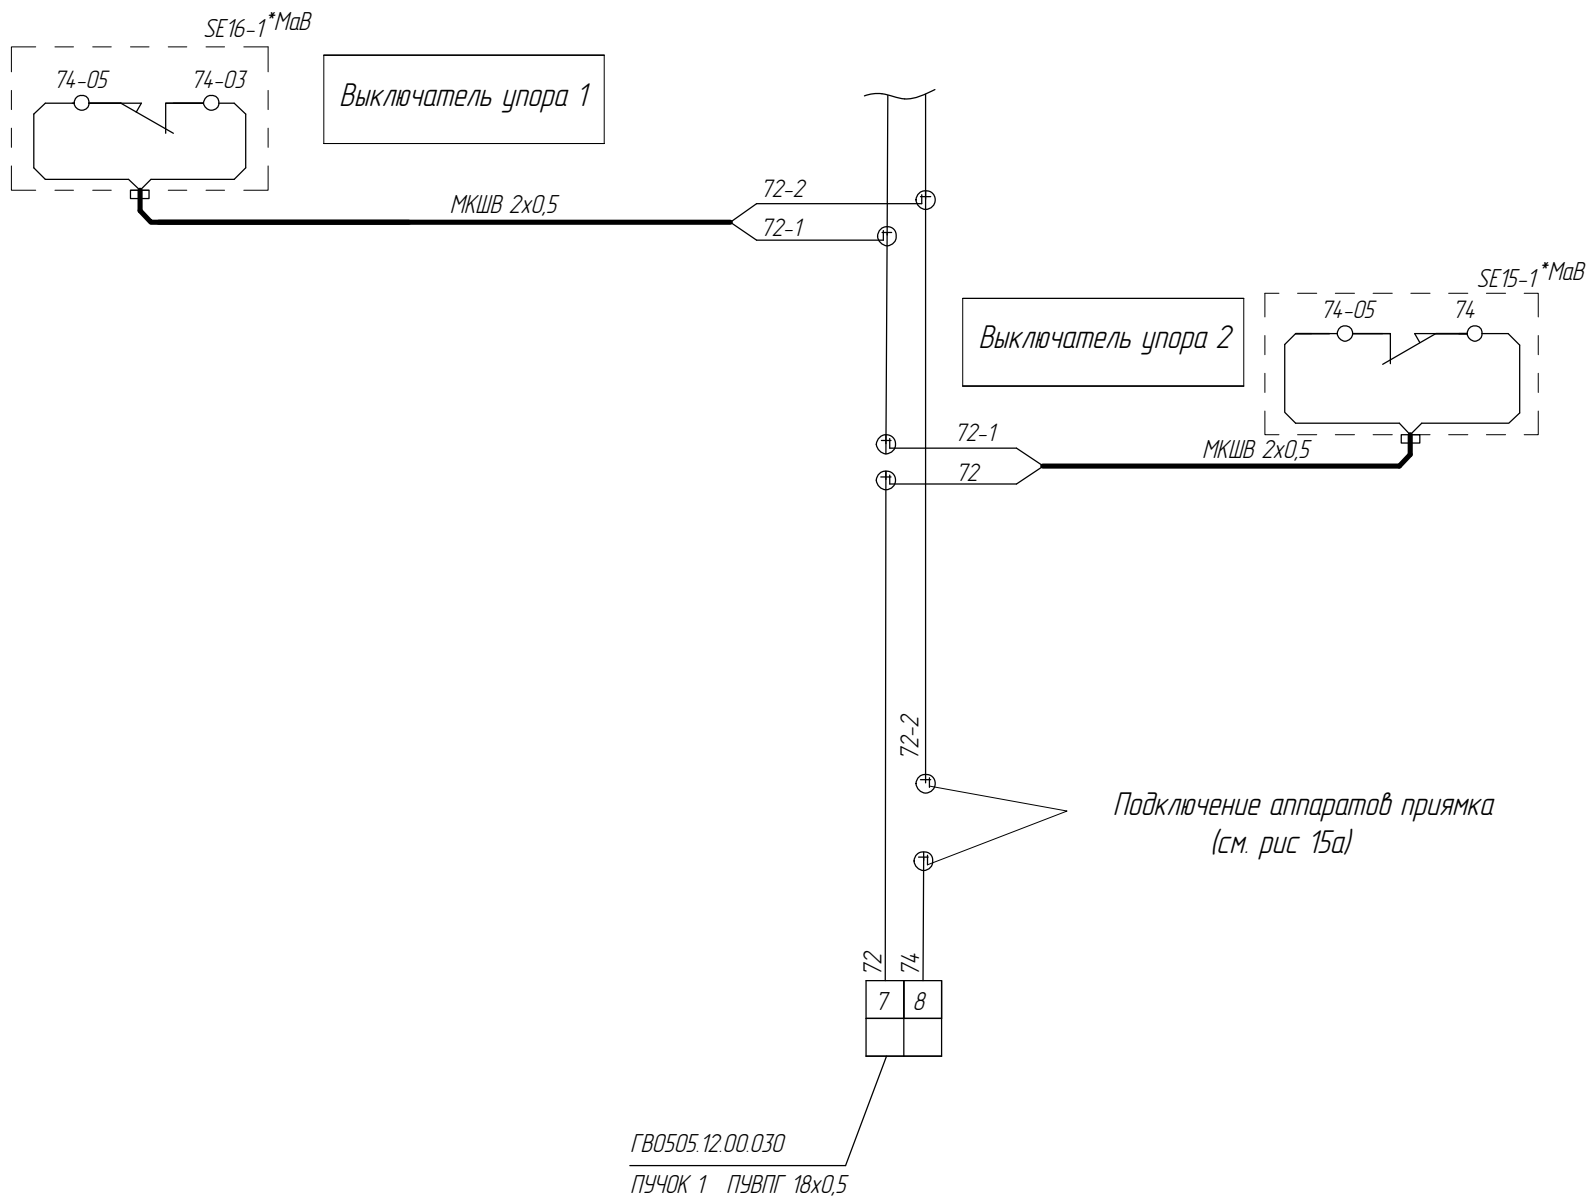


*MaB – только для лифтов с малым верхним этажом

| | | | | | |
|---|---|---|---|---|---|
| 7 | | 186.013823-2025 | | | ФАИД.484440.002 Э4 |
| Изм | Лист | № докум. | Подп. | Дата | |

Лист 8

ФАИД.484440.002 Э4


Инв.№ подл. 4031 | Подп. и дата Черенкова (Подп) 19.12.2025 | Взам. инв. № | Инв.№ дубл. | Подп. и дата | Справ. № | Перв. примен.

IPS ID: 110655800

Список цехов:расцеховок нет.

Копировал Формат А3

# Подключение кнопок вызова

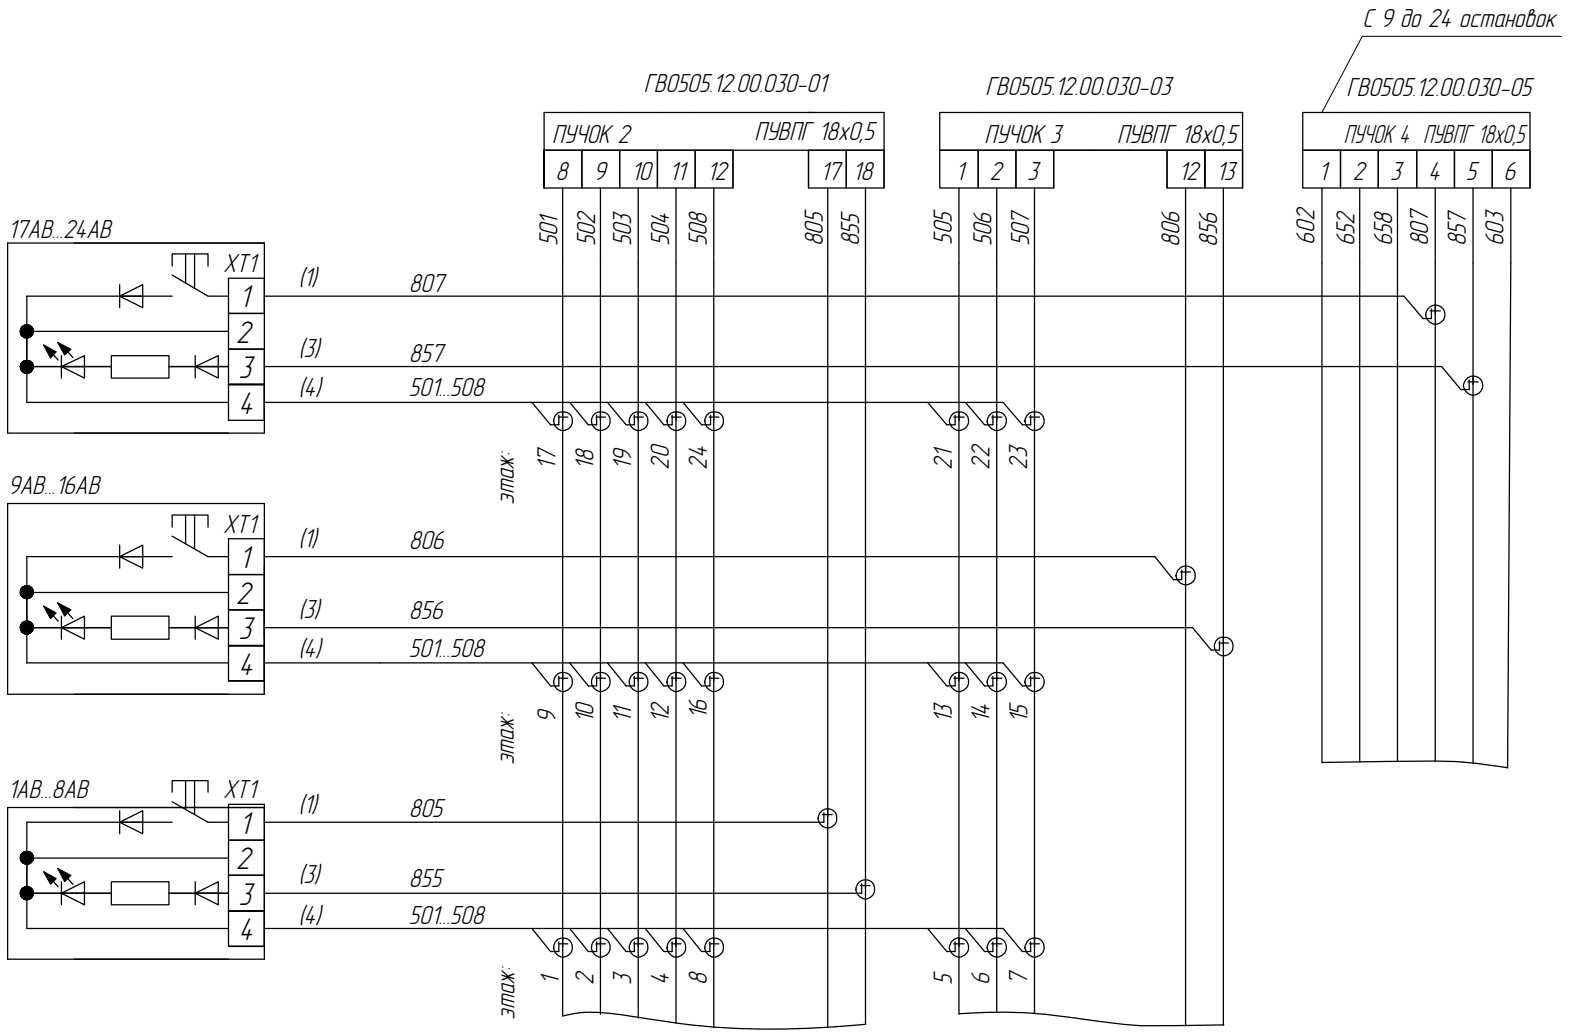


Кабели подключения постов вызывных – в комплекте

| | | | | | | |
|---|---|---|---|---|---|---|
| 7 | | 186.013823-2025 | | | ФАИД.484440.002 ЭЗ | Лист 9 |
| Изм | Лист | № докум. | Подп. | Дата | | |

Инв.№ подл. 4031 | Подп. и дата Черенкова (Подп) 19.12.2025 | Взам. инв. № | Инв.№ дубл. | Подп. и дата

Справ. №

Перв. примен.

IPS ID: 110655800

Список цехов: расцеховок нет.

Копировал

Формат А3

| Инв.№ подл. | Подп. и дата | Взам. инв. № | Инв.№ дубл. | Подп. и дата |
|---|---|---|---|---|
| 4031 | Черенкова (Подп) 19.12.2025 | | | |

| Справ. № | Перв. примен. |
|---|---|
| | |

IPS ID: 110655800

# Индикация на этажах (устанавливается по спецзаказу)

(P)AH1,(n)AH1 — Табло ТИ

XT1: G 507, F 506
XT2: A 501, B 502
XT3: C 503, D 504, E 505
XT4: СТВ 655, СТН 656, СТ 508

(P)AH1,(n)AH1 — Табло ТИМ2

XP1: 606, 656, 655, 501, -L, 3

(P)AH1,(n)AH1 — Табло MLM LCD

XP2: 3, -L, 501, 606, 655, 656

(P)AH1,(n)AH1 — Табло MLM LCD (Посл. канал)

XP2: 3, -L, 655

(P)AH1,(n)AH1 — Табло Зенит 7

XP1: 3, -L, 655
XP2
LCD Color 800x480

ГВ05Г5 12.00.030 ПУЧОК 1 ПУВПТ 18х0,5

| | | |
|---|---|---|
| A | 501 | 8 |
| B | 502 | 9 |
| C | 503 | 10 |
| D | 504 | 11 |
| СТ | 508 | 12 |
| | 605 | 13 |
| | 606 | 14 |
| | 608 | 15 |
| | 805 | 17 |
| | 855 | 18 |
| | 3 | 13 |
| | -L | 14 |

ГВ05Г5 12.00.030-01 ПУЧОК 2 ПУВПТ 18х0,5

| | | |
|---|---|---|
| E | 505 | 1 |
| F | 506 | 2 |
| G | 507 | 3 |
| СТВ | 655 | 8 |
| СТН | 656 | 9 |

ГВ05Г5 12.00.030-03 ПУЧОК 3 ПУВПТ 18х0,5

Кабели подключения табло индикации - в комплекте

| Изм. | Лист | № докум. | Подп. | Дата |
|---|---|---|---|---|
| 7 | | 186.01382З-2025 | | |

Спискок цехов расцеховок нет.


ФАИД.484440.002 Э4

Лист 10

Копировал

Формат А3

ФАИД.484440.002 Э4

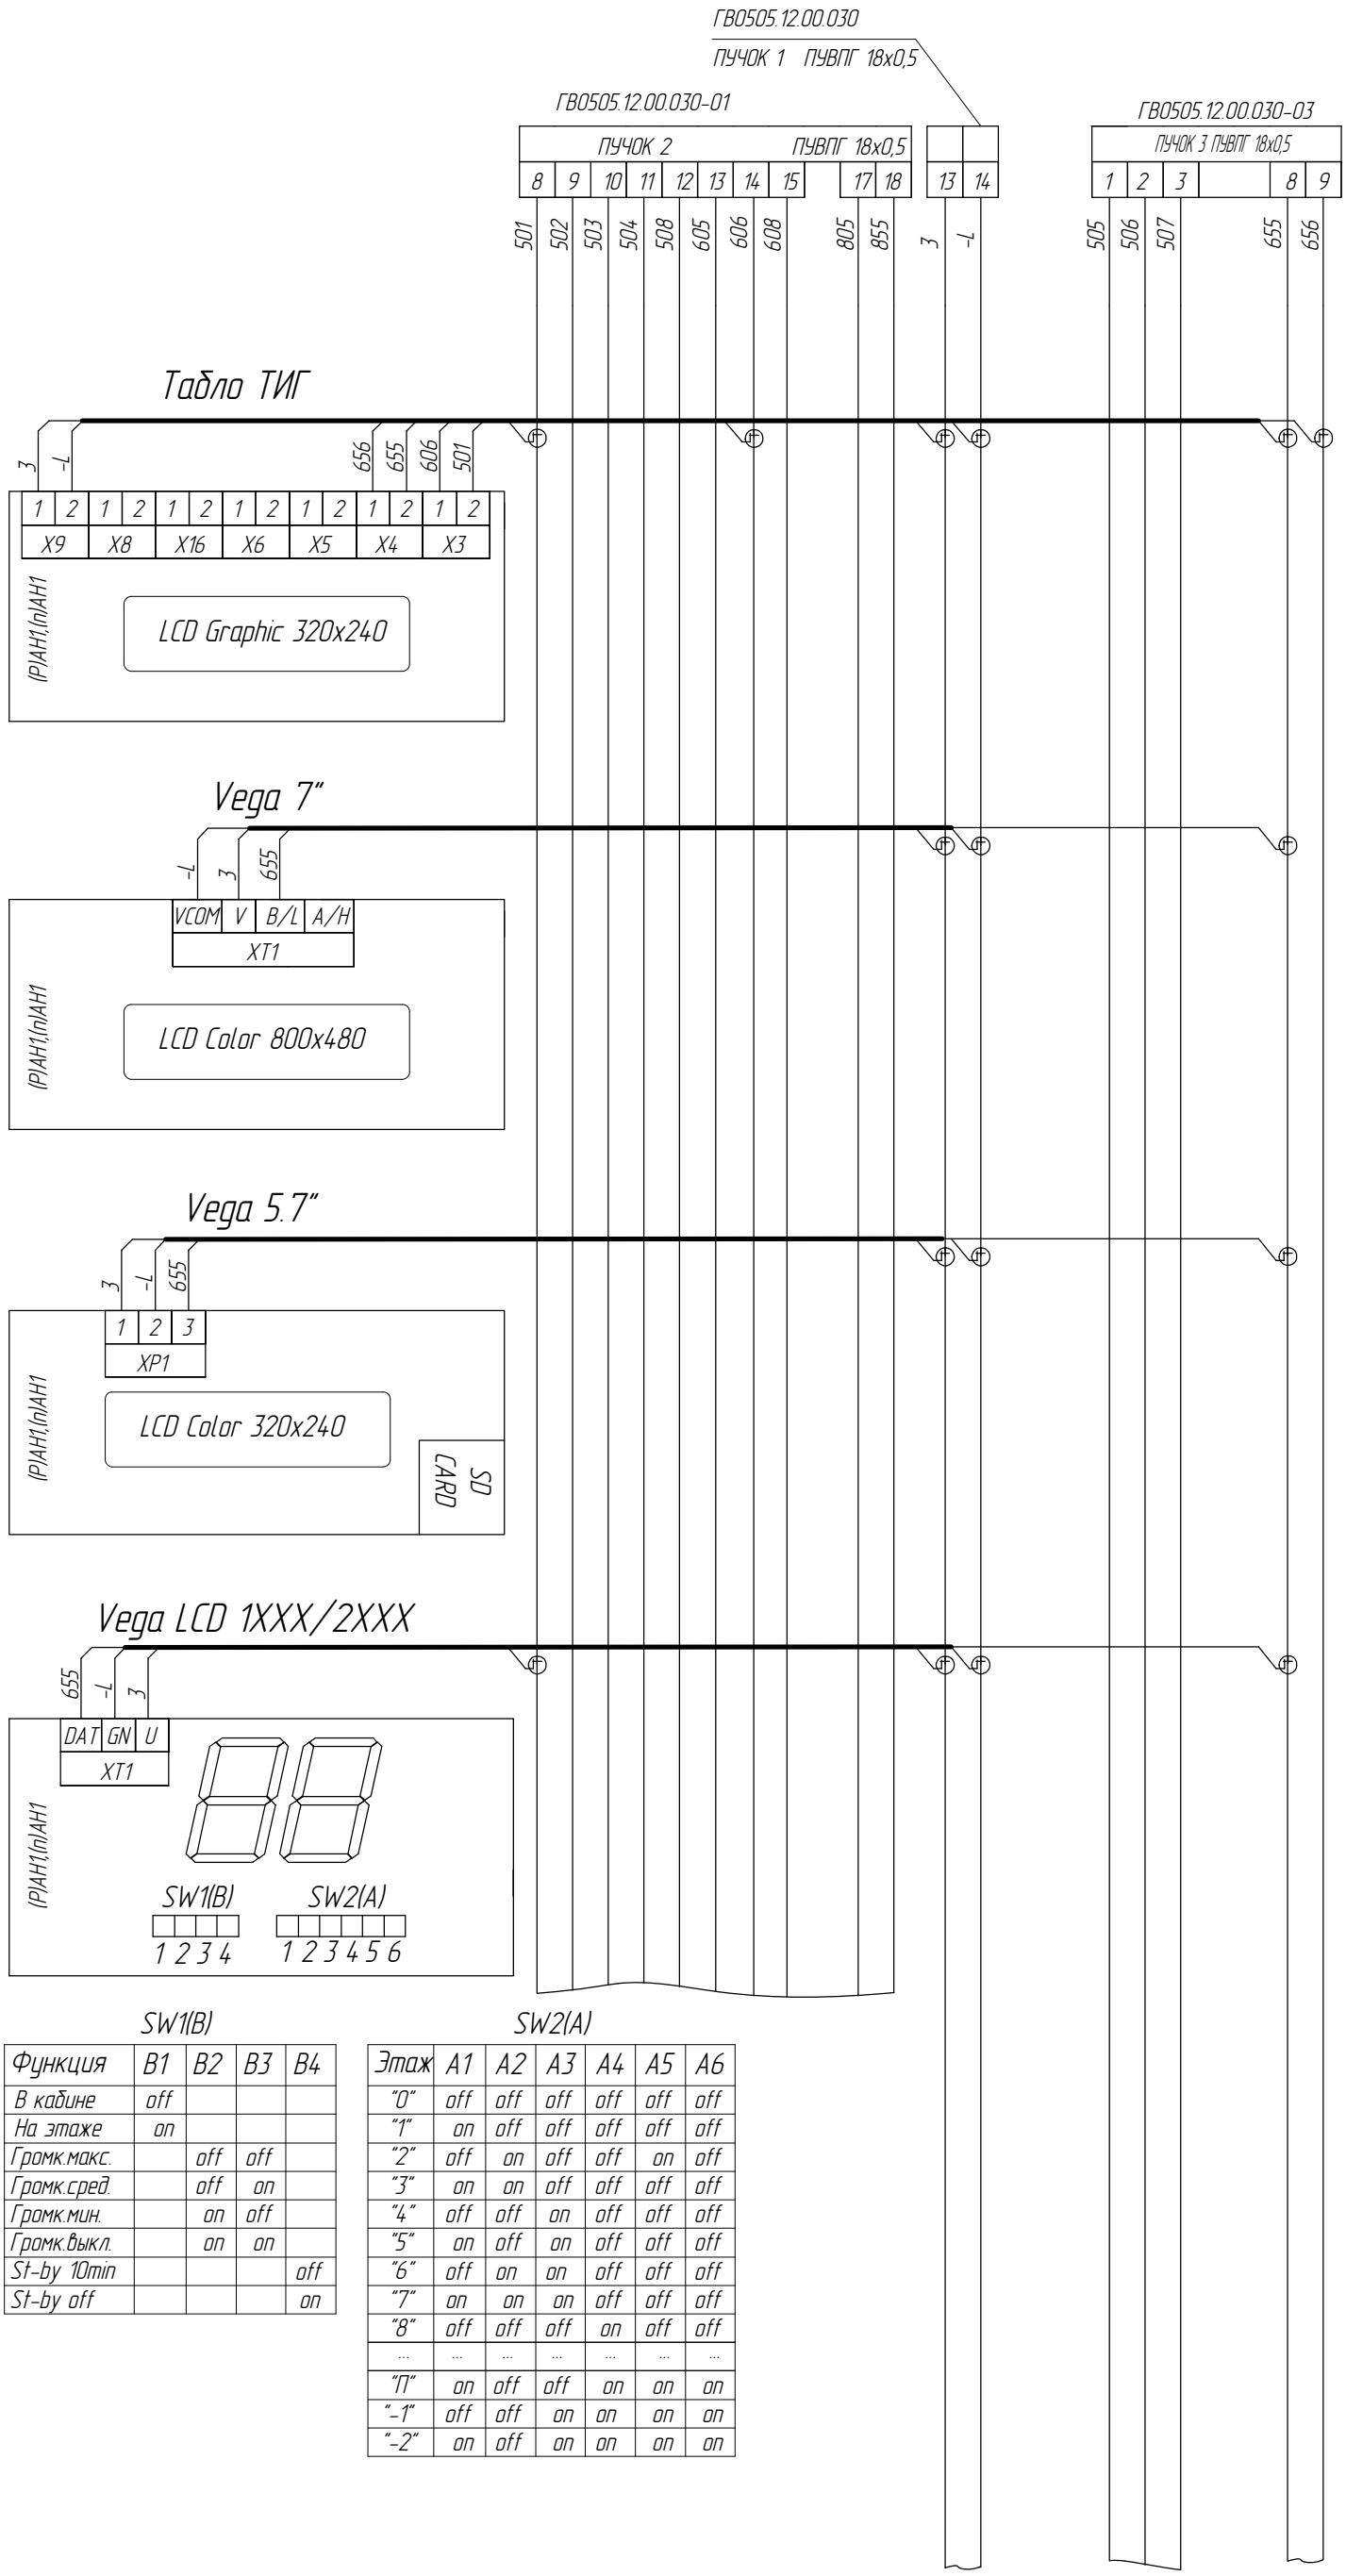


SW1(B)

| Функция | B1 | B2 | B3 | B4 |
|---|---|---|---|---|
| В кабине | off | | | |
| На этаже | on | | | |
| Громк.макс. | | off | off | |
| Громк.сред. | | off | on | |
| Громк.мин. | | on | off | |
| Громк.выкл. | | on | on | |
| St-by 10min | | | | off |
| St-by off | | | | on |

SW2(A)

| Этаж | A1 | A2 | A3 | A4 | A5 | A6 |
|---|---|---|---|---|---|---|
| "0" | off | off | off | off | off | off |
| "1" | on | off | off | off | off | off |
| "2" | off | on | off | off | on | off |
| "3" | on | on | off | off | off | off |
| "4" | off | off | on | off | off | off |
| "5" | on | off | on | off | off | off |
| "6" | off | on | on | off | off | off |
| "7" | on | on | on | off | off | off |
| "8" | off | off | off | on | off | off |
| ... | ... | ... | ... | ... | ... | ... |
| "П" | on | off | off | on | on | on |
| "-1" | off | off | on | on | on | on |
| "-2" | on | off | on | on | on | on |

Кабели подключения табло индикации – в комплекте

| Изм | Лист | № докум. | Подп. | Дата | ФАИД.484440.002 Э4 | Лист 10а |
|---|---|---|---|---|---|---|
| 7 | | 186.013823-2025 | | | | |

ФАИД.484440.002 Э4

Перв. примен.

Справ. №

Подп. и дата

Инв.№ дубл.

Взам. инв. №

Подп. и дата 19.12.2025 Черенкова (Подп)

Инв.№ подл. 4031


IPS ID: 110655800

Список цехов-расцеховок нет.

Копировал

Формат А3

# Вариатны постов с ограничением доступа на этаже (iButton)
(устанавливается по спецзаказу)

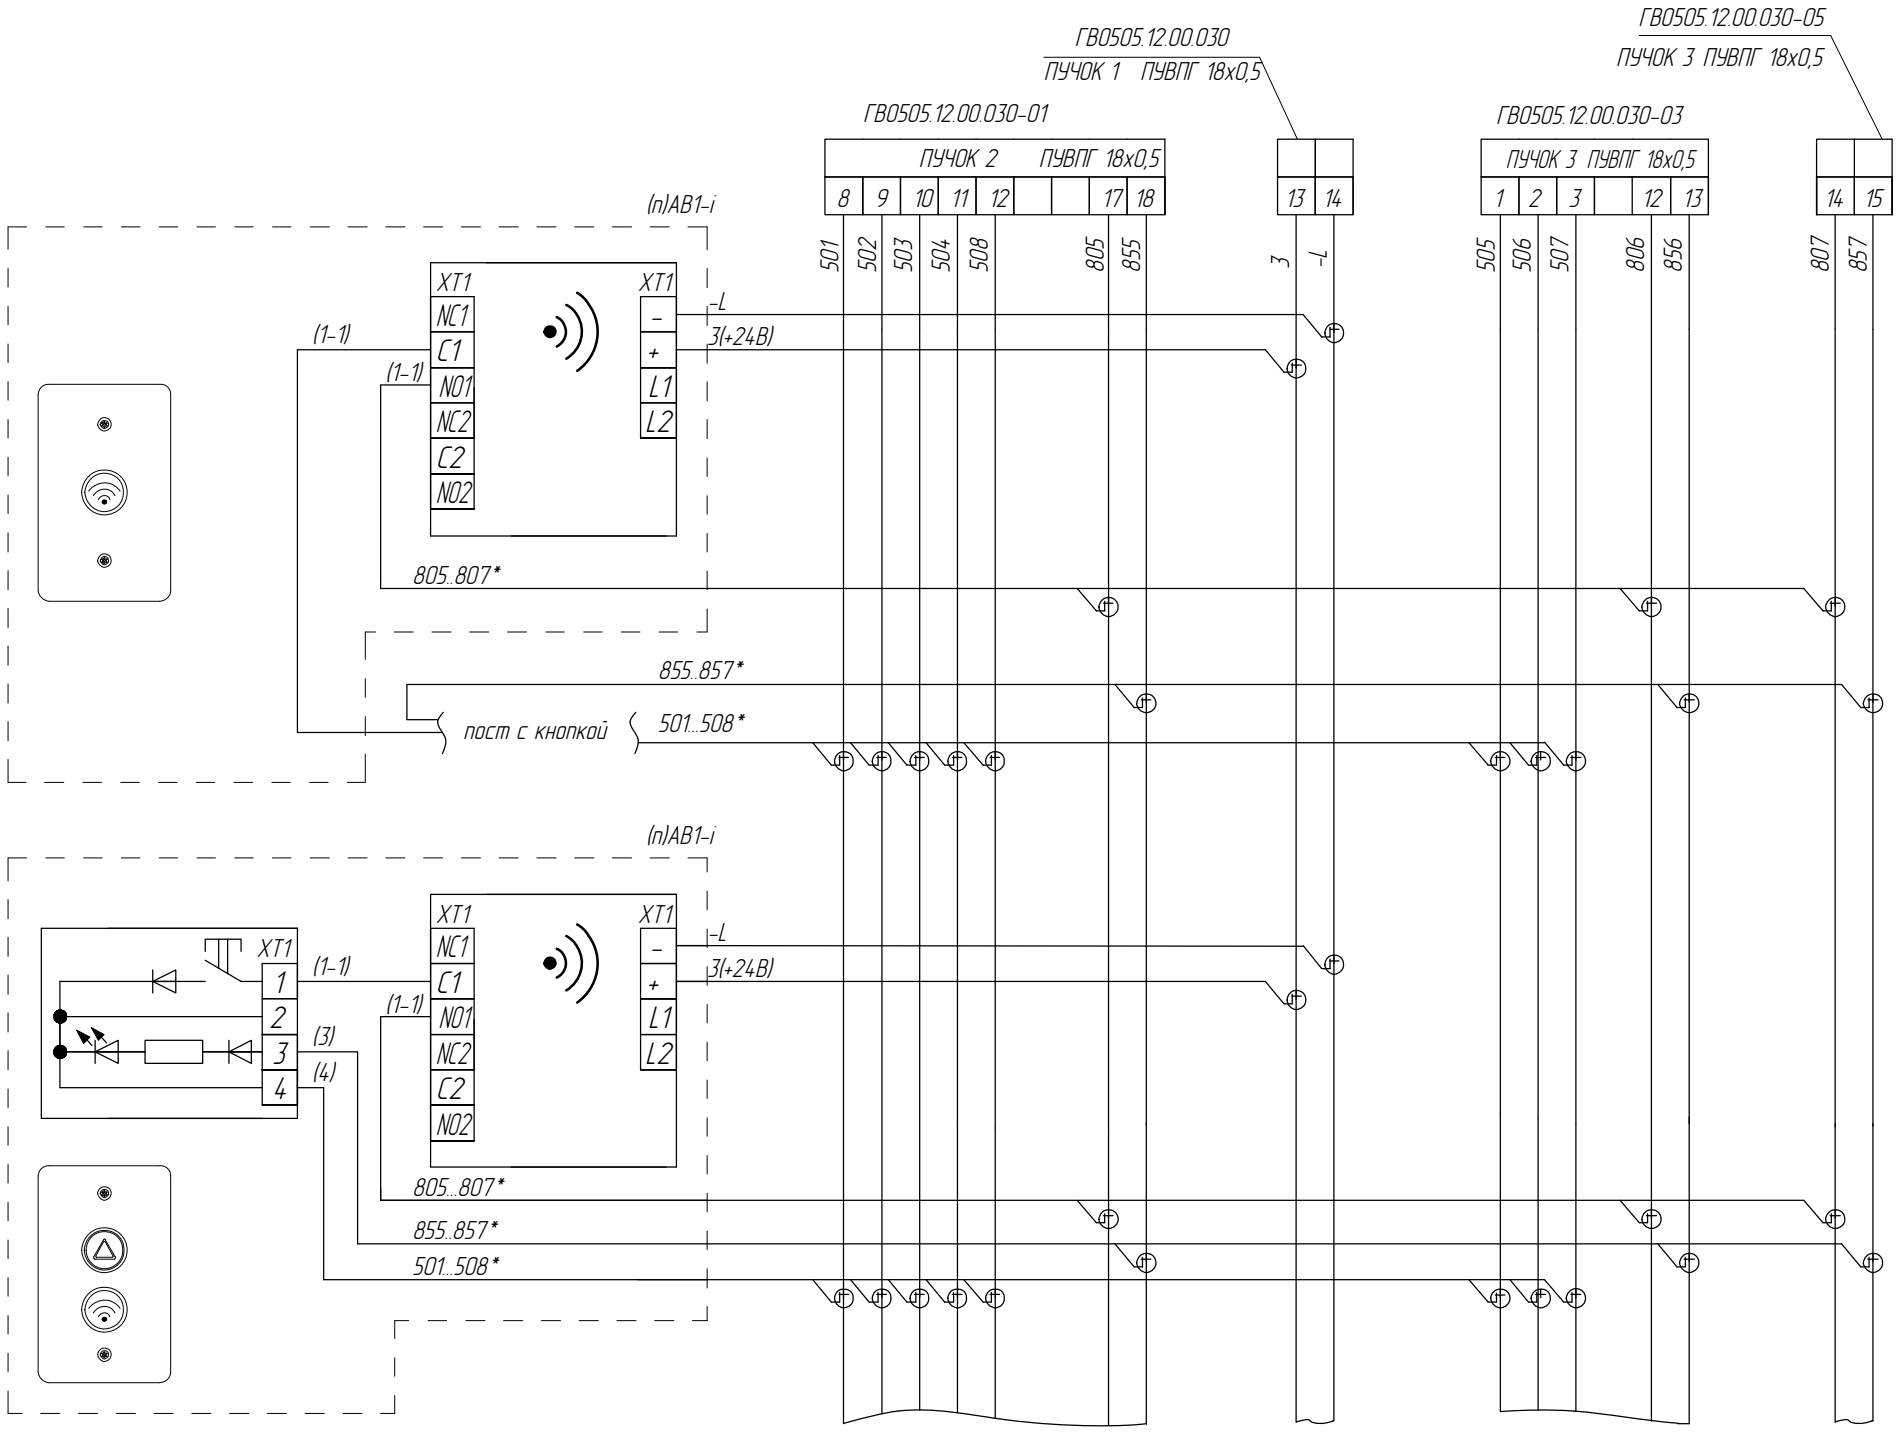


Кабели постов – в комплекте

ФАИД.484440.002 Э4

| Изм | Лист | № докум. | Подп. | Дата |
|---|---|---|---|---|
| 7 | | 186.013823-2025 | | |

Лист 11

Инв.№ подл. 4031 | Подп. и дата Черенкова (Подп) 19.12.2025 | Взам. инв. № | Инв.№ дубл. | Подп. и дата

Перв. примен.

Справ. №

Список цехов: расцеховок нет.


Копировал

Формат А3

IPS ID: 110655800

# Подключение поста приказов на этажах

ФАИД.484440.002 Э4

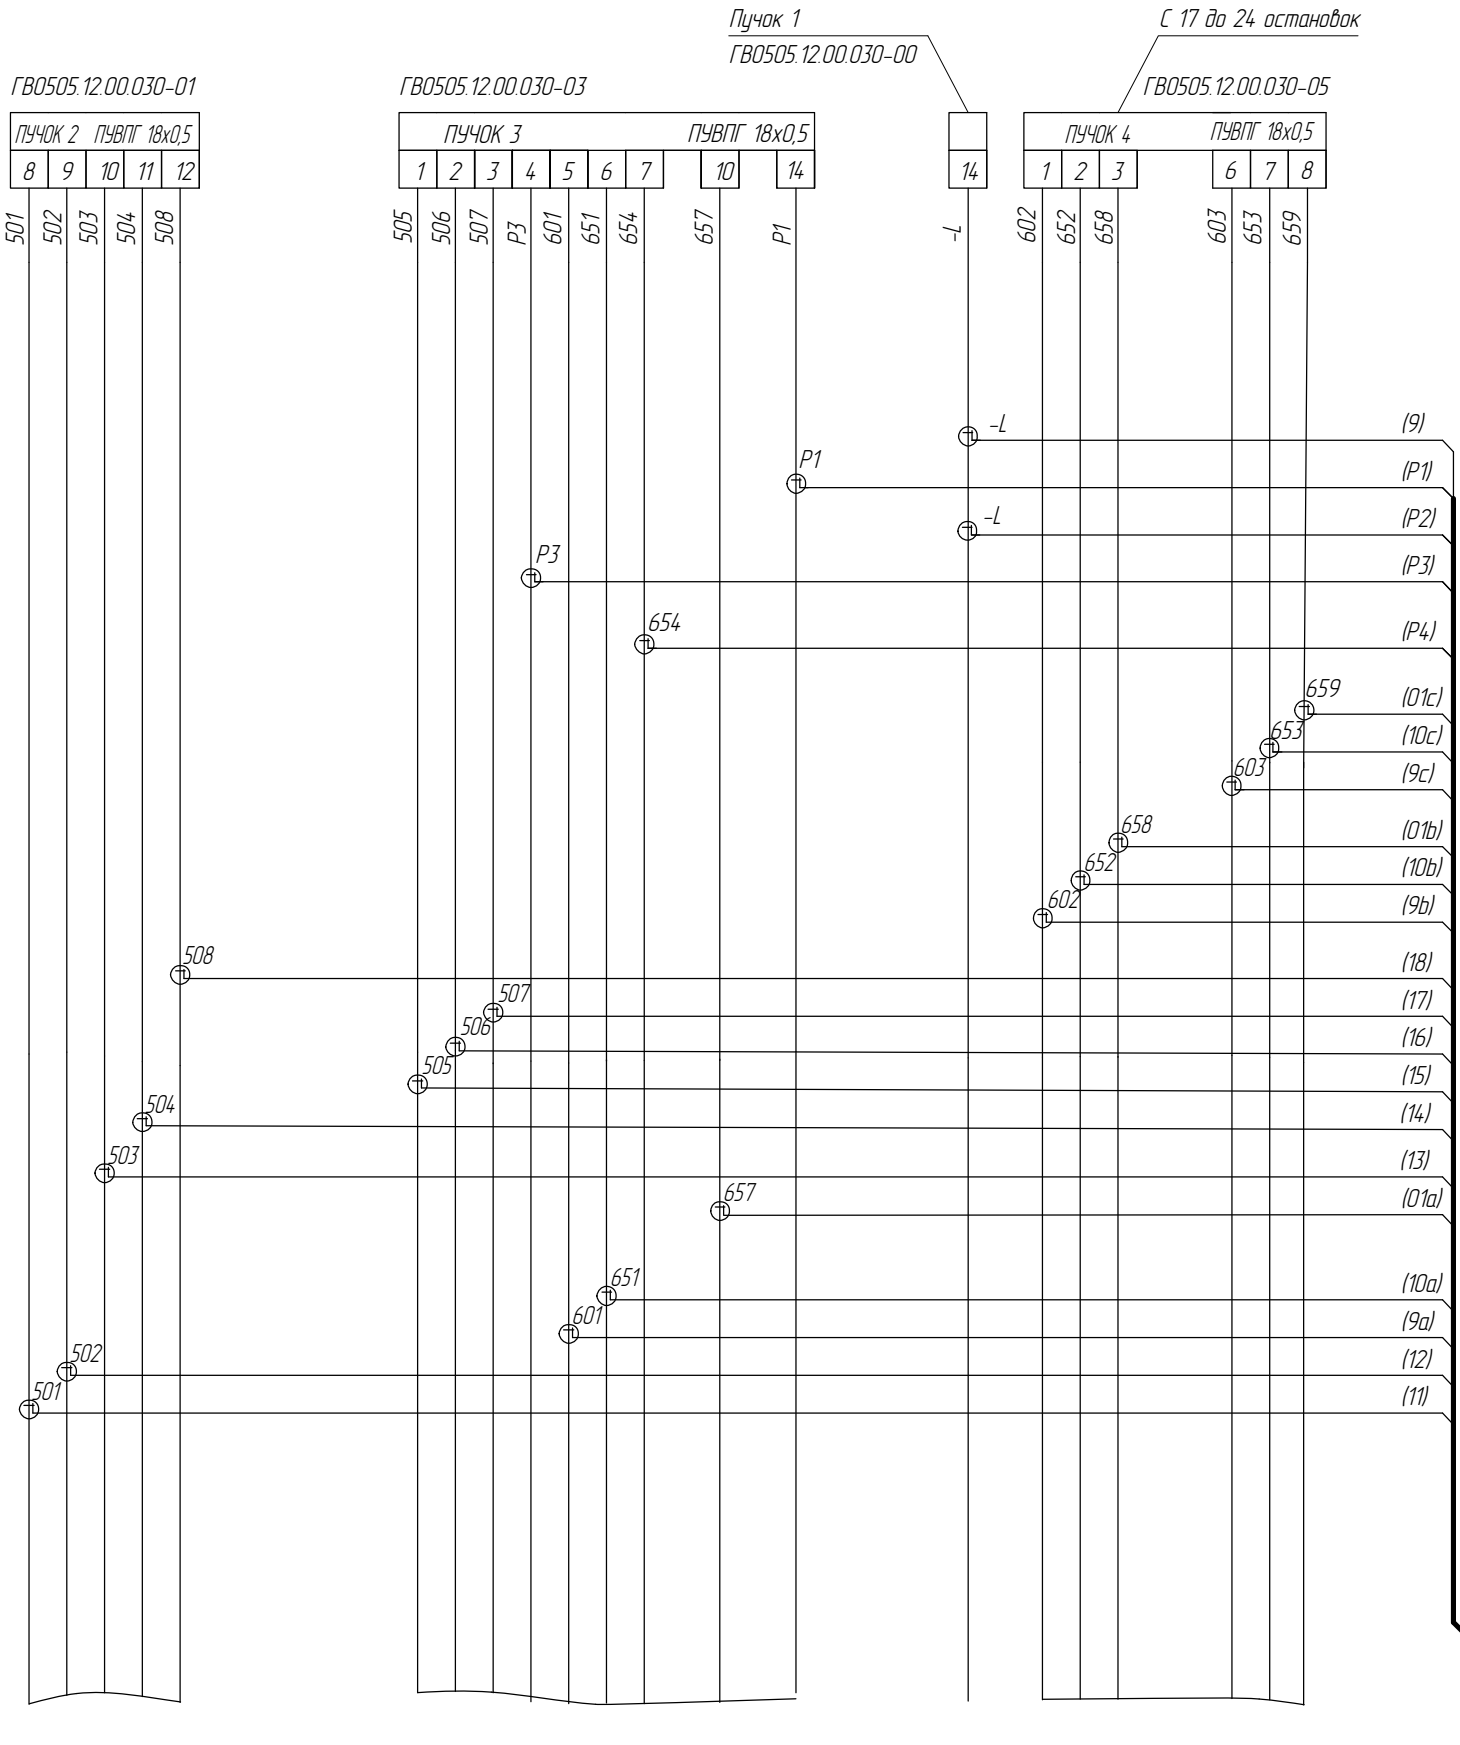


| Инв.№ подл. | Подп. и дата | Взам. инв. № | Инв.№ дубл. | Подп. и дата | Перв. примен. |
|---|---|---|---|---|---|
| 4031 | Черенкова (Подп) 19.12.2025 | | | | Справ. № |

| Изм | Лист | № докум. | Подп. | Дата | 186.013823-2025 | ФАИД.484440.002 Э4 | Лист 12 |
|---|---|---|---|---|---|---|---|
| 7 | | | | | | | |

# Подключение датчиков положения и пожарной сигнализации

ГВ0505.12.00.030-03
ПУЧОК 3 ПУВПГ 18х0,5

ГВ0505.12.00.030-00

ГВ0505.12.00.030-01

## Датчики положения (вариант размещения: в шахте)

магнитные датчики

датчики ВПЛ

SQ5(ДВЭ)
бистабильный
бел.
кр.
508
606
(-)
(+)

SQ6(ДПЭ)
моностабильный
506
608

SQ4(ДНЭ)
бистабильный
508
608

ПУЧОК 1: 12, 13
ПУЧОК 2: 7, 12, 14, 15
2

163
3
022
508
606
608
506

(-) белый
(+) красный

## Контакт системы пожарной сигнализации здания (не входит в комплект лифта)

163
3

Основная погрузочная остановка

Пост ПО (кулачковый)
AP2*
XT1
1 (1) 163
2 (2) 3

Пост ПО (Vega)
AP2*
XT1
NC (1) 163
C (2) 3

Пост дистанционного отключения
Дист. откл.
SA5
022
3
АП1
XT1
3 1
022 2
3
4
5

Кабели – в комплекте
* – наличие зависит от исполнения

ФАИД.484440.002 Э4

| Изм | Лист | № докум. | Подп. | Дата | 186.013823-2025 | ФАИД.484440.002 Э4 | Лист 13 |
|---|---|---|---|---|---|---|---|

Инв.№ подл. 4031 | Подп. и дата | Черенкова (Подп) 19.12.2025 | Взам. инв. № | Инв.№ дубл. | Подп. и дата | Справ. № | Перв. примен.

IPS ID: 110655800

Список цехов: расцеховок нет.

Копировал

Формат А3

# Цепь безопасности дверей шахты

## Верхний этаж

ГВ0505.12.00.030-01

ПУЧОК 2 ПУВПГ 18х0,5

1 | 2 | 3 | 4 | 5 | 6

(В-1)-7 (В-1)-8 64 70 224 110

Двери шахты 2 *ПК

(В)SM1-2 Притвор

70 (1) (2) (В)-6 → В-6

70

(В)SM3 Охрана шахты

110 (11) *М (12) (В)-4

R

(33) (34)

(В)SM2-2 Замок

64 (2) (1) (В)-5 → (В)-5

64

110

ПУВВПГ 4х0,5

ПУВВПГ 4х0,5 *ПК

(В-1)-7

(В-1)-8

110

224

Двери шахты 1

(В)SM1-1 Притвор

(В)-6 *ПК (1) (2) (В-1)-8 → (В-1)-8

70

(В)-6 → 70

(В)SM3-А Охрана шахты

110 (11) *М (12) (В)-4

R

224 (33) (34)

(В)SM2-1 Замок

(В)-5 *ПК (2) (1) (В-1)-7 → (В-1)-7

64

ПУВВПГ 4х0,5

(В)-5 → 64

(В)-4

Подключение дверей шахты для непроходной кабины

## Промежуточный этаж

Двери шахты 2 *ПК

(В)SM1-2 Притвор

(п-8) (1) (2) (п)-6 → (п)-6

(п)-8

(В)SM3-А Охрана шахты

110 (11) *М (12) (п)-4

R

(33) (34)

(В)SM2-2 Замок

(п)-7 (2) (1) (п)-5 → (п)-5

(п)-7

ПУВВПГ 4х0,5 *ПК

(п-7)

(п)-8

110

ПУВВПГ 4х0,5

Подключение дверей шахты для непроходной кабины

(п-1)-7

(п-1)-8

110

224

110

Двери шахты 1

(В)SM1-1 Притвор

(п)-6 *ПК (1) (2) (п-1)-8 → (п-1)-8

(п)-8

(п)-6 → (п)-8

(В)SM3 Охрана шахты

110 (11) *М (12) (п)-4

R

224 (33) (34)

(В)SM2-1 Замок

(п)-5 *ПК (2) (1) (п-1)-7 → (п-1)-7

(п)-7

ПУВВПГ 4х0,5

(п)-5 → (п)-7

(п)-4 224

(п-1)-7 (п-1-8 64 212 224 110

Продолжение см. лист 26

Кабели – в комплекте

*ПК – проходная кабина;

*М – контакт показан под воздействием механического усилия.

| Изм | Лист | № докум. | Подп. | Дата | 186.013823-2025 |
|---|---|---|---|---|---|

ФАИД.484440.002 Э4

Лист 14

Перв. примен.

Справ. №

Подп. и дата

Инв.№ дубл.

Взам. инв. №

Подп. и дата (Подп) Черенкова 19.12.2025

Инв.№ подл. 4031

IPS ID: 110655800

Список цехов-расцеховок нет.

Копировал

Формат А3

ФАИД.484440.002 Э4

# Цепь безопасности дверей шахты

## Подключение аварийной двери шахты (при наличии)

ФАИД.484440.002 Э4

ГВ0505.12.00.030-01

ГВ0505.12.00.030-00

ПУЧОК 2 ПУВПГ 18х0,5

1 2 3 4 5 6

11 17 18

E-7 E-8 64 70 224 110

212 01-7 01-8

(n)SME1 ДШ

E-8 (1) (2) (n)-8

E-8

(n)SME3 Охрана шахты

110 (11) *M (12)

R

224 (33) (34)

ДШ (n)SME2

E-7 (2) (1) (n)-7

E-7

E-7

E-8

(n)-7

(n)-8

110

224

ПУВВПГ 4х0,5

## Первый этаж

Двери шахты 2 *ПК

1SM1-2 Притвор

01-8 (1) (2) 01-6

01-8

1SM3-A Охрана шахты

110 (11) *M (12) 01-4

R

(33) (34)

1SM2-2 Замок

01-7 (2) (1) 01-5

1-7

01-6

01-5

110 01-4

1-7

1-8

110

ПУВВПГ 4х0,5

Подключение дверей шахты для непроходной кабины

ПУВВПГ 4х0,5 *ПК

212

212

110

224

Двери шахты 1

1SM1-1 Притвор

01-6 *ПК (1) (2) 212

01-8

212

01-6 *ПК

01-8

1SM3 Охрана шахты

110 (11) *M (12) 01-4

R

224 (33) (34)

1SM2-1 Замок

01-5 *ПК (2) (1) 212

01-7

212

01-5 *ПК

01-7

ПУВВПГ 4х0,5

Кабели – в комплекте

*ПК – проходная кабина;

*М – контакт показан под воздействием механического усилия.

| | | | | | |
|---|---|---|---|---|---|
| 7 | | 186.013823-2025 | | | ФАИД.484440.002 Э4 |
| Изм | Лист | № докум. | Подп. | Дата | |

Лист 14а

Копировал Формат А3

Список цехов-расцеховок нет.

Перв. примен.

Справ. №

Подп. и дата

Инв.№ дубл.

Взам. инв. №

Подп. и дата (Подп) Черенкова 19.12.2025

Инв.№ подл. 4031

IPS ID: 110655800

# Устройства безопасности приямка
## Верхнее машинное помещение

ГВ0505.12.00.030-00

ПУЧОК 1 ГВ0505.12.00.030-00

1 | 3 | 4 | 5 | 7 | 8 | 13 | 14 | 16

L313 | L314 | L315 | N3 | 72 | 74 | 3 | -L | 153

*МаВ
см. подключение упоров в шахте, лист 8

**Выключатель натяжного устройства**

SE4

74/73-4*МаГ — 73-3

МКШВ 2х0,5

74/73-4*МаВ — 73-3

**Выключатель двери приямка**

SE13*

73-3 — 73-2

МКШВ 2х0,5

73-3 — 73-2

**Выключатель лестницы приямка**

SE14*

73-2 — 73-1

МКШВ 2х0,5

73-2 — 73-1

**Кнопка "СТОП" дополнительная**

SC3-1*

73-1 — 73

МКШВ 2х0,5

73-1 — 73

**Кнопка "СТОП"**

SC3

73 — 73

МКШВ 2х0,5

73 — 72

HA3

N3 — L314

МКШВ 2х0,5

L314 — N3

L313 | L314 | L315 | N3 | 72 | 74 | 3 | -L | 153

### Блок приямка

XS3: 5 4 3 2 1 / 9 8 7 6 / -L 153 3

XH4 "24В": -L 3

XH7 "220В": N3 L313

ST3: L313 — L315

*К

XT1

| | |
|---|---|
| 1 | L315 |
| 2 | L313 |
| 3 | 153 |
| 4 | -L |
| 5 | 3 |
| 6 | N3 |

МКШВ 7х0,75

* При наличии. При отсутствии установить соответствующие перемычки.
*К – Кабель в комплекте с устройством
*МаВ – Для лифтов с малым верхним этажом

| Изм | Лист | № докум. | Подп. | Дата |
|---|---|---|---|---|
| 7 | | 186.013823-2025 | | |

ФАИД.484440.002 Э4

Лист 15

Инв.№ подл. 4031 | Подп. и дата Черенкова (Подп) 19.12.2025 | Взам. инв. № | Инв.№ дубл. | Подп. и дата | Справ. № | Перв. примен.


IPS ID: 110655800

Список цехов:расцеховок нет.

Копировал

Формат А3

# Устройства безопасности приямка
## Нижнее машинное помещение

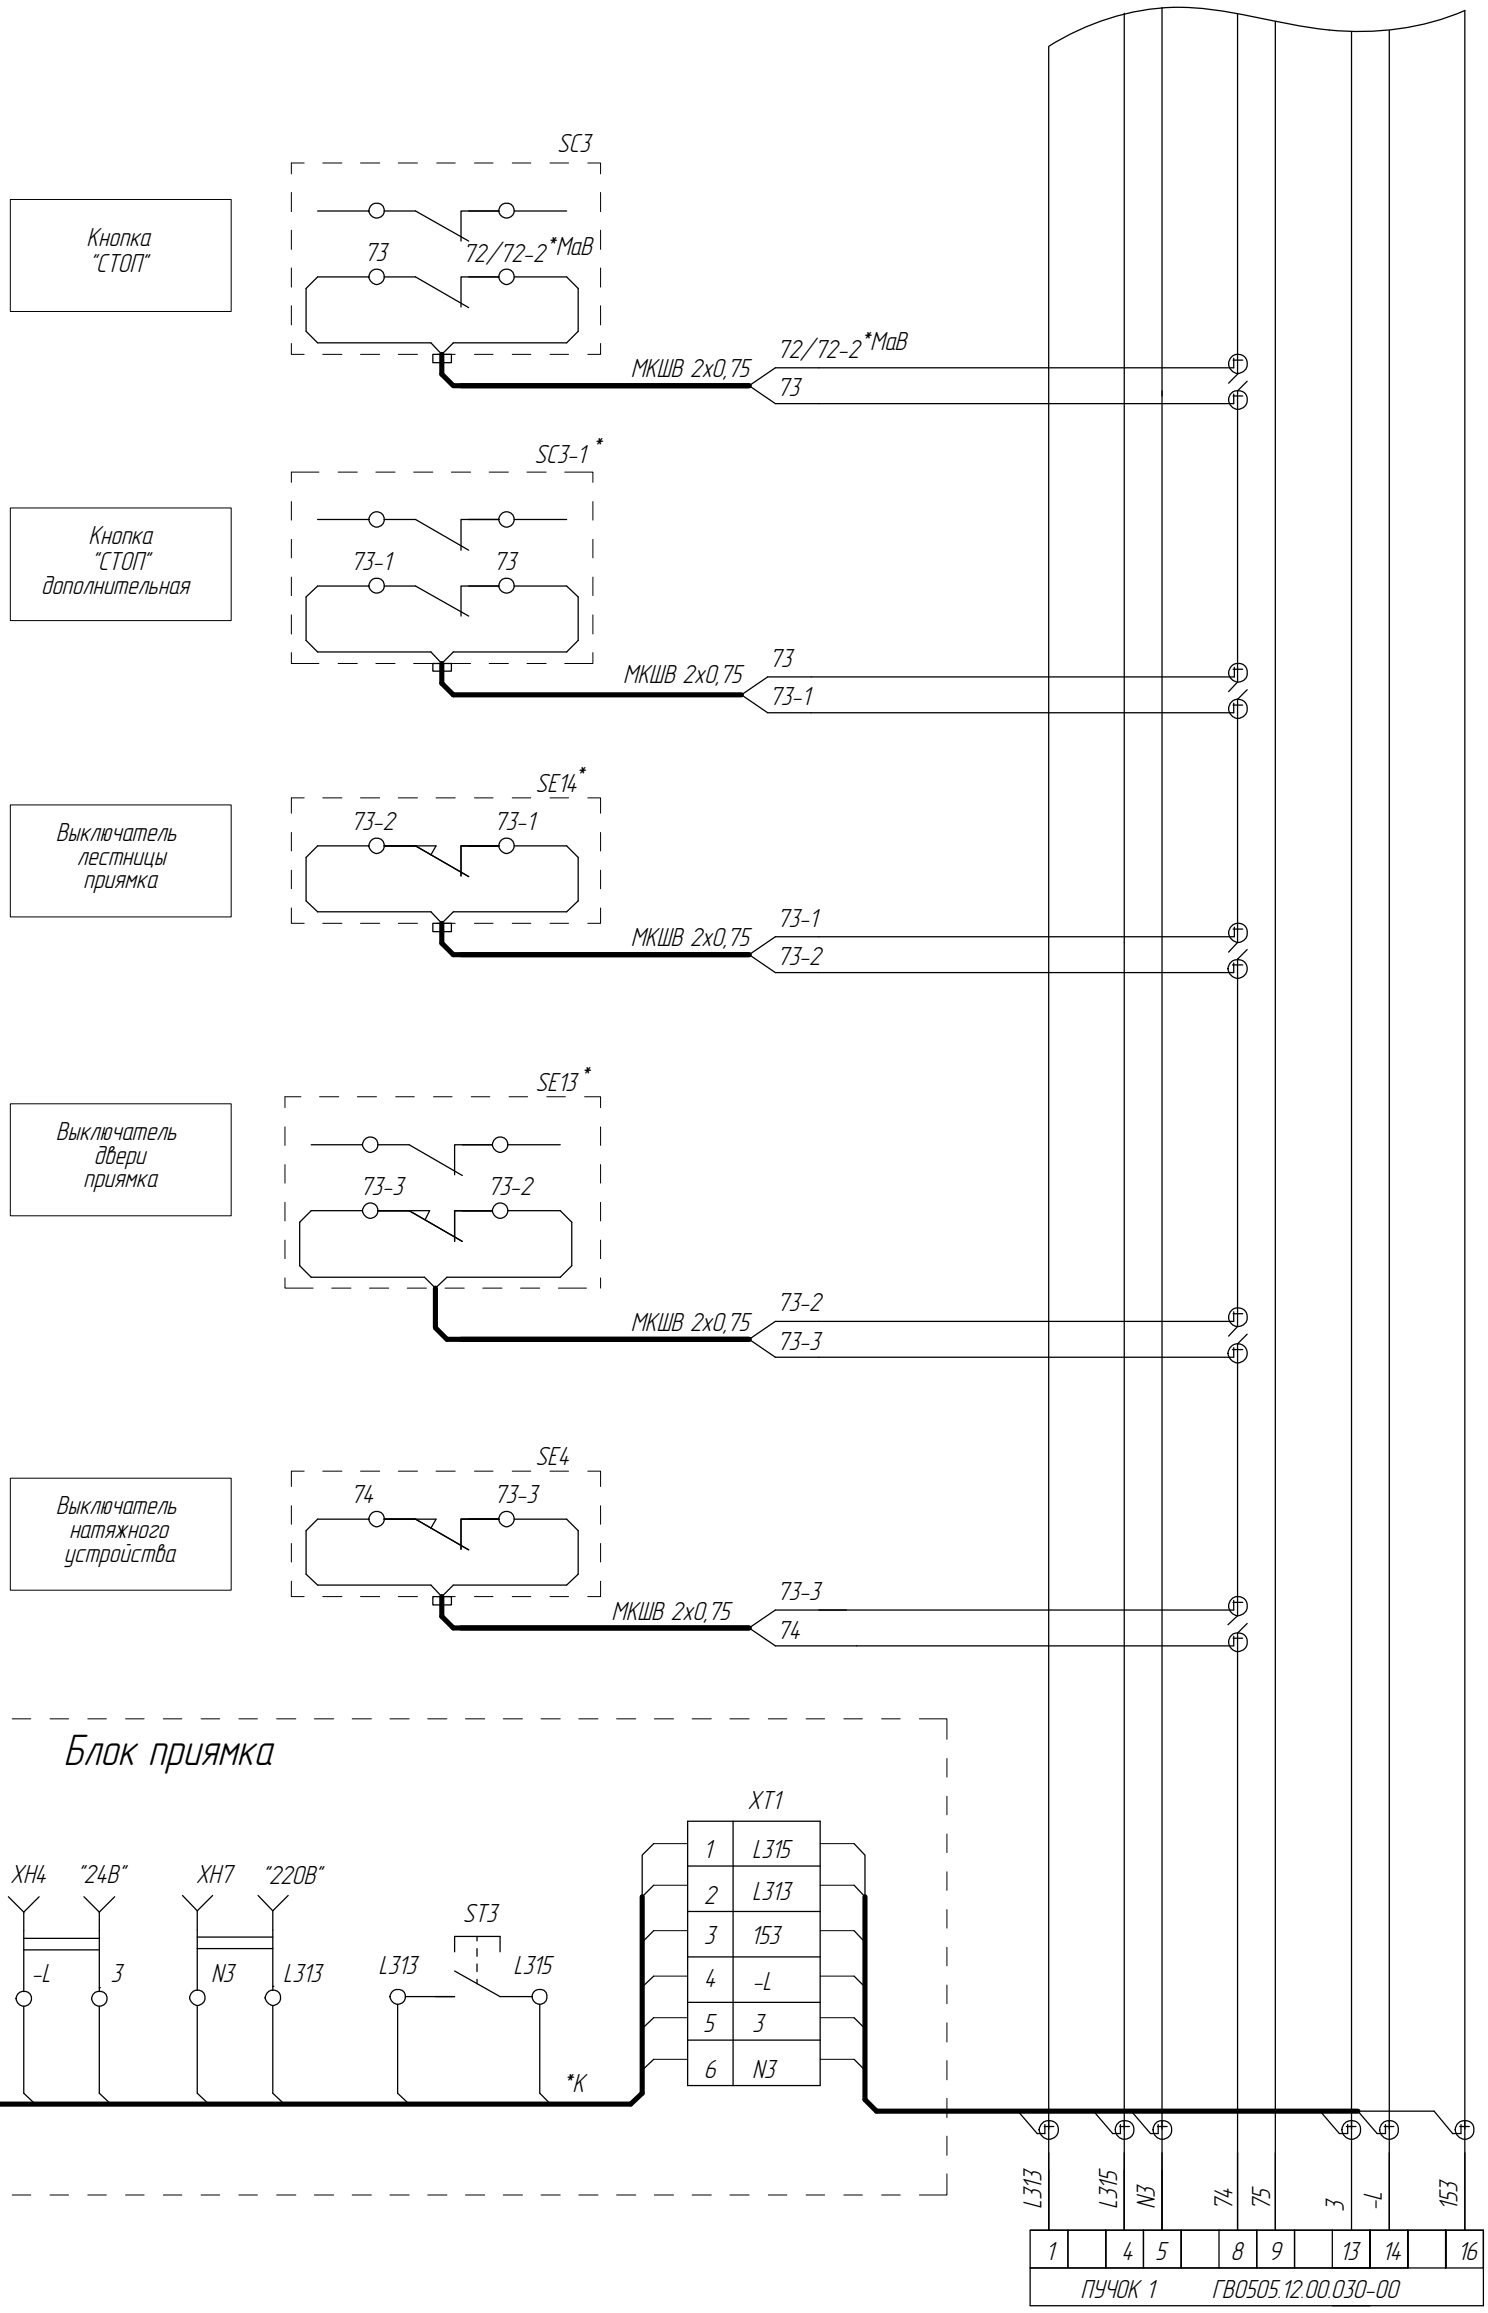


* При наличии. При отсутствии установить соответствующие перемычки.

*К – Кабель в комплекте с устройством

| Изм | Лист | № докум. | Подп. | Дата | ФАИД.484440.002 Э4 | Лист 15а |
|---|---|---|---|---|---|---|
| 7 | | 186.013823-2025 | | | | |

Инв.№ подл. 4031 | Подп. и дата Черенкова (Подп) 19.12.2025 | Взам. инв. № | Инв.№ дубл. | Справ. № | Перв. примен.

Подп. и дата

IPS ID: 110655800 Список цехов: расцеховок нет. Копировал Формат А3

# Подключение подвесных кабелей в щит управления кабины

АК1

ХТ33

| марк. | конт. | цепь | марк. |
|---|---|---|---|
| 501 | 1 | stb 1 | 501 |
| 502 | 2 | stb 2 | 502 |
| 503 | 3 | stb 3 | 503 |
| 507 | 4 | stb 7 | 507 |
| 508 | 5 | stb 8 | 508 |
| 601 | 6 | stb 1 | 601 |
| 605 | 7 | stb 5 | 605 |
| 655 | 8 | Ustb5 | 655 |
| 656 | 9 | Ustb6 | 656 |
| 609 | 10 | Кн.Ревиз. | 609 |

ХТ30

| марк. | конт. | цепь | марк. |
|---|---|---|---|
| 63 | 1 | Шунт ДШ | 63 |
| 64 | 2 | ДЗ | 64 |
| 71 | 3 | Доп.кн "СТОП" | 71 |
| 71-1 | 4 | Кн "СТОП" ПКР | 71-1 |
| 71-2 | 5 | СПК | 71-2 |
| 72 | 6 | "СТОП" приямок | 72 |
| 213 | 7 | ВЛ | 213 |
| | 8 | | |
| | 9 | | |
| | 10 | | |

ХТ34

| марк. | конт. | цепь | марк. |
|---|---|---|---|
| D1 | 1 | Диспетч. связь | D1 |
| D4 | 2 | | D4 |
| M1 | 3 | | M1 |
| M4 | 4 | | M4 |
| 438 | 5 | Взешивающ. ус-во | 438 |
| 606 | 6 | | 606 |
| P3 | 7 | | P3 |
| 439 | 8 | КБР | 439 |
| L318 | 9 | | L318 |
| L319 | 10 | | L319 |

ХТ31

| марк. | конт. | цепь | марк. |
|---|---|---|---|
| 153 | 1 | Тел.связь | 153 |
| | 2 | | |
| 3 | 3 | 24В | 3 |
| 3 | 4 | | 3 |
| 3 | 5 | | 3 |
| 3 | 6 | | 3 |
| -L | 7 | 24В Общ. | -L |
| -L | 8 | | -L |
| -L | 9 | | -L |
| -L | 10 | | -L |

ХТ35

| марк. | конт. | цепь | марк. |
|---|---|---|---|
| 70 | 1 | ДК | 70 |
| 70-1 | 2 | ДК | 70-1 |
| 70-2 | 3 | ДК | 70-2 |
| 70-3 | 4 | ДК | 70-3 |
| 70-4 | 5 | ДК1 | 70-4 |
| 70-5 | 6 | ДК1 | 70-5 |
| 70-6 | 7 | ДК1 | 70-6 |
| 70-7 | 8 | ДК1 | 70-7 |
| | 9 | | |
| | 10 | | |

ХТ32

| марк. | конт. | цепь | марк. |
|---|---|---|---|
| L312 | 1 | Освещ. | L312 |
| L313 | 2 | Зв. каб | L313 |
| L315 | 3 | Кн. тел. св | L315 |
| N | 4 | Общ. 220В | N |
| N | 5 | | N |
| N3 | 6 | 313 N | N3 |
| | 7 | | |
| 342 | 8 | Отводка 1 | 342 |
| | 9 | | |
| 342-1 | 10 | Отводка 2 | 342-1 |

ХТ37

| марк. | конт. | цепь | марк. |
|---|---|---|---|
| 74-03 | 1 | Склд.пер. | 74-03 |
| 74-04 | 2 | | 74-04 |
| 74-05 | 3 | | 74-05 |
| 74-06 | 4 | | 74-06 |
| | 5 | | |
| | 6 | | |
| | 7 | | |
| | 8 | | |
| | 9 | | |
| | 10 | | |

ГВ0505.12.00.050-01
КПЛМ-18х0,75
4.2

ГВ0505.12.00.050-00
КПЛМ-18х0,75
4.1

*2- Для лифтов с тремя выключателями упоров.

ФАИД.484440.002 Э4

| Изм | Лист | № докум. | Подп. | Дата |
|---|---|---|---|---|
| 7 | | 186.013823-2025 | | |

Лист 16

ФАИД.484440.002 Э4

Перв. примен.

Справ. №

Инв.№ подл. 4031 | Подп. и дата Черенкова (Подп) 19.12.2025 | Взам. инв. № | Инв.№ дубл. | Подп. и дата


IPS ID: 110655800

Список цехов-расцеховок нет.

Копировал

Формат А3

# Подключение поста ревизии на крыше кабины (маркировка выводов кабеля ПКР указана в скобках)

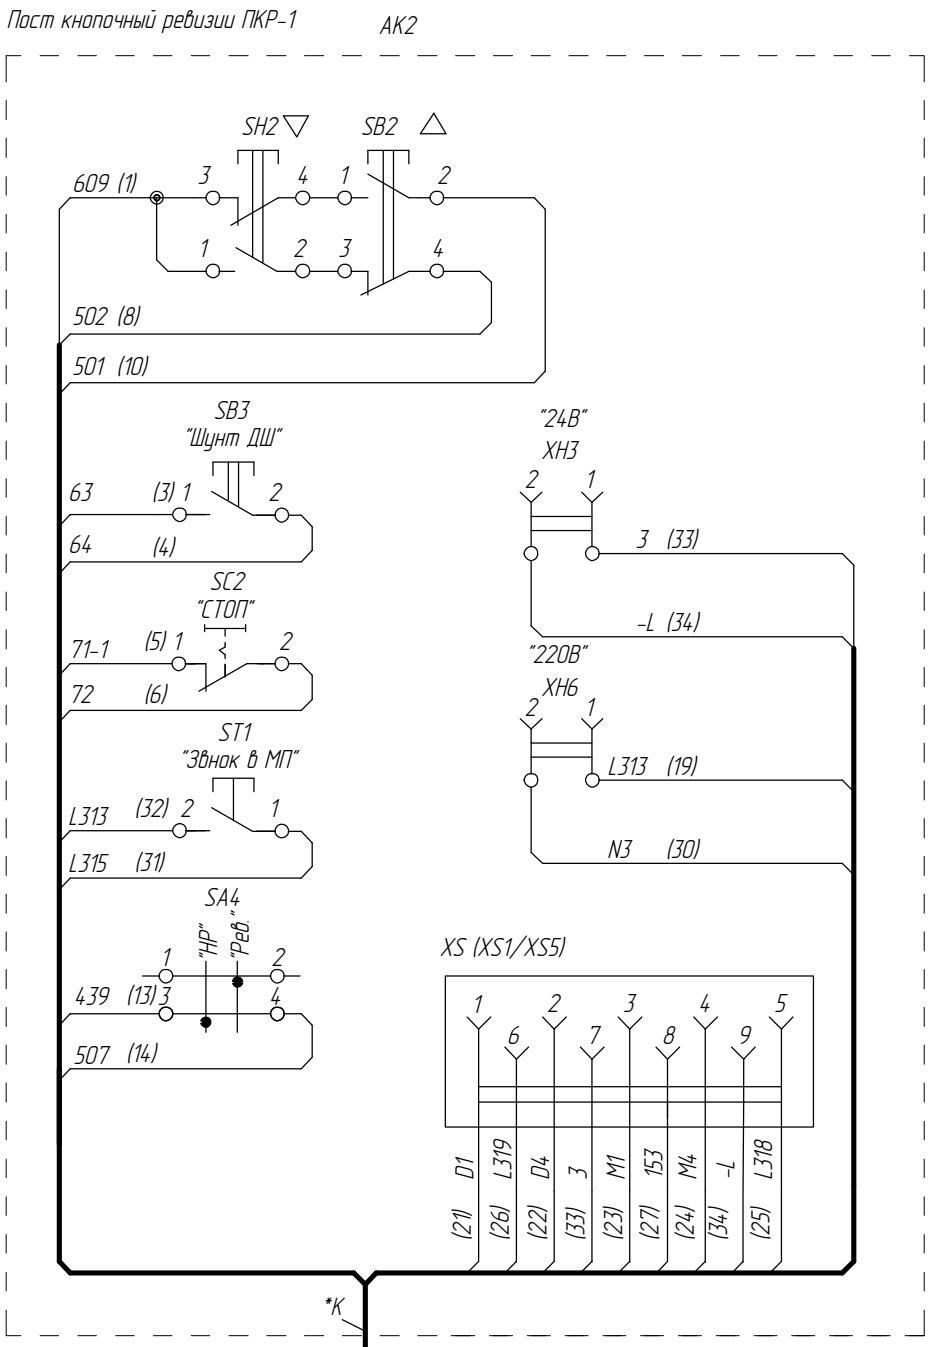


| марк. | к. | марк. |
|---|---|---|
| 501 | 1 | 501 |
| 502 | 2 | 502 |
| 503 | 3 | 503 |
| 507 | 4 | 507 |
| 508 | 5 | 508 |
| 601 | 6 | 601 |
| 605 | 7 | 605 |
| 655 | 8 | 655 |
| 656 | 9 | 656 |
| 609 | 10 | 609 |

(10) (8) (14) (1)

| марк. | к. | марк. |
|---|---|---|
| 63 | 1 | 63 |
| 64 | 2 | 64 |
| 71 | 3 | 71 |
| 71-1 | 4 | 71-1 |
| 71-2 | 5 | 71-2 |
| 72 | 6 | 72 |
| 213 | 7 | 213 |
| | 8 | |
| | 9 | |
| | 10 | |

(3) (4) (5) (6)

| марк. | к. | марк. |
|---|---|---|
| D1 | 1 | D1 |
| D4 | 2 | D4 |
| M1 | 3 | M1 |
| M4 | 4 | M4 |
| 438 | 5 | 438 |
| 606 | 6 | 606 |
| P3 | 7 | P3 |
| 439 | 8 | 439 |
| L318 | 9 | L318 |
| L319 | 10 | L319 |

(21) (22) (23) (24) (13) (25) (26)

| марк. | к. | марк. |
|---|---|---|
| 153 | 1 | 153 |
| | 2 | |
| 3 | 3 | 3 |
| 3 | 4 | 3 |
| 3 | 5 | 3 |
| 3 | 6 | 3 |
| -L | 7 | -L |
| -L | 8 | -L |
| -L | 9 | -L |
| -L | 10 | -L |

(27) (33) (34)

| марк. | к. | марк. |
|---|---|---|
| L312 | 1 | L312 |
| L313 | 2 | L313 |
| L315 | 3 | L315 |
| N | 4 | N |
| N | 5 | N |
| N3 | 6 | N3 |
| | 7 | |
| 342 | 8 | 342 |
| | 9 | |
| 342-1 | 10 | 342-1 |

(32) (19) (31) (30)


*K – Кабель в комплекте с устройством

| Изм | Лист | № докум. | Подп. | Дата | 186.013823-2025 | ФАИД.484440.002 Э4 | Лист 17 |
|---|---|---|---|---|---|---|---|

Инв.№ подл. 4031 | Подп. и дата Черенкова (Подп) 19.12.2025 | Взам. инв. № | Инв.№ дубл. | Подп. и дата | Справ. № | Перв. примен.

IPS ID: 110655800 Список цехов-расцеховок нет. Копировал Формат А3

# Подключение поста ревизии на крыше кабины при наличии складных перил (маркировка выводов кабеля ПКР указана в скобках)

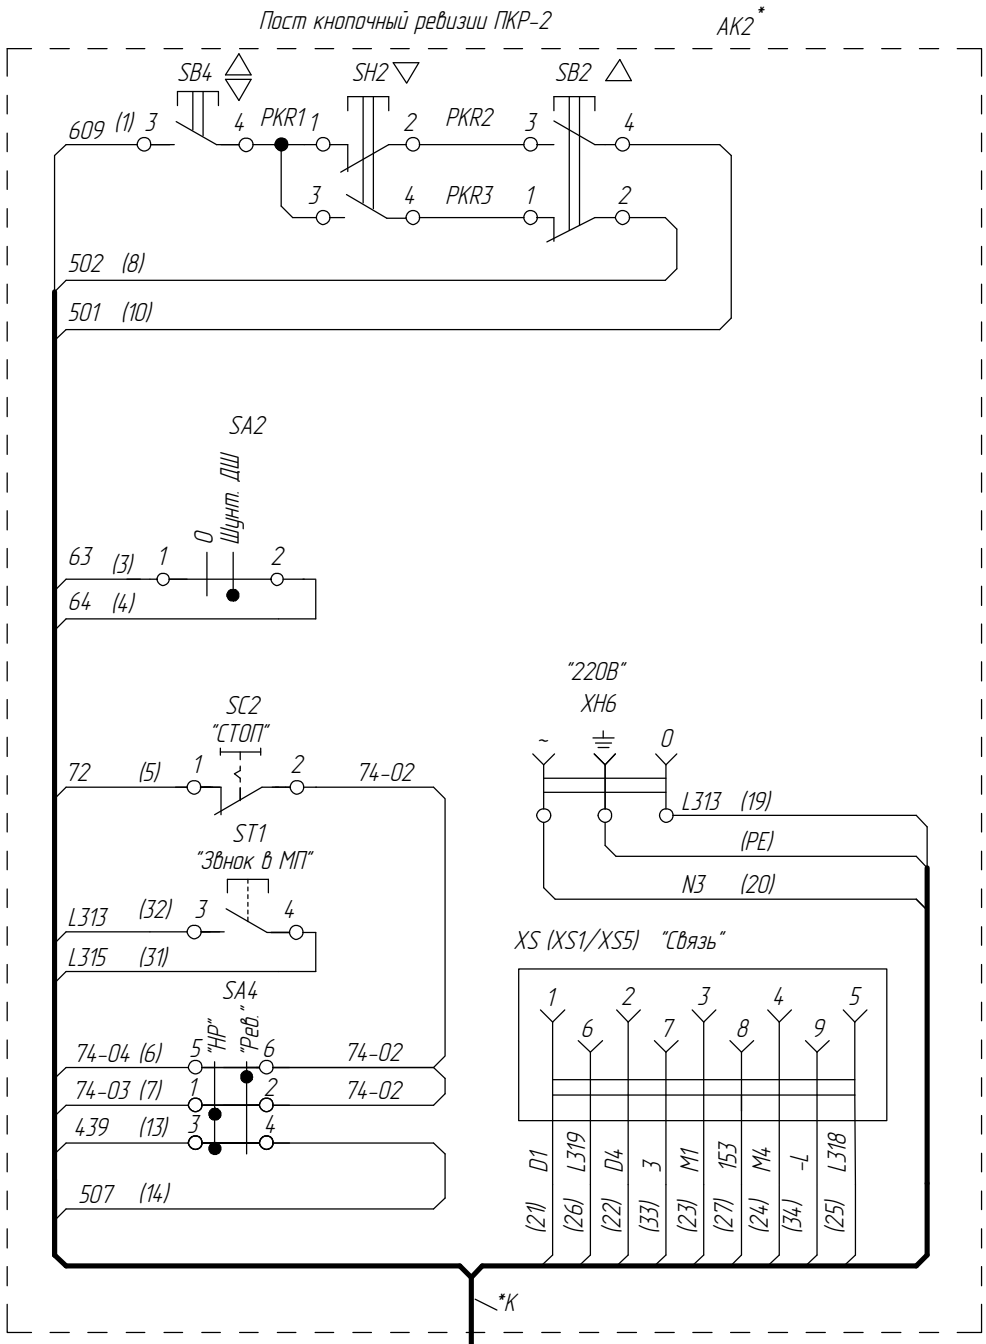


*K – Кабель в комплекте с устройством

| | | | | | |
|---|---|---|---|---|---|
| 7 | | 186.013823-2025 | | | ФАИД.484440.002 Э4 |
| Изм. | Лист | № докум. | Подп. | Дата | |

Лист 17а

Перв. примен.

Справ. №

Подп. и дата

Инв.№ дубл.

Взам. инв. №

Подп. и дата 19.12.2025 (Подп) Черенкова

Инв.№ подл. 4031


IPS ID: 110655800

Список цехов: расцеховок нет.


Копировал

Формат А3

# Подключение устройств безопасности кабины и датчиков

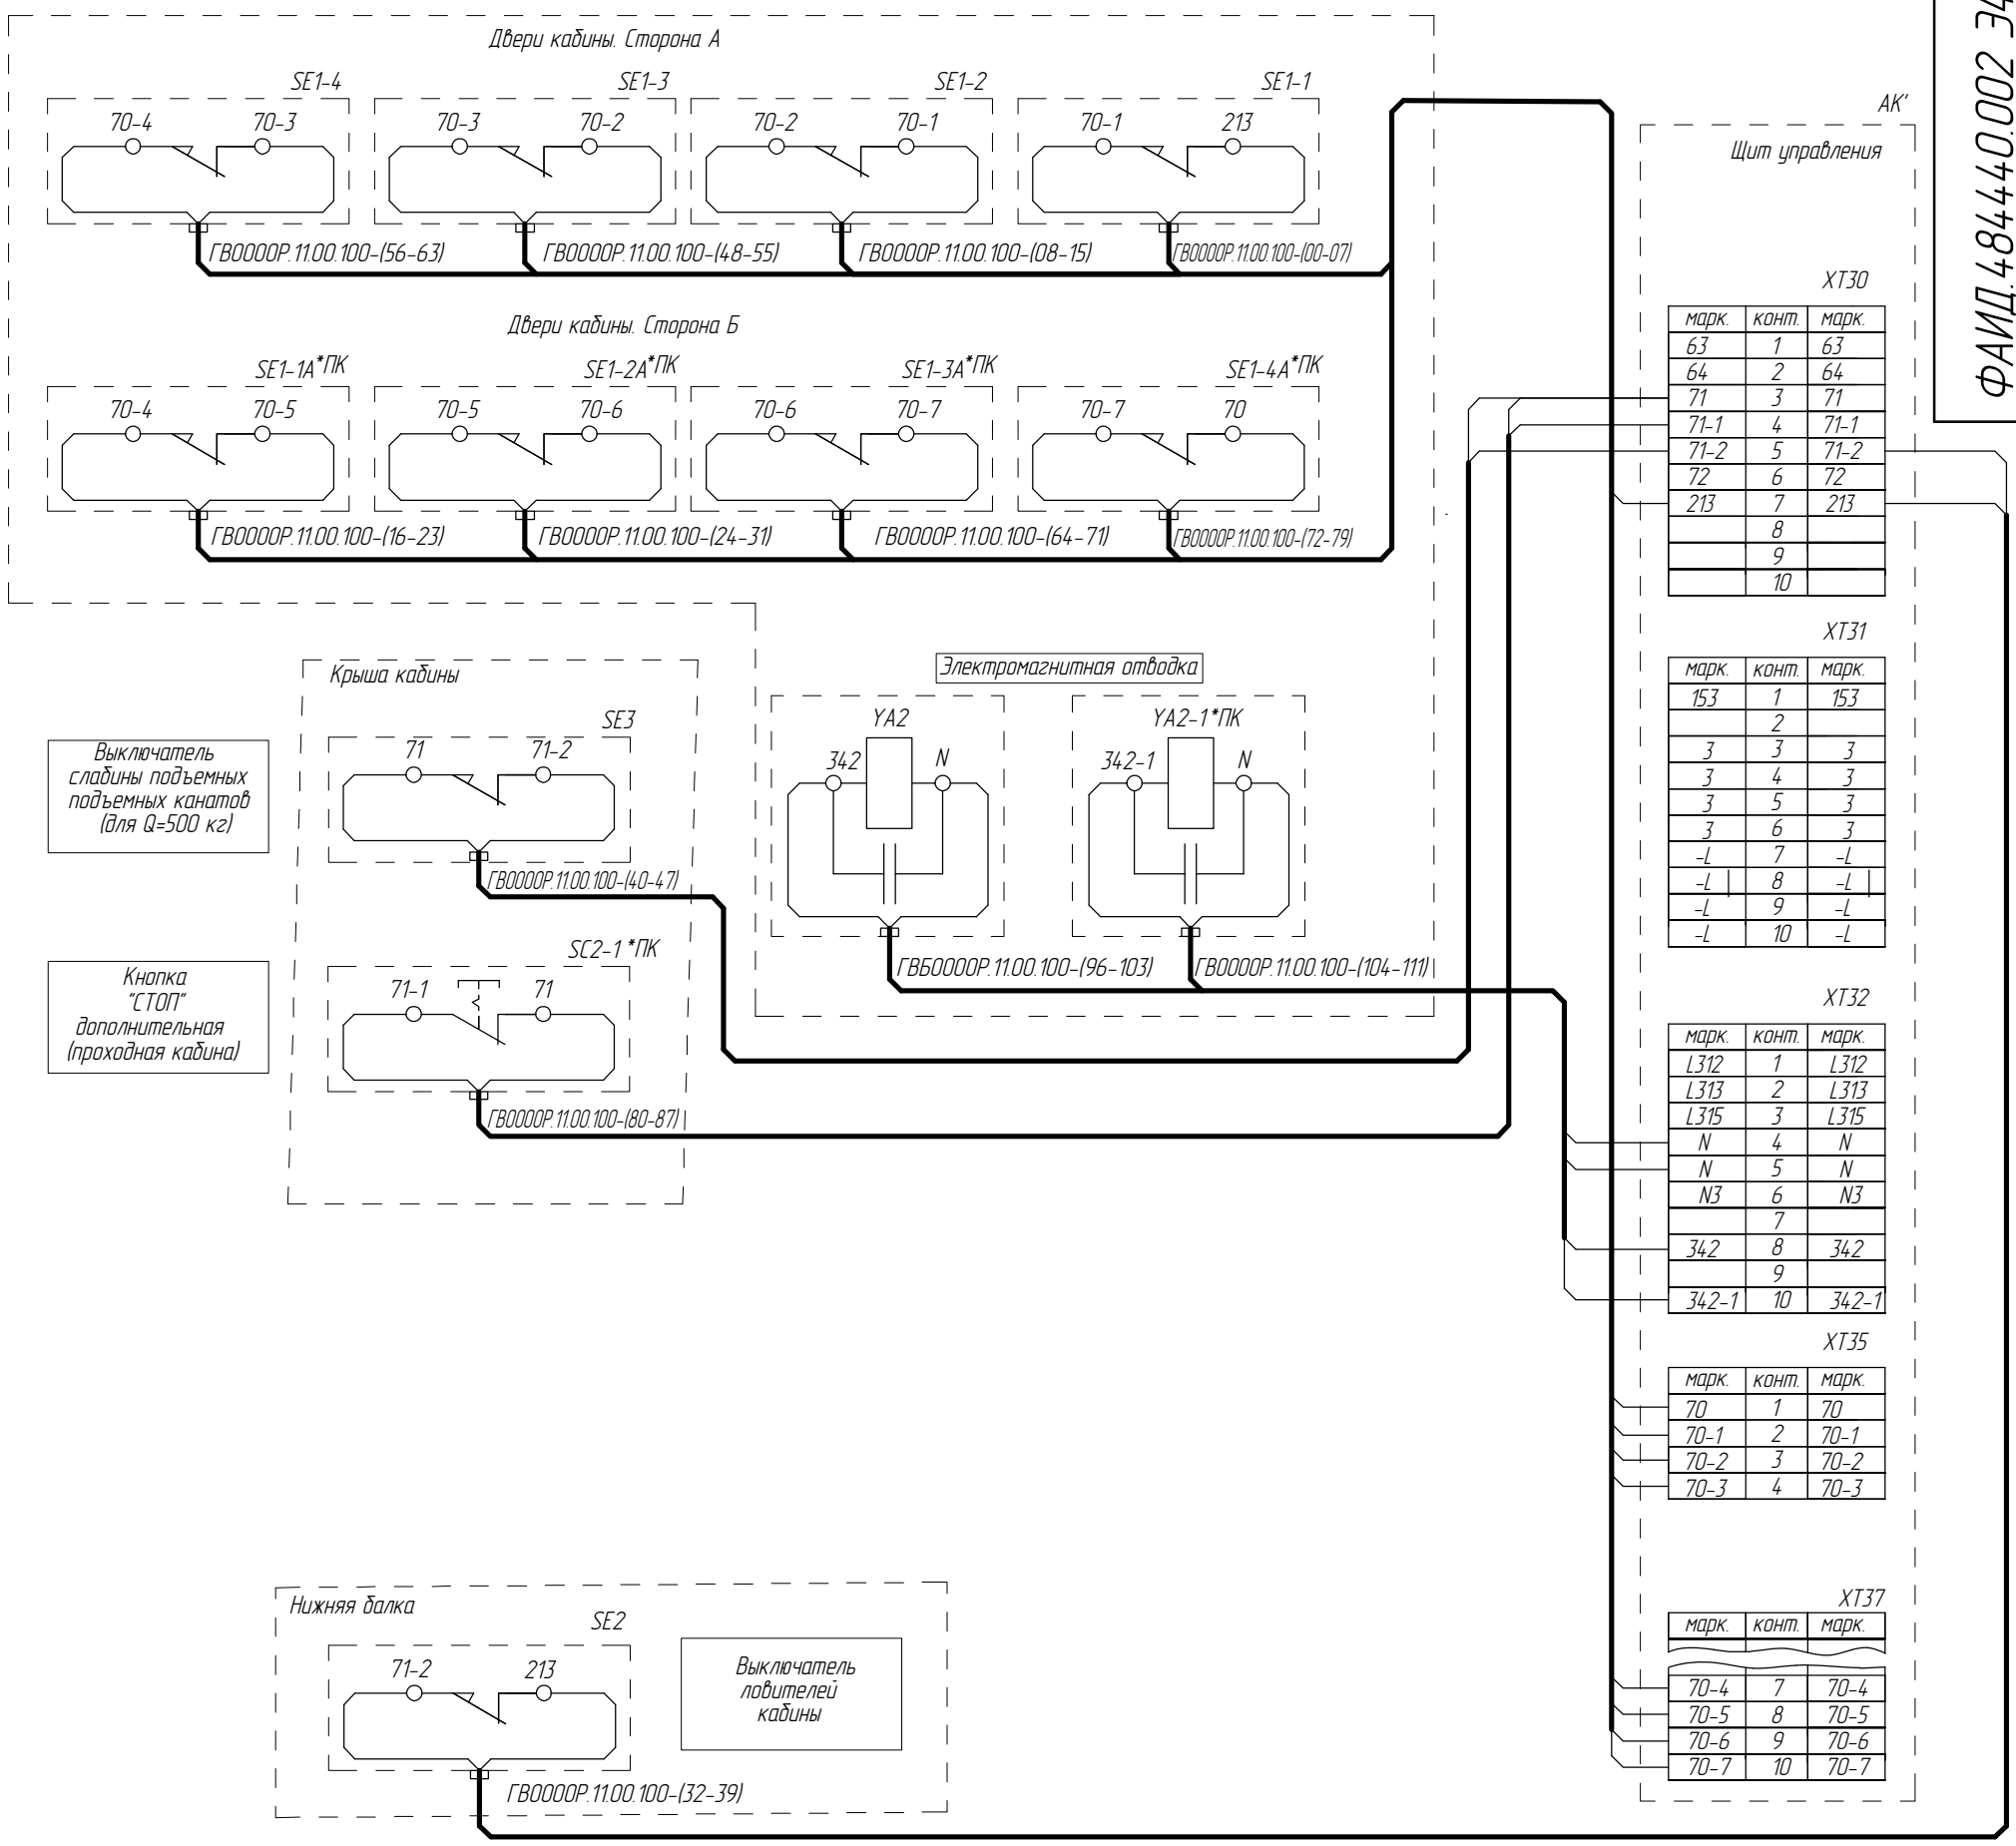


# Подключение датчиков замедления и точной остановки (ВПЛ)

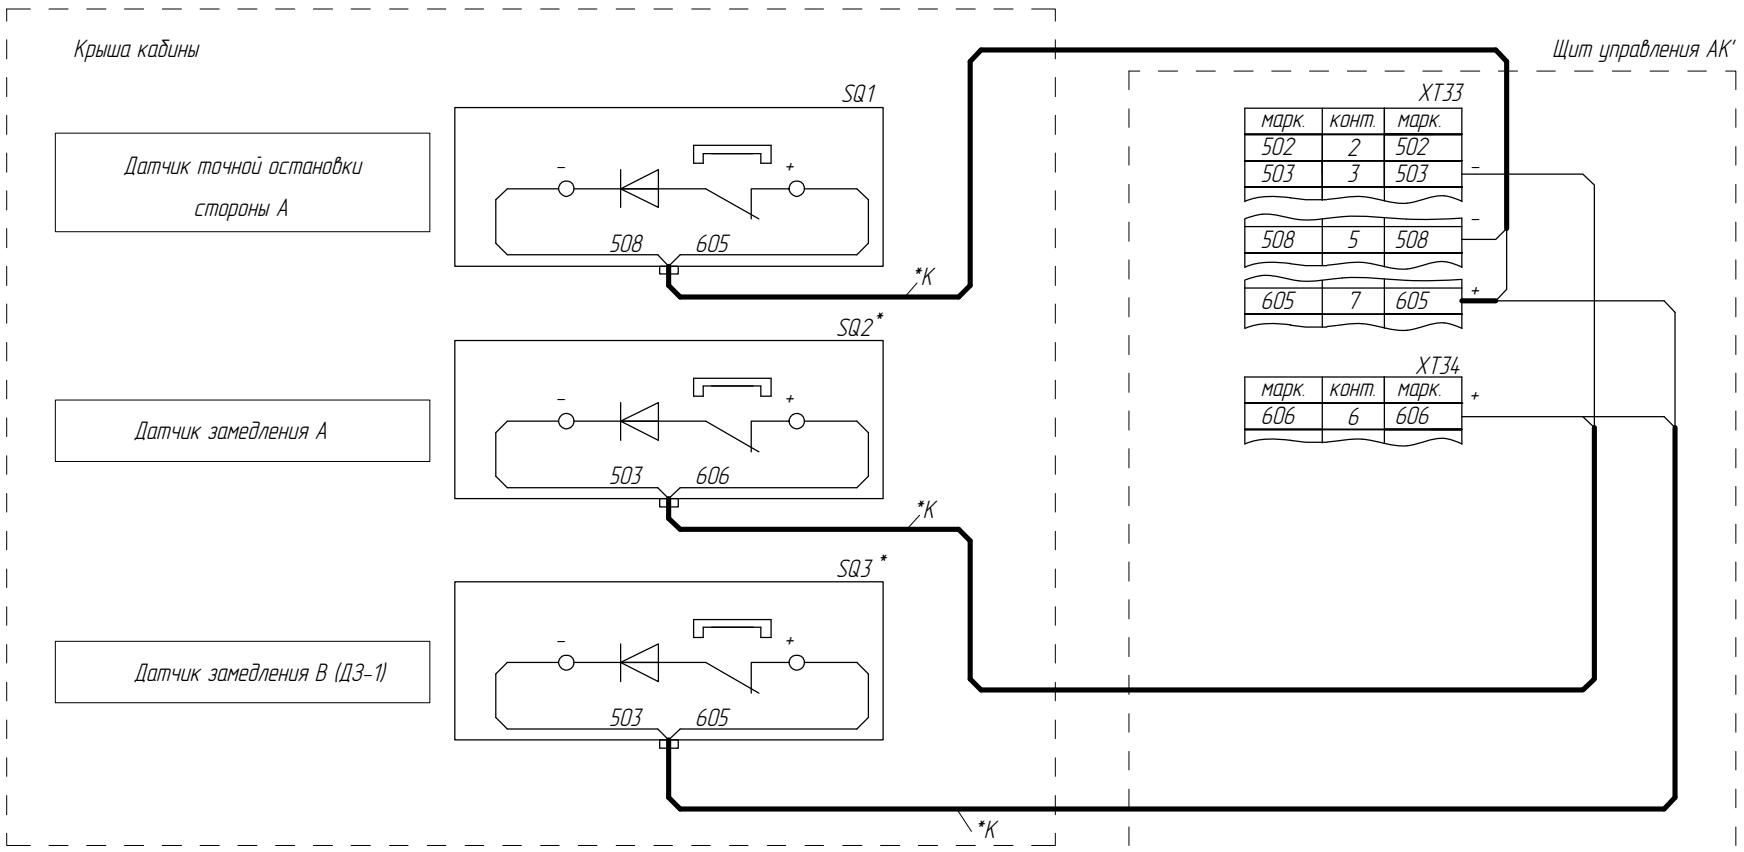


*К – Кабель в комплекте с устройством
*ПК – Для лифтов с проходной кабиной

| Изм | Лист | № докум. | Подп. | Дата |
|---|---|---|---|---|
| 7 | | 186.013823-2025 | | |

ФАИД.484440.002 Э4

Лист 18

Перв. примен.

Справ. №

Подп. и дата

Инв.№ подл. 4031 | Подп. и дата Черенкова (Подп) 19.12.2025 | Взам. инв. № | Инв.№ дубл. | Подп. и дата

IPS ID: 110655800

Список цехов-расцеховок нет.


Копировал

Формат А3


# Подключение складных перил крыши кабины

ФАИД.484440.002 Э4

Вариант 1

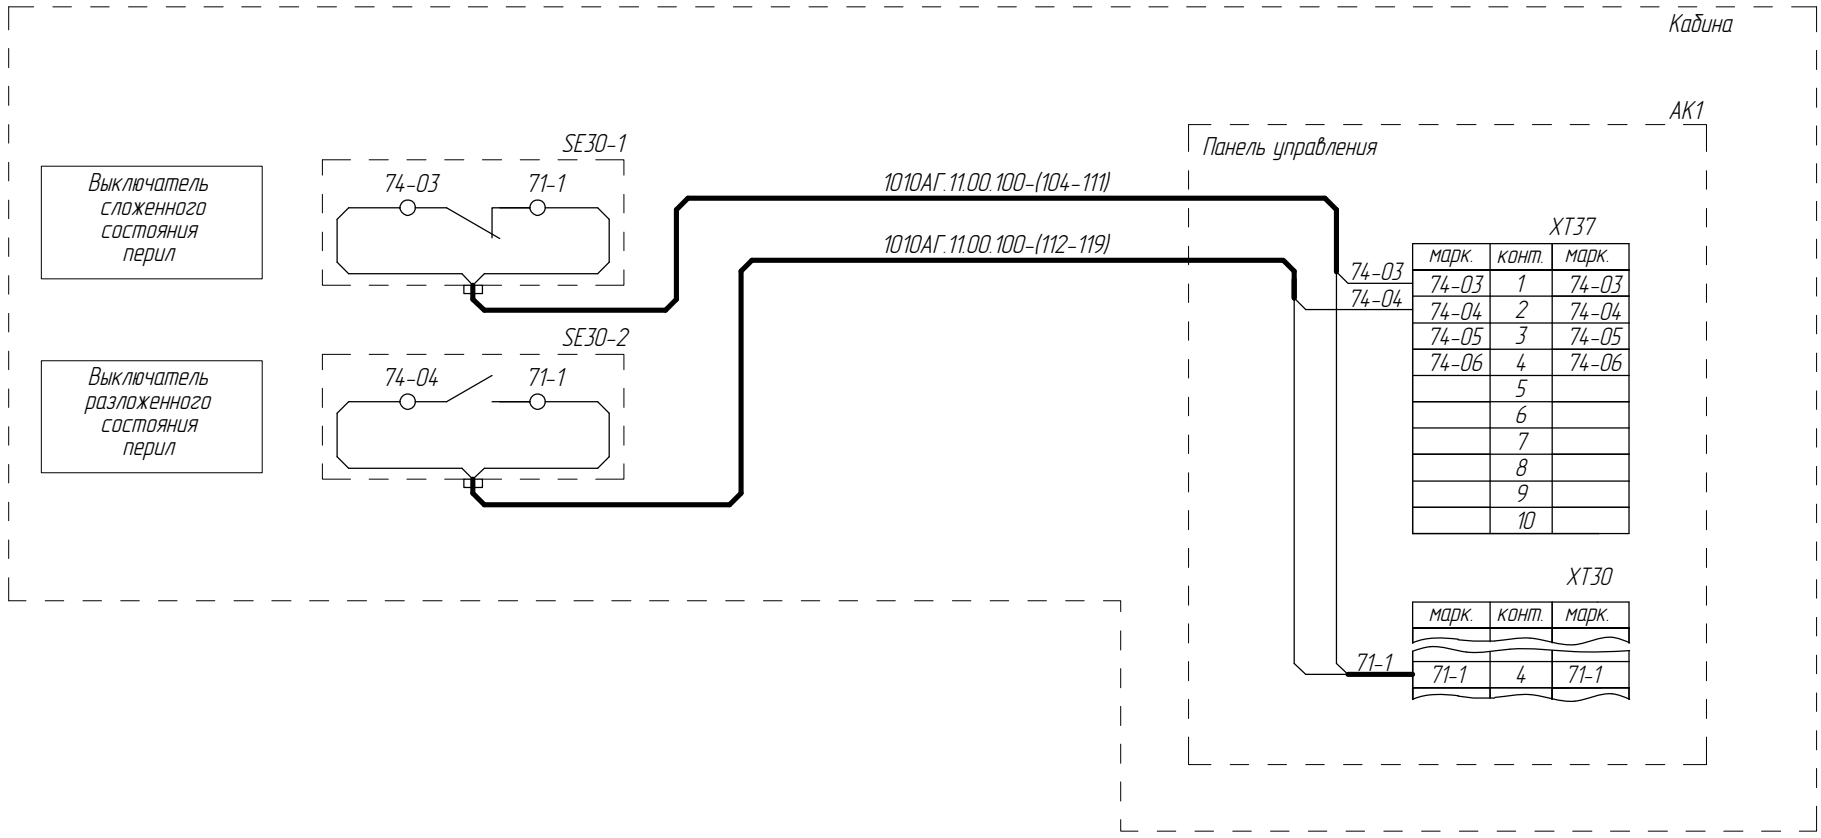


Вариант 2

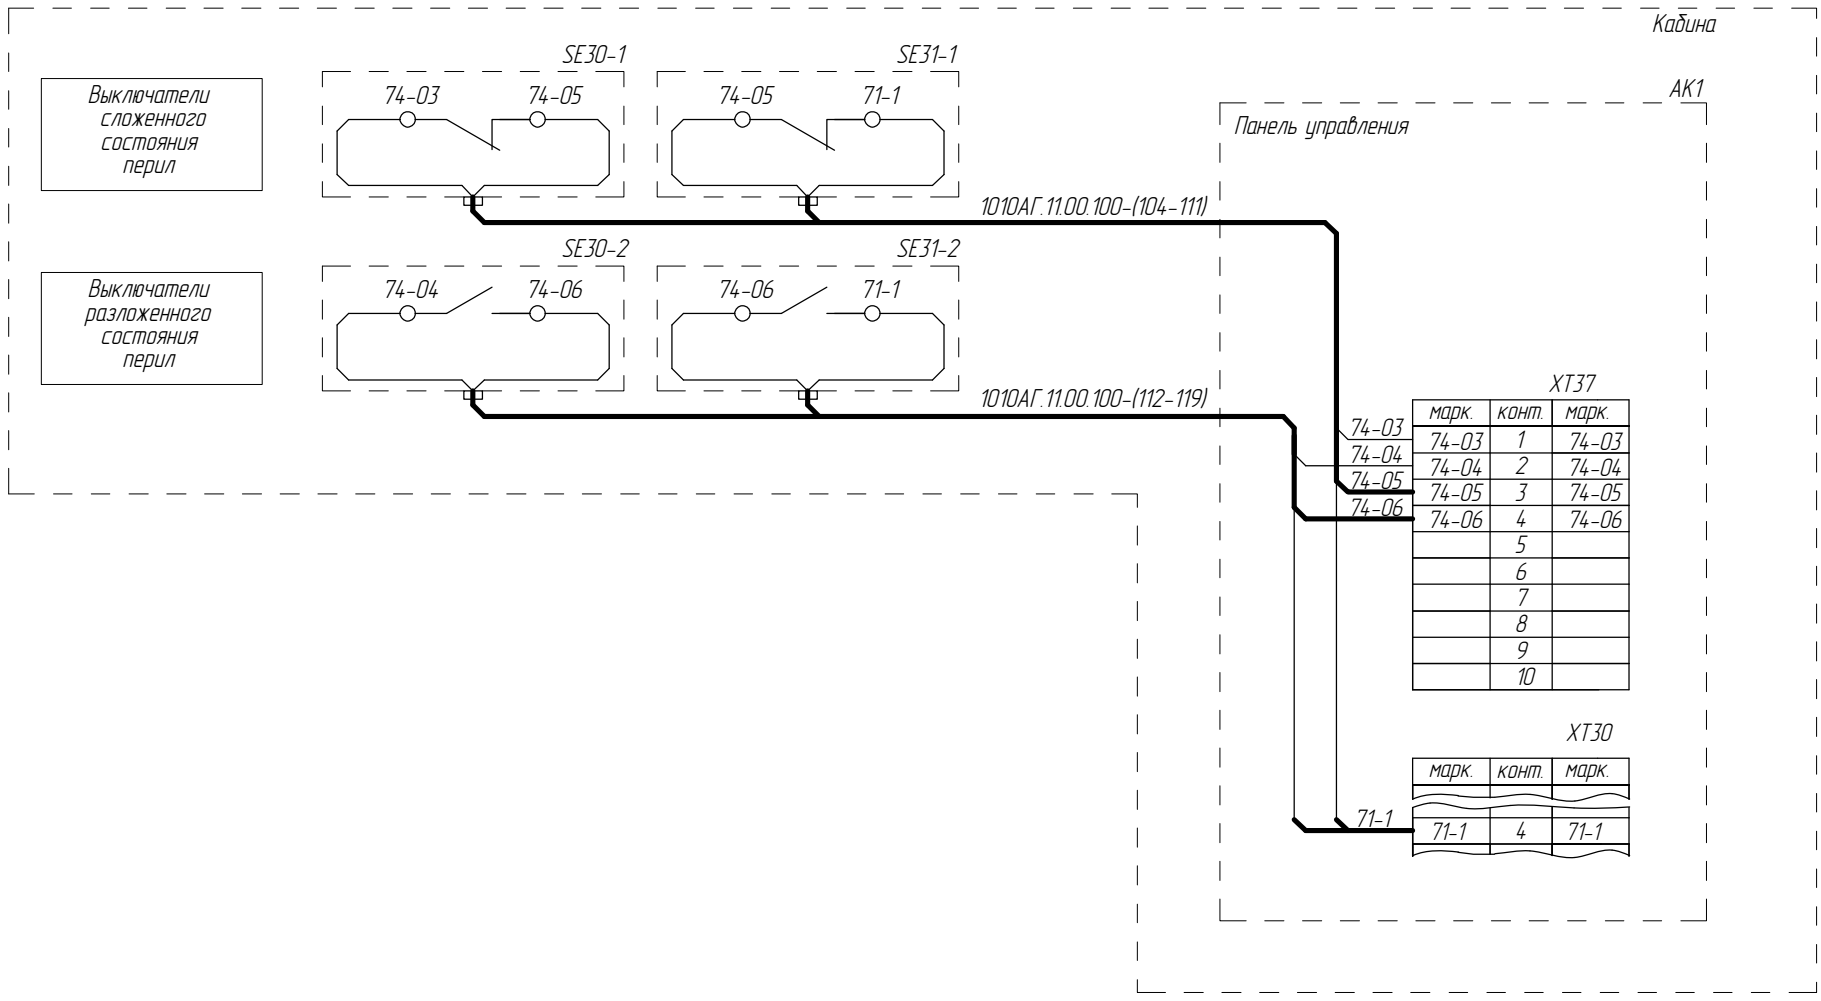


Перв. примен.

Справ. №

| Инв.№ подл. | Подп. и дата | Взам. инв. № | Инв.№ дубл. | Подп. и дата |
|---|---|---|---|---|
| 4031 | Черенкова (Подп) 19.12.2025 | | | |

| | | | | | |
|---|---|---|---|---|---|
| 7 | | 186.013823-2025 | | | ФАИД.484440.002 Э4 |
| Изм. | Лист | № докум. | Подп. | Дата | |

Лист 19

IPS ID: 110655800

Список цехов-расцеховок нет.

Копировал

Формат А3

# Подключение освещения

Вариант 3

Рабочее освещение кабины

Для светодиодных светильников 220V AC

EL9 EL8 EL7 EL6

EL5 EL4 EL3 EL2

L N L312

ФБИР.685621.043-(64-71)

АК1

XT32

| марк. | конт. | марк. |
|---|---|---|
| L312 | 1 | L312 |
| N | 4 | N |

*К

+67В -67В G2.1

L312 N ФБИР.685621.043-(64-71)

*К

+67В-1 -67В-1 G2.2

Панель управления основная

Вариант 1

Рабочее освещение кабины

**2х0,5

+67В -67В EL9.1 EL8.1 EL7.1 EL6.1

+БП +БП -БП -БП

1 2

EL9.2 EL8.2 EL7.2 EL6.2

EL1.3

+ + Авар.осв.- Авар.осв.-

**2х0,5 Для светодиодных светильников 67V DC

Вариант 2

Рабочее освещение кабины

+67В-1 -67В-1 EL5 EL4 EL3 EL2

EL1.2 EL1.1

1. К одному блоку питания допускается подключать:
   - не более 4-х длинных светодиодных линеек (см. потолок 1);
   - не более 4-х пар коротких светодиодных линеек (см. потолок 2);
2. Допускается подключатель не более 4-х ламп аварийного освещения.

*К - Кабель в комплекте с устройством

**провод ПВ3

*К - Кабель в комплекте с устройством

| Изм | Лист | № докум. | Подп. | Дата |
|---|---|---|---|---|
| 7 | | 186.013823-2025 | | |

ФАИД.484440.002 Э4

Лист 20

Перв. примен.

Справ. №

Подп. и дата

Инв.№ дубл.

Взам. инв. №

Подп. и дата (Подп) Черенкова 19.12.2025

Инв.№ подл. 4031


IPS ID: 110655800


Список цехов-расцеховок нет.

Копировал

Формат А3

# Подключение освещения кабины 24В

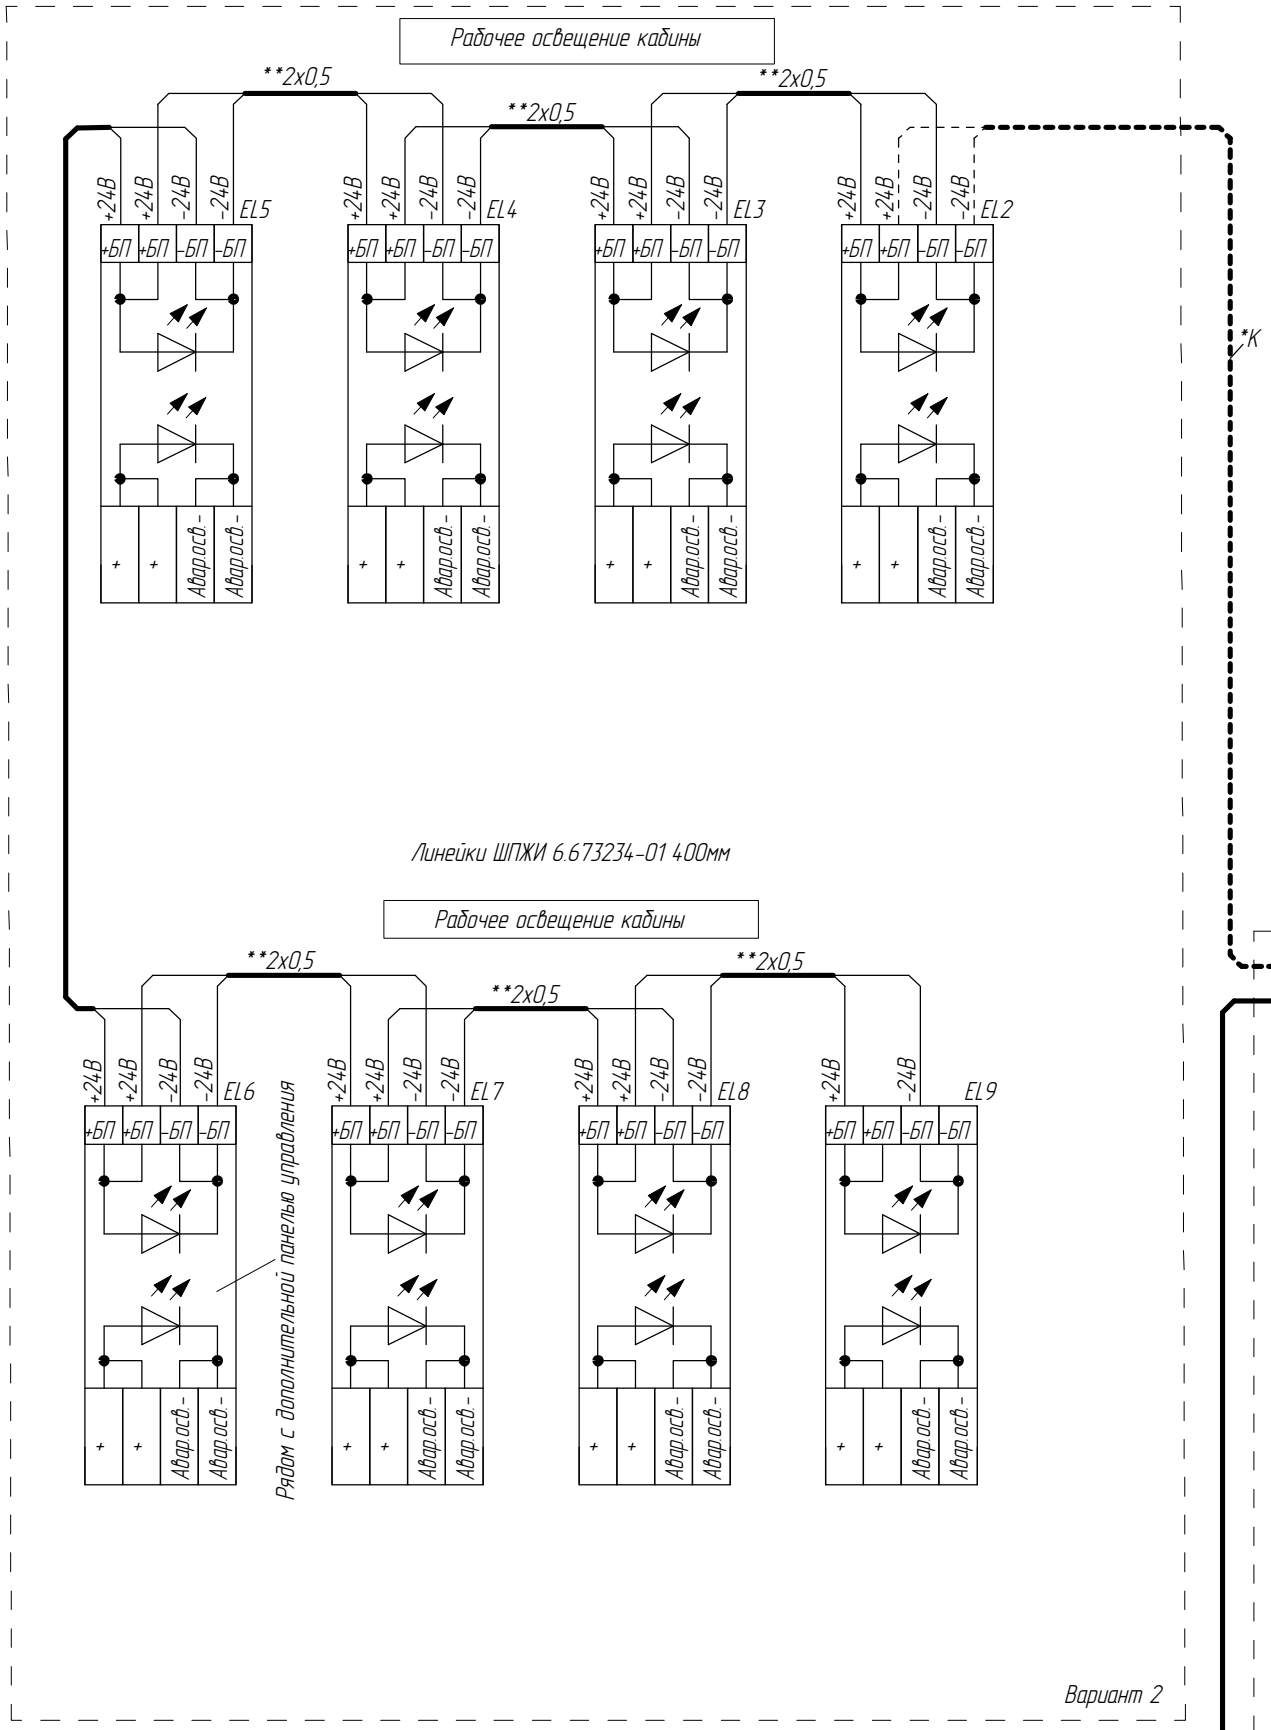

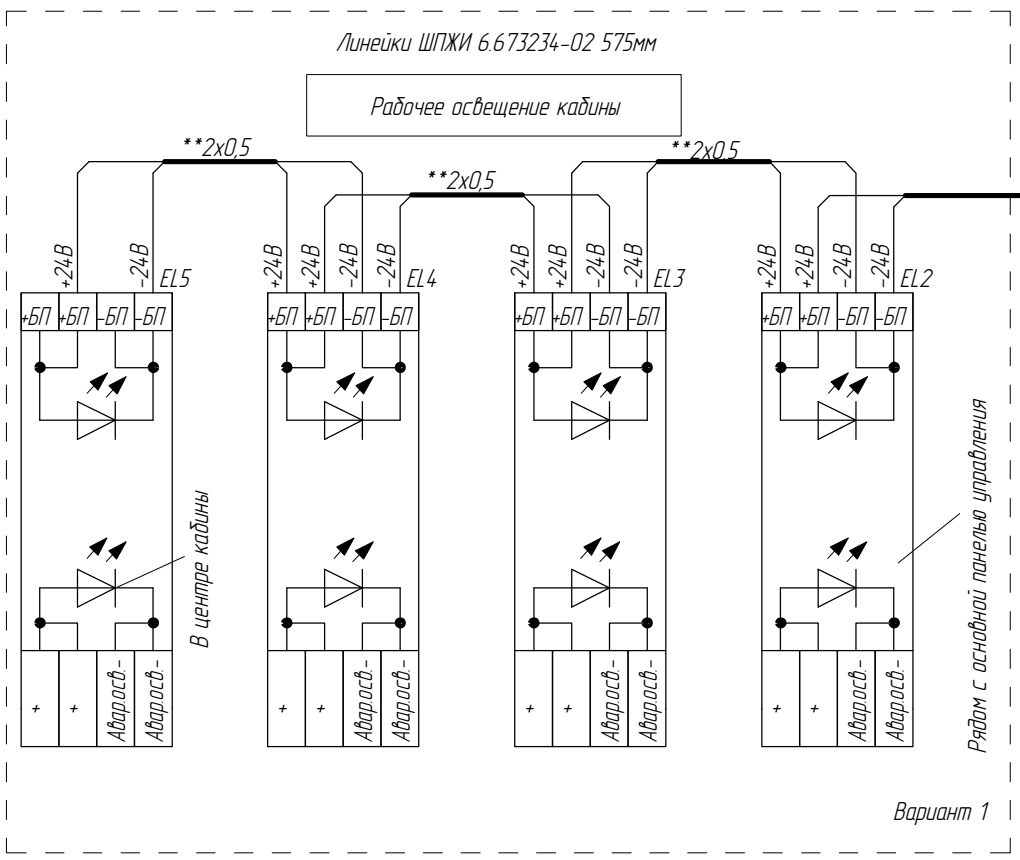
1. К одному блоку питания допускается подключать:
   - не более 4-х длинных светодиодных линеек (см. потолок 1);
   - не более 4-х пар коротких светодиодных линеек (см. потолок 2);
2. Допускается подключатель не более 4-х ламп аварийного освещения.

*К - Кабель в комплекте с устройством

**провод ПВ3

| Изм | Лист | № докум. | Подп. | Дата | ФАИД.484440.002 Э4 | Лист 20а |
|---|---|---|---|---|---|---|
| 7 | | 186.013823-2025 | | | | |

ФАИД.484440.002 Э4

Перв. примен.

Справ. №

Подп. и дата | Инв.№ подл. | 4031 | Черенкова (Подп) 19.12.2025

Взам. инв. № | Инв.№ дубл. | Подп. и дата


# Подключение устройств контроля загрузки кабины
# Взвешивающего устройства отдельно от кабины

ФАИД.484440.002 Э4

Устройство грузовзвешивающее ГУ-01 "Зенит"

Устройство контроля загрузки УКЗ-ВТ


Машинное помещение (лифты с верх. МП г/п > 500 кг) или шахта (вблизи канатной подвески)

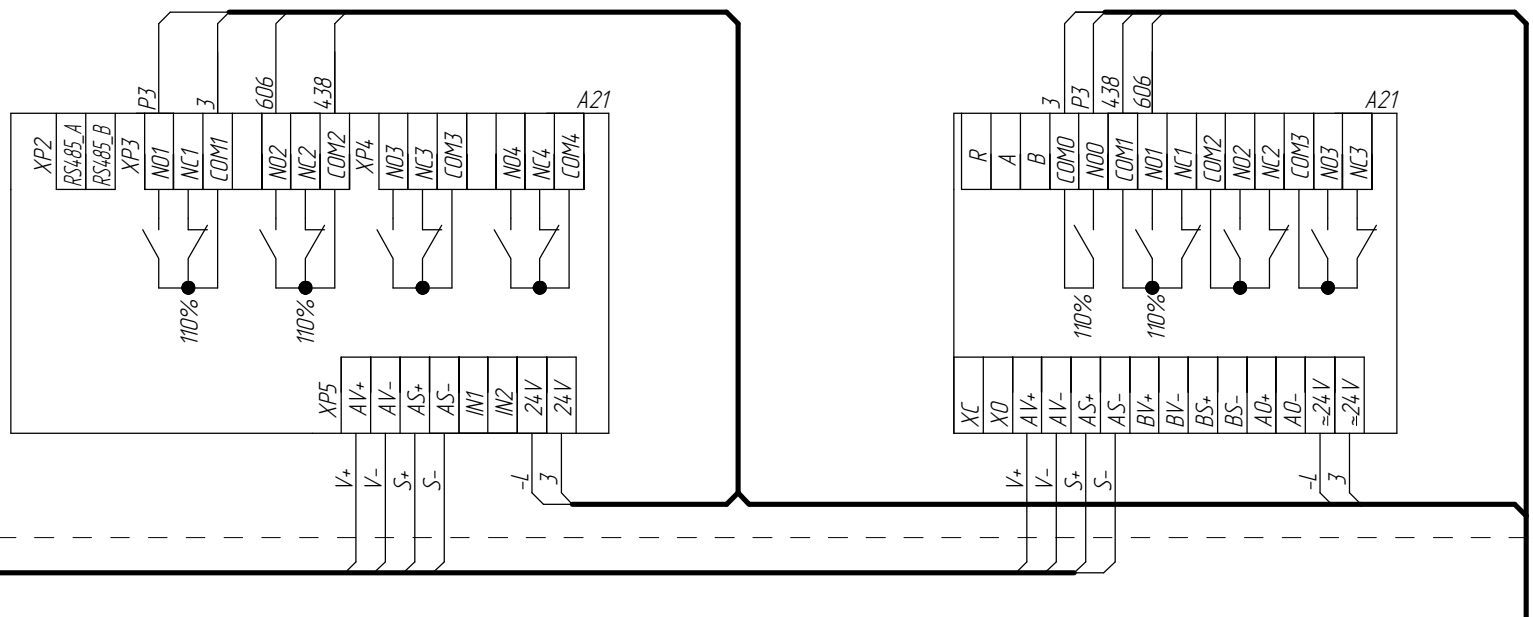


МКШВ 7х0,5 *ВМП

к УЛ

*НМП

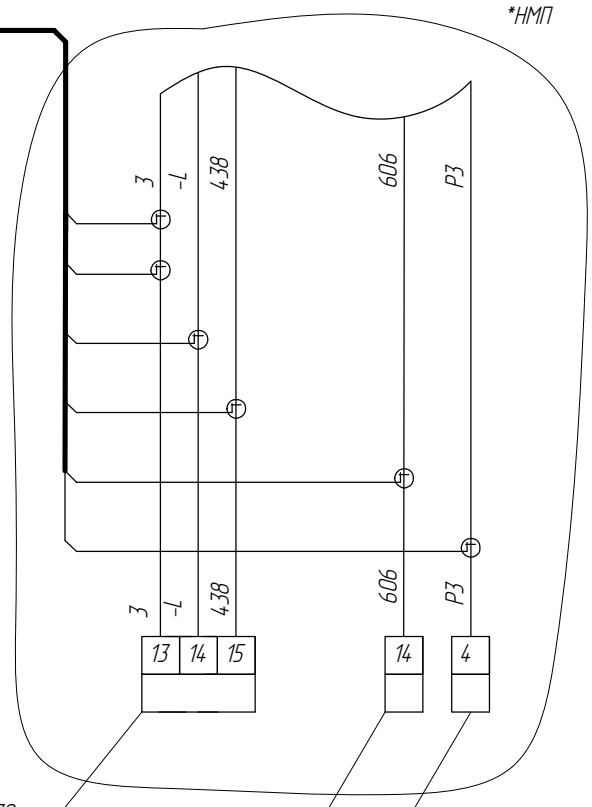



ГВ0505.12.00.030
Пучок 1

ГВ0505.12.00.030-01
Пучок 2

ГВ0505.12.00.030-03
Пучок 3

Канатная подвеска

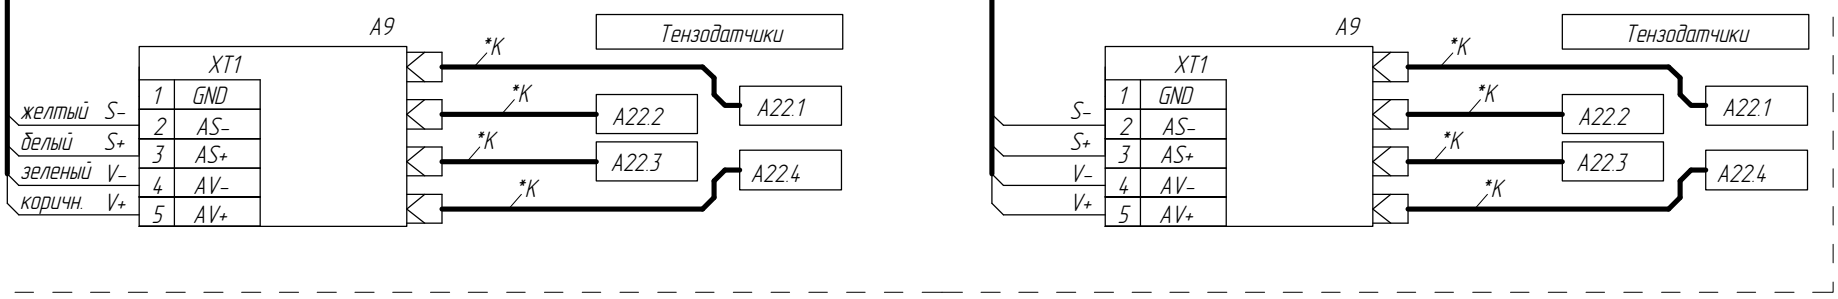


*К – Кабель в комплекте с устройством
*ВМП – подключение показано для лифтов с верхним машинным помещением
*НМП – подключение показано для лифтов с нижним машинным помещением

| Изм | Лист | № докум. | Подп. | Дата | ФАИД.484440.002 Э4 | Лист 21 |
|---|---|---|---|---|---|---|
| 7 | | 186.013823-2025 | | | | |

Перв. примен.
Справ. №
Подп. и дата
Инв.№ дубл.
Взам. инв. №
Подп. и дата
Черенкова (Подп) 19.12.2025
Инв.№ подл. 4031

IPS ID: 110655800

Список цехов-расцеховок нет.

Копировал

Формат А3

# Подключение устройств контроля загрузки кабины


## Взвешивающее устройство на кабине
## (для лифтов с верхним машинным помещением и г/п 500 кг)


ФБИР.484440.002 Э4

Устройство грузовзвешивающее ГУ-01 "Зенит"

Устройство контроля загрузки УКЗ-ВТ

Щит управления АК'

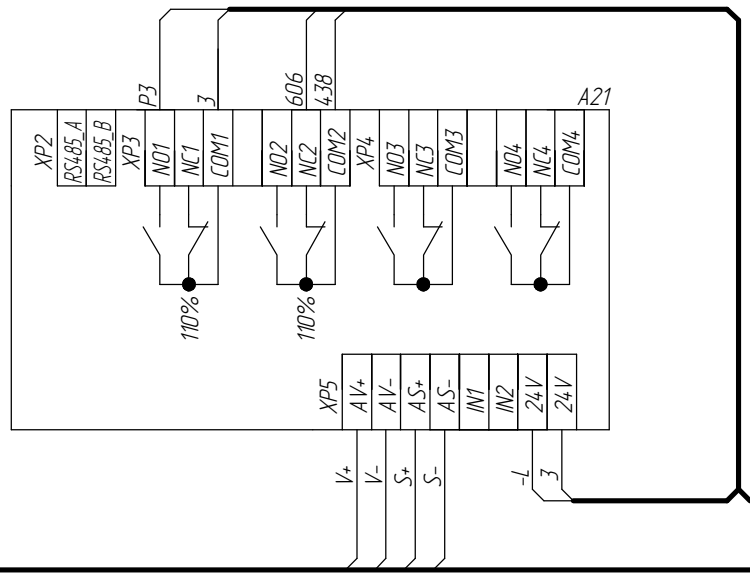

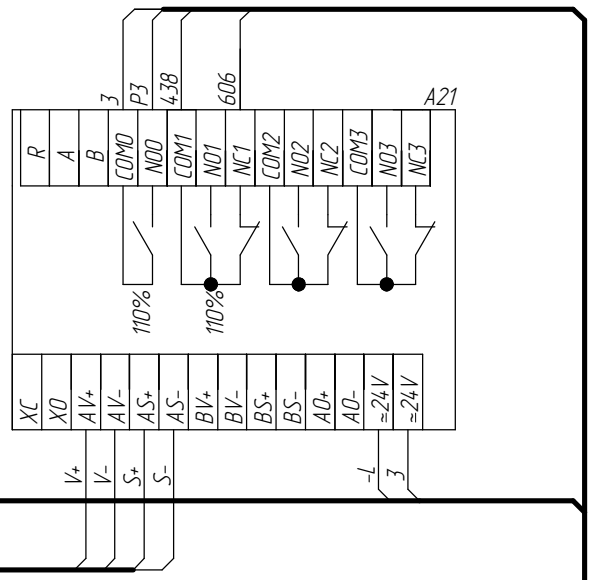
*K


XT34


| марк. | конт. | марк. |
|---|---|---|
| 438 | 5 | 438 |
| 606 | 6 | 606 |
| P3 | 7 | P3 |

XT31

| марк. | конт. | марк. |
|---|---|---|
| 3 | 4 | 3 |
| -L | 10 | -L |

Нижняя балка кабины

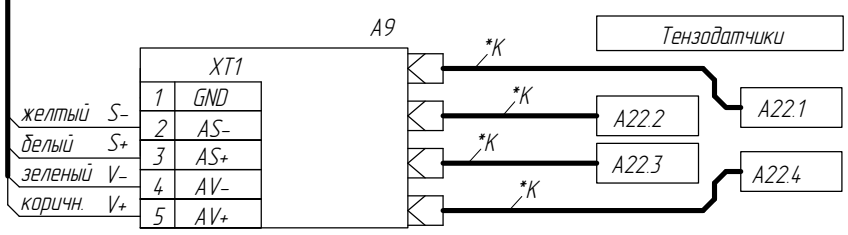

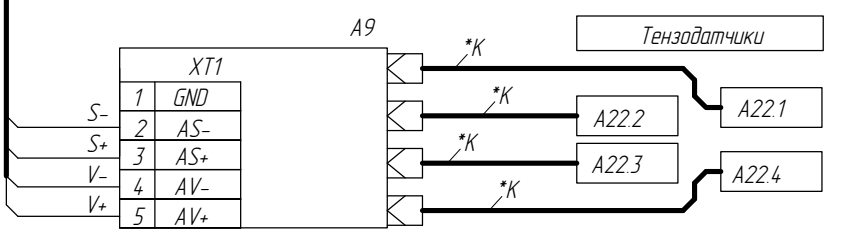
*K – Кабель в комплекте с устройством

| Изм | Лист | № докум. | Подп. | Дата | ФБИР.484440.002 Э4 | Лист 21а |
|---|---|---|---|---|---|---|
| 7 | | 186.013823-2025 | | | | |

Инв.№ подл. 4031 | Подп. и дата Черенкова (Подп) 19.12.2025 | Взам. инв. № | Инв.№ дубл. | Подп. и дата | Справ. № | Перв. примен.

IPS ID: 110655800 Список цехов-расцеховок нет. Копировал Формат А3

# Подключение устройств связи

ФАИД.484440.002 Э4

Устройство УЛ

Устройство переговорное — A26.1

*К

XT2A

| марк. | конт. | марк. |
|---|---|---|
| 153 | 1 | 153 |

XT4A

| марк. | конт. | марк. |
|---|---|---|
| 3 | 22 | 3 |
| -L | 23 | -L |

Кабина лифта

Пост кнопочный ревизии на крыше кабины АК2

Устройство абонентское лифтовое диспетчерское — A18 — XS5 — "Дисп."

| | | | |
|---|---|---|---|
| 1 | 1 | D1 | D1 |
| 2 | 2 | D4 | D4 |
| 3 | 3 | M1 | M1 |
| 4 | 4 | M4 | M4 |
| 5 | 5 | L318 | L318 |
| 6 | 6 | L319 | L319 |

Устройство переговорное — A26.2 — XS2

| | | |
|---|---|---|
| 7 | 3 | |
| 8 | 153 | |
| 9 | -L | |

*К

Щит управления АК'

XT31

| марк. | конт. | марк. |
|---|---|---|
| 153 | 1 | 153 |
| | 2 | |
| 3 | 3 | 3 |
| 3 | 4 | 3 |
| 3 | 5 | 3 |
| 3 | 6 | 3 |
| -L | 7 | -L |
| -L | 8 | -L |
| -L | 9 | -L |
| -L | 10 | -L |

XT34

| марк. | конт. | марк. |
|---|---|---|
| D1 | 1 | D1 |
| D4 | 2 | D2 |
| M1 | 3 | M1 |
| M4 | 4 | M2 |
| 438 | 5 | 438 |
| 606 | 6 | 606 |
| L318 | 9 | L318 |
| L319 | 10 | L319 |

ГВ0505.12.00.050 Трасса №4.1

ГВ0505.12.00.030 Пучок 1

в шахту

Трасса №4.2 — 15, 16, 8

ГВ0505.12.00.050-01

3, 153, -L

в кабину

ПУЧОК 1 — 16, 17, 16

-L, 153, 3

ГВ0505.12.00.030

Блок приямка

Устройство переговорное — A26.3 — XS3

| | |
|---|---|
| 7 | 3 |
| 8 | 153 |
| 9 | -L |

МКШВ 7х0,75

XT1

| | |
|---|---|
| 1 | L315 |
| 2 | L313 |
| 3 | 153 |
| 4 | -L |
| 5 | 3 |
| 6 | N3 |

* К – Кабель в комплекте с устройством

| Изм | Лист | № докум. | Подп. | Дата | 186.013823-2025 | ФАИД.484440.002 Э4 | Лист 22 |
|---|---|---|---|---|---|---|---|

Перв. примен.

Справ. №

Подп. и дата

Инв.№ дубл.

Взам. инв. №

Подп. и дата (Подп) Черенкова 19.12.2025

Инв.№ подл. 4031

IPS ID: 110655800

Список цехов-расцеховок нет.

Копировал

Формат А3